



Департамент капитального ремонта города Москвы Государственное автономное учреждение города Москвы Московский научно-исследовательский и проектный институт жилищного хозяйства «МосжилНИИпроект» (ГАУ «МосжилНИИпроект»)

mgnp@mgnp.mos.ru +7 495 624 40 65 107078, г. Москва, ул. Каланчевская, д. 4/2, стр. 1

Арх. №

**Капитальный ремонт здания,
расположенного по адресу:
г. Москва, улица Мясницкая, дом 44, стр. 1**

ПРОЕКТНАЯ ДОКУМЕНТАЦИЯ

**Раздел 5. Сведения об инженерном оборудовании,
о сетях и системах инженерно-технического обеспечения.**

Подраздел 5. Сети связи

Часть 2. Система оповещения и управления эвакуацией

Том 5.5.2

2025-00224-01-0-ИОС5.2

**Капитальный ремонт здания,
расположенного по адресу:
г. Москва, улица Мясницкая, дом 44, стр. 1**

ПРОЕКТНАЯ ДОКУМЕНТАЦИЯ

**Раздел 5. Сведения об инженерном оборудовании,
о сетях и системах инженерно-технического обеспечения.**

Подраздел 5. Сети связи

Часть 2. Система оповещения и управления эвакуацией

Том 5.5.2

2025-00224-01-0-ИОС5.2

Начальник ОПИС №1

ГИП



Д.П. Белоусова

07.04.2026

В.Ю. Гунченко

07.04.2026

Содержание раздела

№п/п	Наименование проектных материалов	Марка листа	Стр.
1	Содержание раздела		
2	Состав проектной документации		
3	Текстовая часть		
4	Условные обозначения	ИОС5.2-1	
5	Принципиальная схема СОУЭ	ИОС5.2-2	
6	План 1-го этажа СОУЭ	ИОС5.2-3	
7	План 2-го этажа СОУЭ	ИОС5.2-4	
8	Спецификация оборудования и материалов	ИОС5.2-С	

Согласовано

Взам. Инв. №

Подп. И дата

Инв. № подл.

Изм.	Кол.уч	Лист	Недок.	Подп.	Дата
Разработал		Короткова К.Н.			03.2026
Зав.сектор.		Роянцева А.А.			03.2026
И.контр.		Роянцева А.А.			03.2026
Нач. ОПИС№1		Белоусова Д.П.			03.2026

2025-00224-01-0-ИОС5.2-С

Капитальный ремонт
здания по адресу
г.Москва, ул.Мясницкая, д.44, стр.1

Стадия	Лист	Листов
П	1	1



Состав проектной документации

Смотри том 1.1, 2025-00224-01-0-СП, Часть1. Раздел1. Состав проектной документации.

Инв. № подл.	Подп. и дата	Взам. инв. №							Лист
Изм.	Коп.уч	Лист	Недок	Подп.	Дата	2025-00224-01-0-ИОС5.2-С			2

Пояснительная записка.

Капитальный ремонт здания по адресу: г. Москва, ул. Мясницкая, д.44, стр.1. Часть помещений не входят в область капитального ремонта.

Здание двухэтажное с неотапливаемым чердаком.

1. Назначение системы оповещения.

Система оповещения и управления эвакуацией людей при пожаре (СОУЭ) 3 типа с возможностью трансляции сообщений (кроме сообщений о пожаре) через микрофон пульта. СОУЭ предназначена для оповещения находящихся в здании людей о возникшем пожаре и организации их своевременной эвакуации, путем трансляции речевой информации в помещениях, о необходимости эвакуации, путях эвакуации и других действиях, направленных на обеспечение безопасности.

- включение от командного импульса, формируемого автоматической установкой пожарной сигнализации или пожаротушения посредством подключения к адресной линии связи;
- СОУЭ сопряжена с системой ГО и ЧС сетью здания с приоритетом оповещения через оборудование шкафа УС-1 (Том 2025-00224-01-0-ИОС5.3).

Система речевого оповещения марки Рубеж принята в составе:

- Прибор управления оповещением Sonar SPM-A01025-AW предназначен для приема командных импульсов, формируемых автоматической установкой пожарной сигнализации, и выдачи команд и электрических сигналов в систему звукового оповещения, подачу основного или резервного питания на усилитель мощности.

Система светового оповещения (включая МГН) представлена в томе «Автоматическая пожарная сигнализация» 2025-00224-01-0-ИОС5.1.

Основное питание прибора управления осуществляется от сети переменного тока 220В.

В соответствии с требованиями ч.11 ст.84 № 123-ФЗ система оповещения о пожаре и управления эвакуацией людей оборудована источниками бесперебойного электропитания. В соответствии с ч.4 ст.103 № 123-ФЗ технические средства автоматических установок пожарной сигнализации и технические средства систем передачи извещений обеспечены бесперебойным электропитанием на время выполнения ими своих функций. Выполнение указанных требований обеспечивается посредством применения источников бесперебойного электропитания со встроенными аккумуляторными батареями. Переход с основного на резервное питание происходит автоматически при пропадании основного питания.

Резервное питание обеспечивает аккумулятор, установленный в блок резервного питания Sonar SPM-Box.

Согласовано			
Взам. Инв. №			
Подп. И дата			
Инв. № подл			

						2025-00224-01-0-ИОС5.2-ПЗ		
Изм.	Кол.уч	Лист	№док.	Подп.	Дата	Капитальный ремонт здания по адресу г.Москва, ул.Мясницкая, д.44, стр.1  МОСЖИЛ НИИПРОЕКТ		
Разработал		Короткова К.Н.			03.2026			
Зав.сектор.		Роянцева А.А.			03.2026			
Н.контр.		Роянцева А.А.			03.2026			
Нач. ОПИС№1		Белоусова Д.П.			03.2026			
						Стадия	Лист	Листов
						П	1	4

Для выполнения СП 484.1311500.2020 изм.1 в частности п. 5.4 прибор комплектуется изолаторами шлейфа ИЗ-1-R, установленными на Sonar-Cover.

Система оповещения имеет одну зону / 2 линии оповещения (1 этаж и 2 этаж).

Суммарная мощность по зонам оповещения:

- 1 зона 66,0 Вт;

Оборудование СОУЭ обеспечивает выполнение основных функций:

- подача звуковых (речевых) сигналов в помещения объекта оповещения с постоянным или временным пребыванием людей;

- трансляцию текстов (голосовое сообщение в микрофон) о необходимости эвакуации, путях эвакуации, направлении движения и других действиях, направленных на обеспечение безопасности людей и распределением сигналов оповещения;

- автоматической трансляцией специально разработанных текстов (речевое сообщение, записанное на магнитофон), направленных на предотвращение паники и других явлений;

Система речевого оповещения марки «Sonar» принята в составе:

- Прибор управления «Sonar SPM-A01025-AW» настенного исполнения на 1 зону предназначен для приема командных импульсов, формируемых автоматической установкой пожарной сигнализации, и выдачи команд и электрических сигналов в систему звукового оповещения, подачу основного или резервного питания.

Основное питание усилителя осуществляется от сети переменного тока 220В. Резервное питание 24В обеспечивается от внешнего блока резервного питания.

- Для организации резервного питания для настенной версии моноблока предусмотрен блок Sonar SPM-Vox, в котором размещены два АКБ 12В емкостью 40Ач. Блок резервного питания предназначен для обеспечения резервным питанием (24В пост. тока) усилителя мощности, входящего в состав системы звукового оповещения. В случае полного отключения напряжения 220В, аккумуляторные батареи позволяют работать оборудованию в течение 24 часов в дежурном режиме и 1 часа в режиме тревоги.

- Речевые пожарные извещатели «Sonar SCS-103» потолочные и «Sonar SWP-103» настенные предназначены для воспроизведения голосовых сообщений, специальных сигналов в системах пожарного оповещения, речевой информации в системах: громкоговорящей связи, звукоусиления и трансляции. Мощность – 1,5/3 Вт. Установить извещатели на этажах, согласно проекту.

- Пульт микрофонный Sonar SRM-7001 на 1 зону установлен на посту охраны пом.101А.

В линейке оборудования Sonar Rubezh контроль линии до последнего динамика осуществляет оконечный фильтр Sonar SFT-2300.

Взам. инв. №	Подп. и дата	Инв. № подл.							Лист	
			2025-00224-01-0-ИОС5.2-ПЗ							2
			Изм.	Кол.уч	Лист	Недок	Подп.	Дата		

Главное оборудование СОУЭ устанавливается на стене в серверной (пом.222).

2. Звуковые сигналы СОУЭ обеспечивают общий уровень звука (уровень звука постоянного шума вместе со всеми сигналами, производимыми оповещателями) не менее 75 дБА на расстоянии 3 м от оповещателя, но не более 120 дБА в любой точке защищаемого помещения.

П.4.2 Звуковые сигналы СОУЭ обеспечивают уровень звука не менее чем на 15 дБА выше допустимого уровня звука постоянного шума в защищаемом помещении. Измерение уровня звука должно проводиться на расстоянии 1,5 м от уровня пола.

П.4.4 Настенные звуковые и речевые оповещатели располагать таким образом, чтобы их верхняя часть была на расстоянии не менее 2,3 м от уровня пола, но расстояние от потолка до верхней части оповещателя должно быть не менее 150 мм.

П.4.6 Речевые оповещатели воспроизводят нормально слышимые частоты в диапазоне от 200 до 5000 Гц. Уровень звука информации от речевых оповещателей соответствуют нормам настоящего свода правил применительно к звуковым пожарным оповещателям.

П.4.7 Установка громкоговорителей и других речевых оповещателей в защищаемых помещениях исключает концентрацию и неравномерное распределение отраженного звука.

П.4.8 Количество звуковых и речевых пожарных оповещателей, их расстановка и мощность обеспечивает уровень звука во всех местах постоянного или временного пребывания людей в соответствии с нормами настоящего свода правил.

Кабели, провода СОУЭ и способы их прокладки обеспечивают работоспособность соединительных линий в условиях пожара в течение времени, необходимого для полной эвакуации людей в безопасную зону п.3.4 СПЗ.13130.2009.

В соответствии с требованиями п.5.2.4 СП 2.13130.2020, места пересечения кабелей, кабеленесущих конструкций со строительными конструкциями с нормируемыми пределами огнестойкости, обеспечиваются проходками не ниже пределов огнестойкости, установленных для пересекаемых конструкций посредством установки гильз из труб с заделкой гидроизоляционной огнеупорной мастикой в соответствии с ГОСТ 30247.1, ГОСТ Р 53306, ГОСТ Р 53310.

3. Электропитание и заземление оборудования.

Питание СОУЭ осуществляется по 1-й категории надежности в соответствии с ПУЭ. 1-я категория надежности обеспечивается за счет применения источников бесперебойного питания. Переход с основного питания на резервное осуществляется автоматически. От отдельного автоматического выключателя щита электроснабжения питание прибор.

Все оборудование системы СОУЭ заземлить.

Изм.	Кол.уч	Лист	Недок	Подп.	Дата	2025-00224-01-0-ИОС5.2-ПЗ	Лист
							3
Изм.	Кол.уч	Лист	Недок	Подп.	Дата		

Соединение оборудования системы произвести кабелями в соответствии с технической документацией. Монтаж элементов системы производить по мере строительной готовности. Разводка системы эвакуационного оповещения производится кабелем КПСнг-FRHF 1x2x1,5 в трубе гофрированной ПВХ за фальшпотолком и в штробах по стенам под потолком. Микрофонный пульт подключается к прибору кабелем ParLan U/UTP Cat5e PVCLSn2(A)-FRHF 4x2x0,52.

4. Для обеспечения безопасности людей электрооборудование должно быть надежно заземлено (занулено) в соответствии с требованиями ПУЭ и паспортными требованиями на электрооборудование.

В помещениях, не вошедших в зону капитального ремонта, необходимо при монтаже сохранить работоспособность системы СОУЭ.

Перечень нормативных документов, использованных при разработке проектной документации.

ГОСТ Р 21.101-2020 «Система проектной документации для строительства (СПДС). Основные требования к проектной и рабочей документации». Постановление №87 от 16.02.2008 «О составе разделов проектной документации и требования к их содержанию» (с изменениями на 23 января 2016г.)

ГОСТ 27990-88 Средства охранной, пожарной и охранно- пожарной сигнализации. Общие технические требования.

СП 3.13130.2009 Система оповещения и эвакуации людей при пожаре. Требования пожарной безопасности.

СП 484.1311500.2020 изм.1 СИСТЕМЫ ПОЖАРНОЙ СИГНАЛИЗАЦИИ И АВТОМАТИЗАЦИЯ СИСТЕМ ПРОТИВОПОЖАРНОЙ ЗАЩИТЫ


СП 133.13330.2012 СЕТИ ПРОВОДНОГО РАДИОВЕЩАНИЯ И ОПОВЕЩЕНИЯ В ЗДАНИЯХ И СООРУЖЕНИЯХ. НОРМЫ ПРОЕКТИРОВАНИЯ

СП 6.13130.2021 Электрооборудование. Требования пожарной безопасности. ГОСТ 31565-2012 Кабельные изделия. Требования пожарной безопасности.


ПУЭ изд.7 "Правила устройства электроустановок"

Изм.	Кол.уч	Лист	Недок	Подп.	Дата	2025-00224-01-0-ИОС5.2-ПЗ	Лист
							4
Изм.	Кол.уч	Лист	Недок	Подп.	Дата		

[illegible]

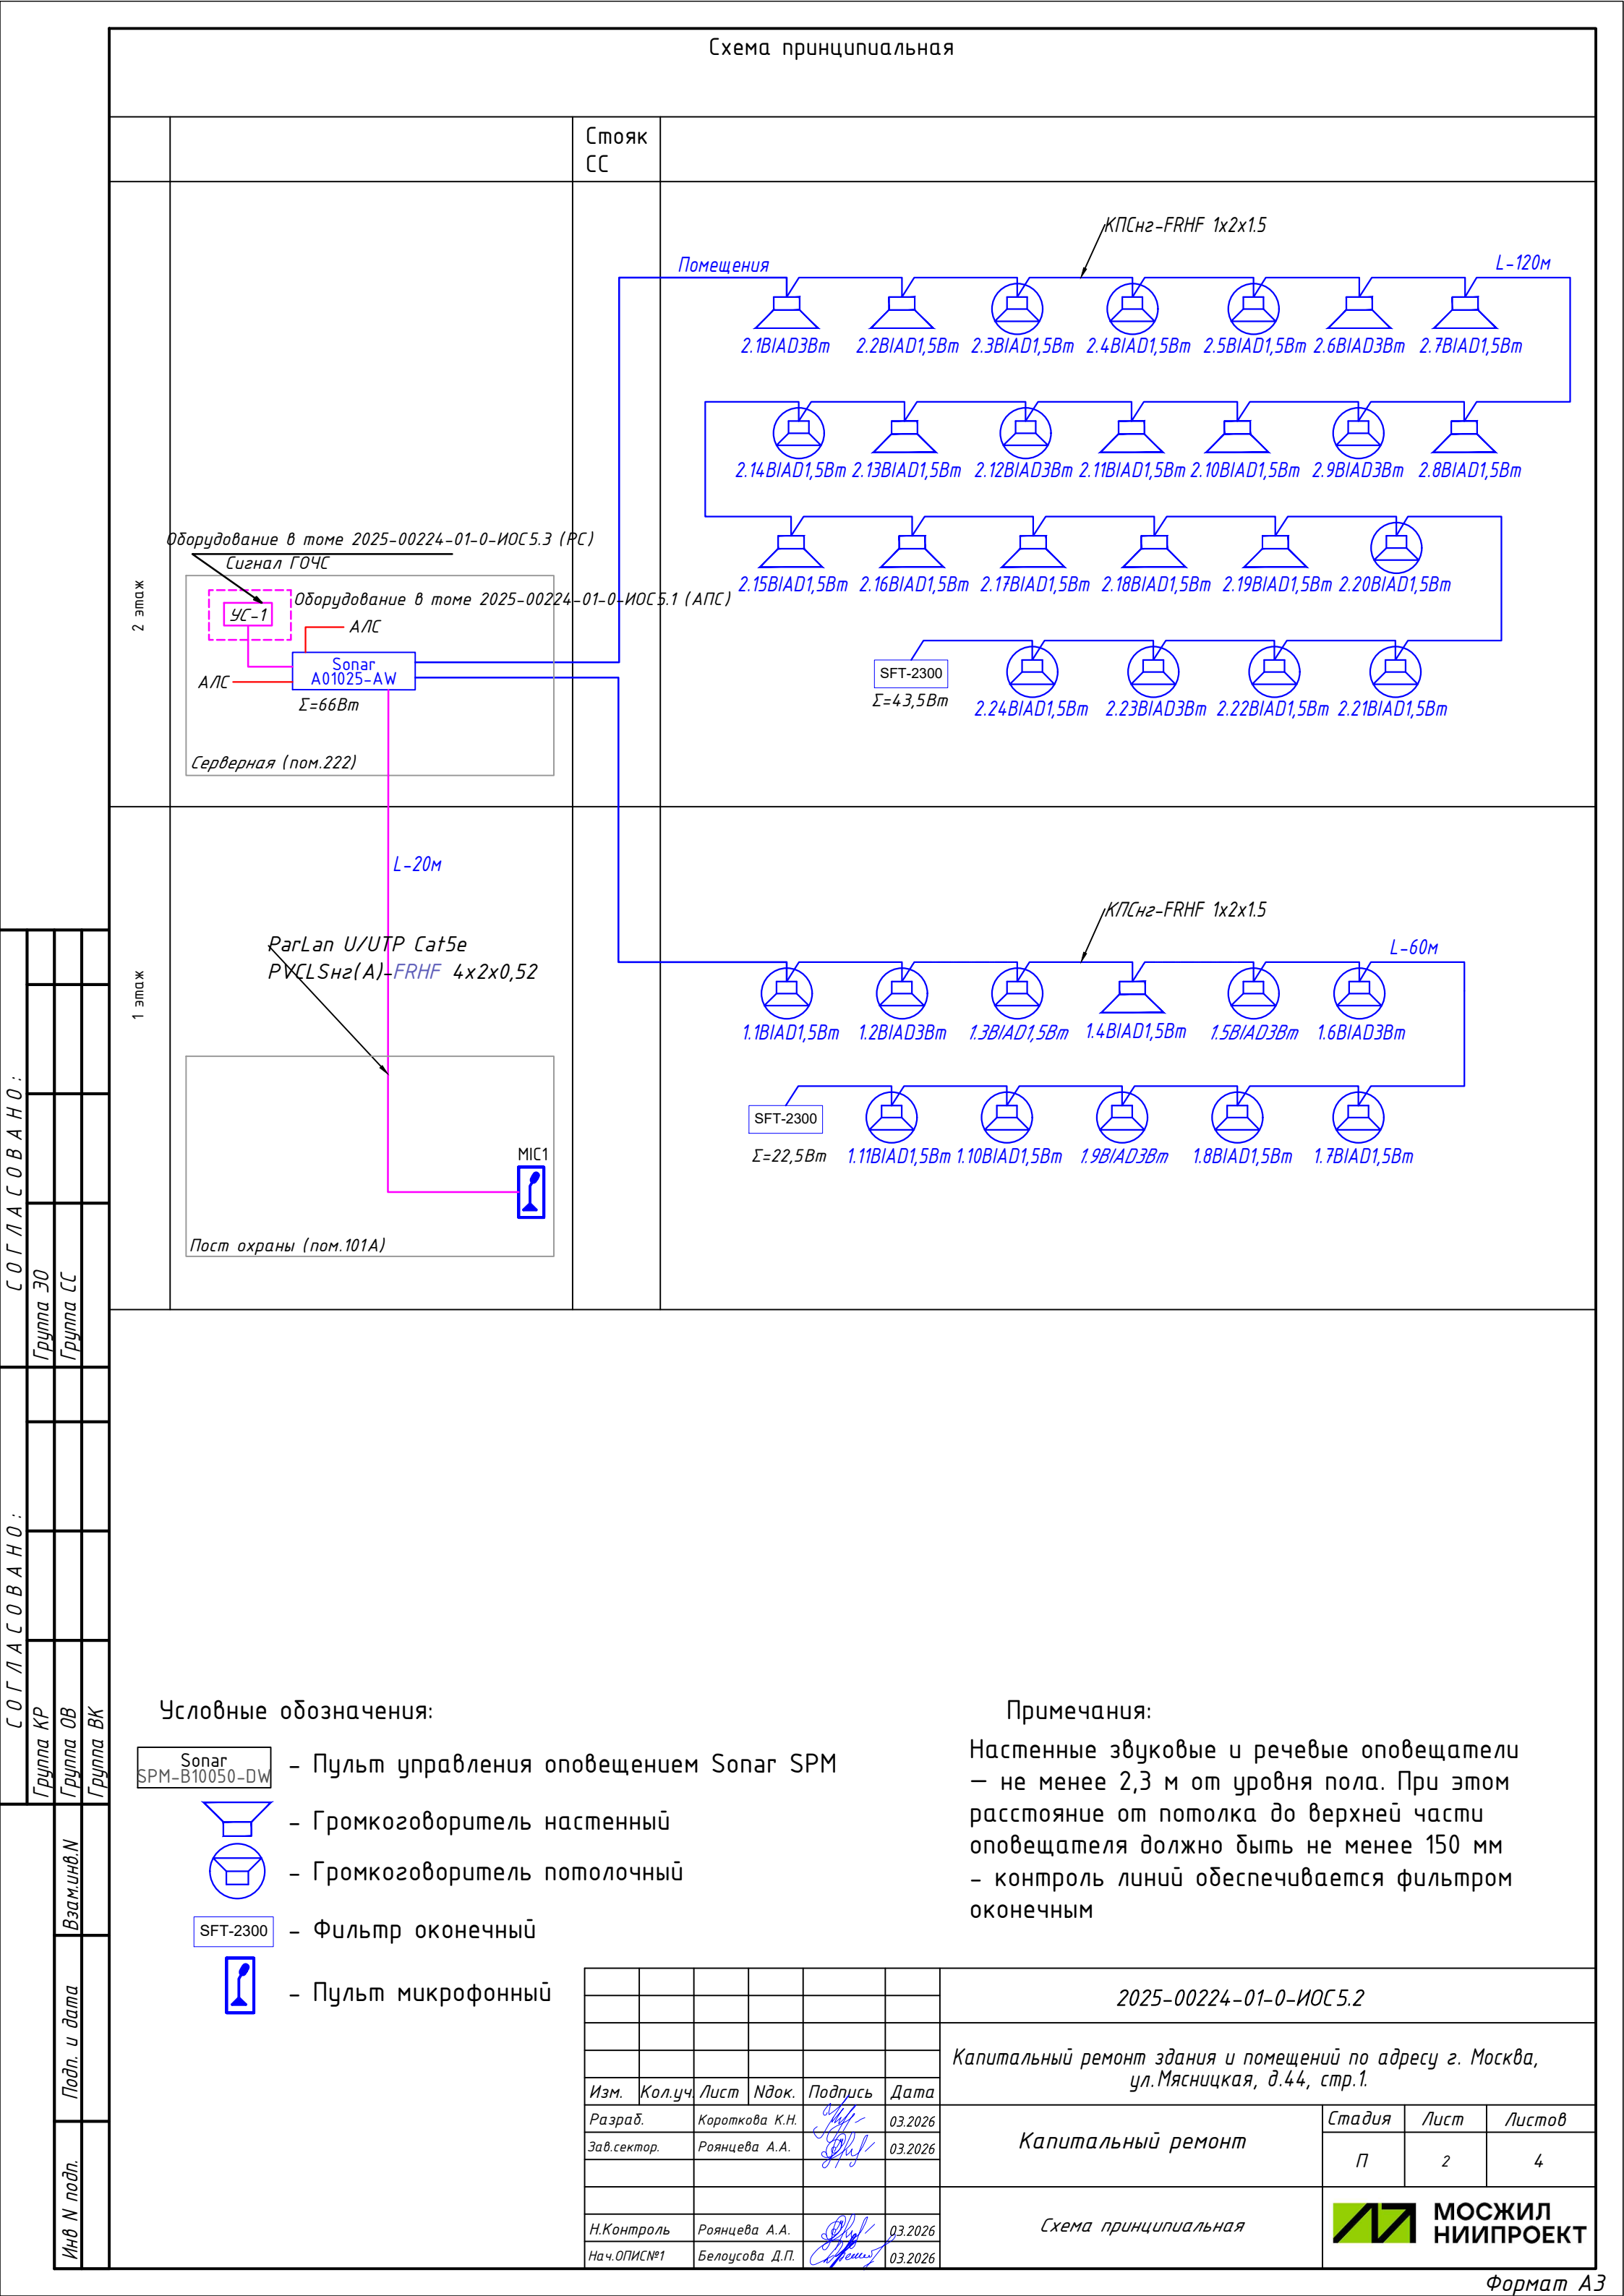

План 1-го этажа на отм. 0.000
М 1:100

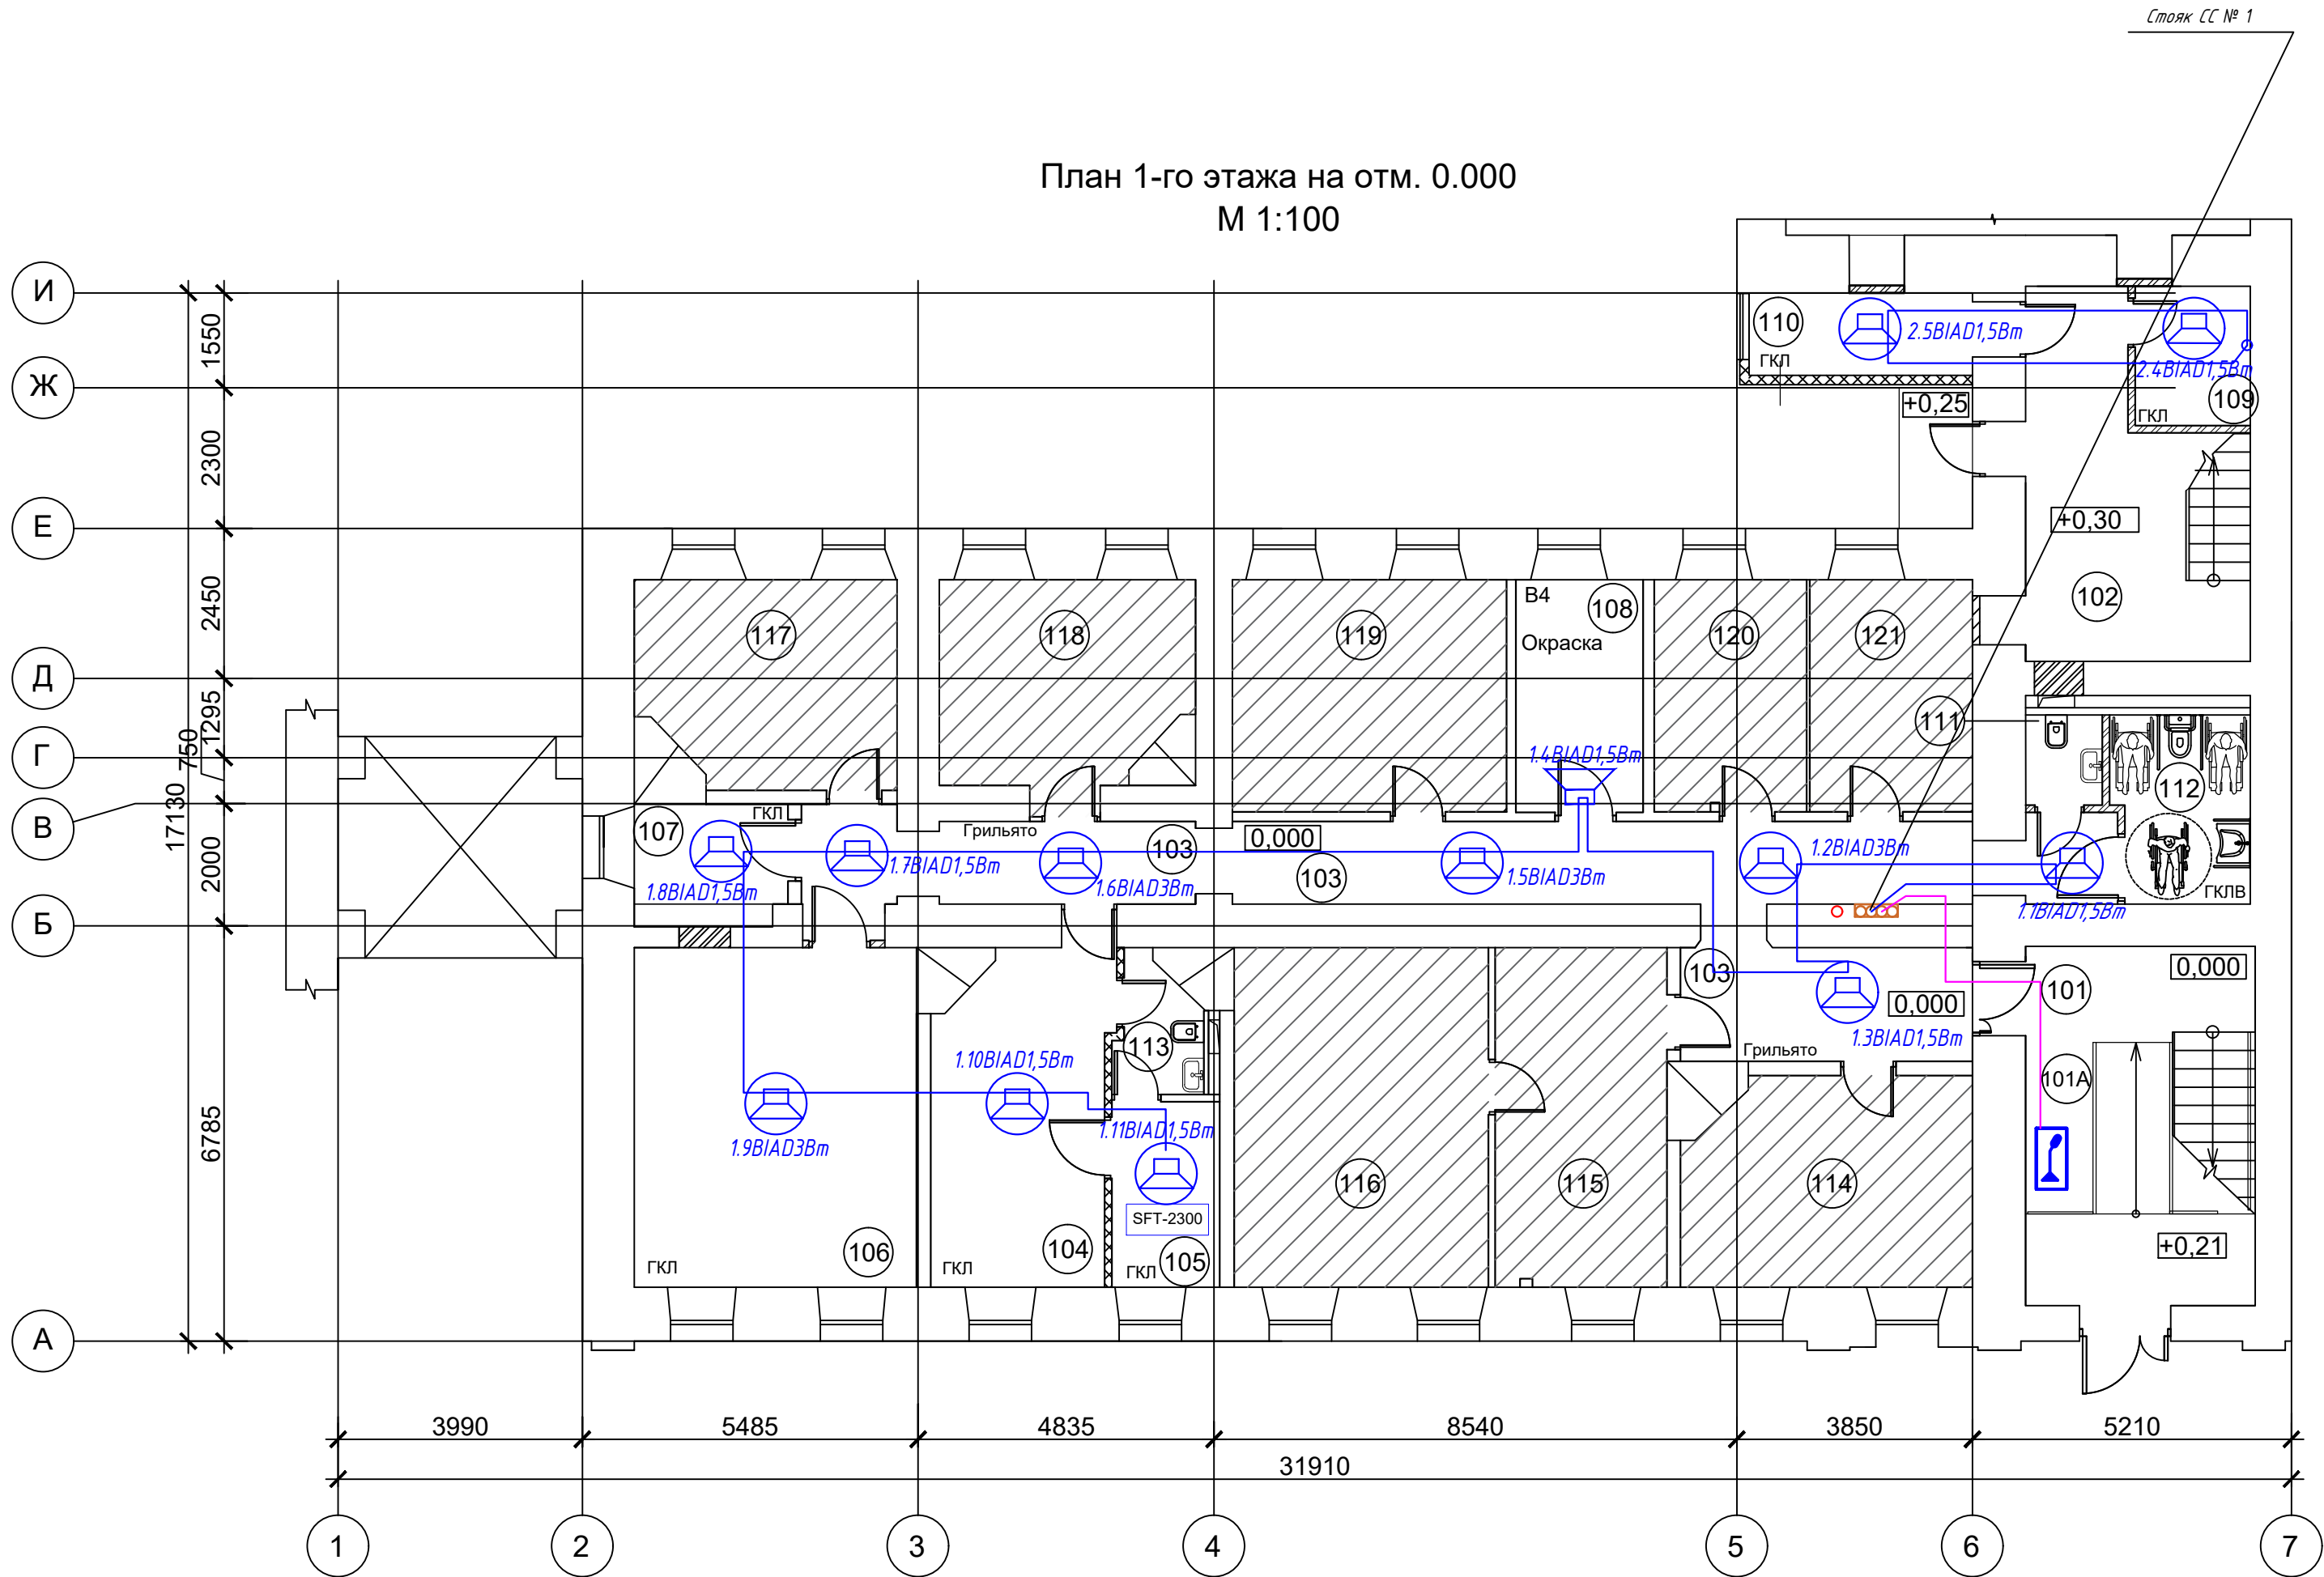

помещения не подлежащие капитальному ремонту

Экспликация помещений 1-го этажа			
N п/п	Наименование помещений	Площадь м²	Кат. пом.
101	Лестница №1 (ЛК ти 1)	22,9	
101А	Пост охраны		
102	Лестница № 2 (ЛК тип 1)	17,7	
103	Коридор	39,4	
104	Кабинет заместителя прокурора	15,9	
105	Комната отдыха заместителя прокурора	5,3	
106	Кабинет помощника прокурора / прием граждан МГН	25,6	
107	Кабинет*	4,8	
108	Архив	7,9	В4
109	Ввод водопровода	4,3	
110	Кабинет для приема граждан	4,9	
111	Санузел	1,8	
112	Санузел МГН	6,7	
113	Санузел заместителя прокурора	2,8	
ИТОГО:		160	


Помещения не входящие в зону ремонта			
N п/п	Наименование помещений	Площадь м²	Кат. пом.
114	Офисное помещение	15,7	
115	Офисное помещение	15,6	
116	Офисное помещение	23,0	
117	Офисное помещение	13,8	
118	Офисное помещение	13,8	
119	Офисное помещение	17,0	
120	Офисное помещение	9,4	
121	Офисное помещение	10,1	
ИТОГО:		118,4	

* - кабинет для работы с секретными документами

Условные обозначения:

- Пульт управления оповещением Sonar SPM
- Громкоговоритель настенный
- Громкоговоритель потолочный
- Фильтр оконечный
- Пульт микрофонный

						2025-00224-01-0-ИОС 5.2			
						Капитальный ремонт здания и помещений по адресу г. Москва, ул.Мясницкая, д.44, стр.1.			
Изм.	Кол.уч	Лист	Ндок.	Подпись	Дата	Капитальный ремонт	Стадия	Лист	Листов
Разраб.		Короткова К.Н.			03.2026		П	3	4
Зав.сектор.		Роянцева А.А.			03.2026				
						План 1-го этажа Расстановка оповещателей			МОСЖИЛ НИИПРОЕКТ
Н.Контроль		Роянцева А.А.			03.2026				
Нач.ОПИС №1		Белоусова Д.П.			03.2026				

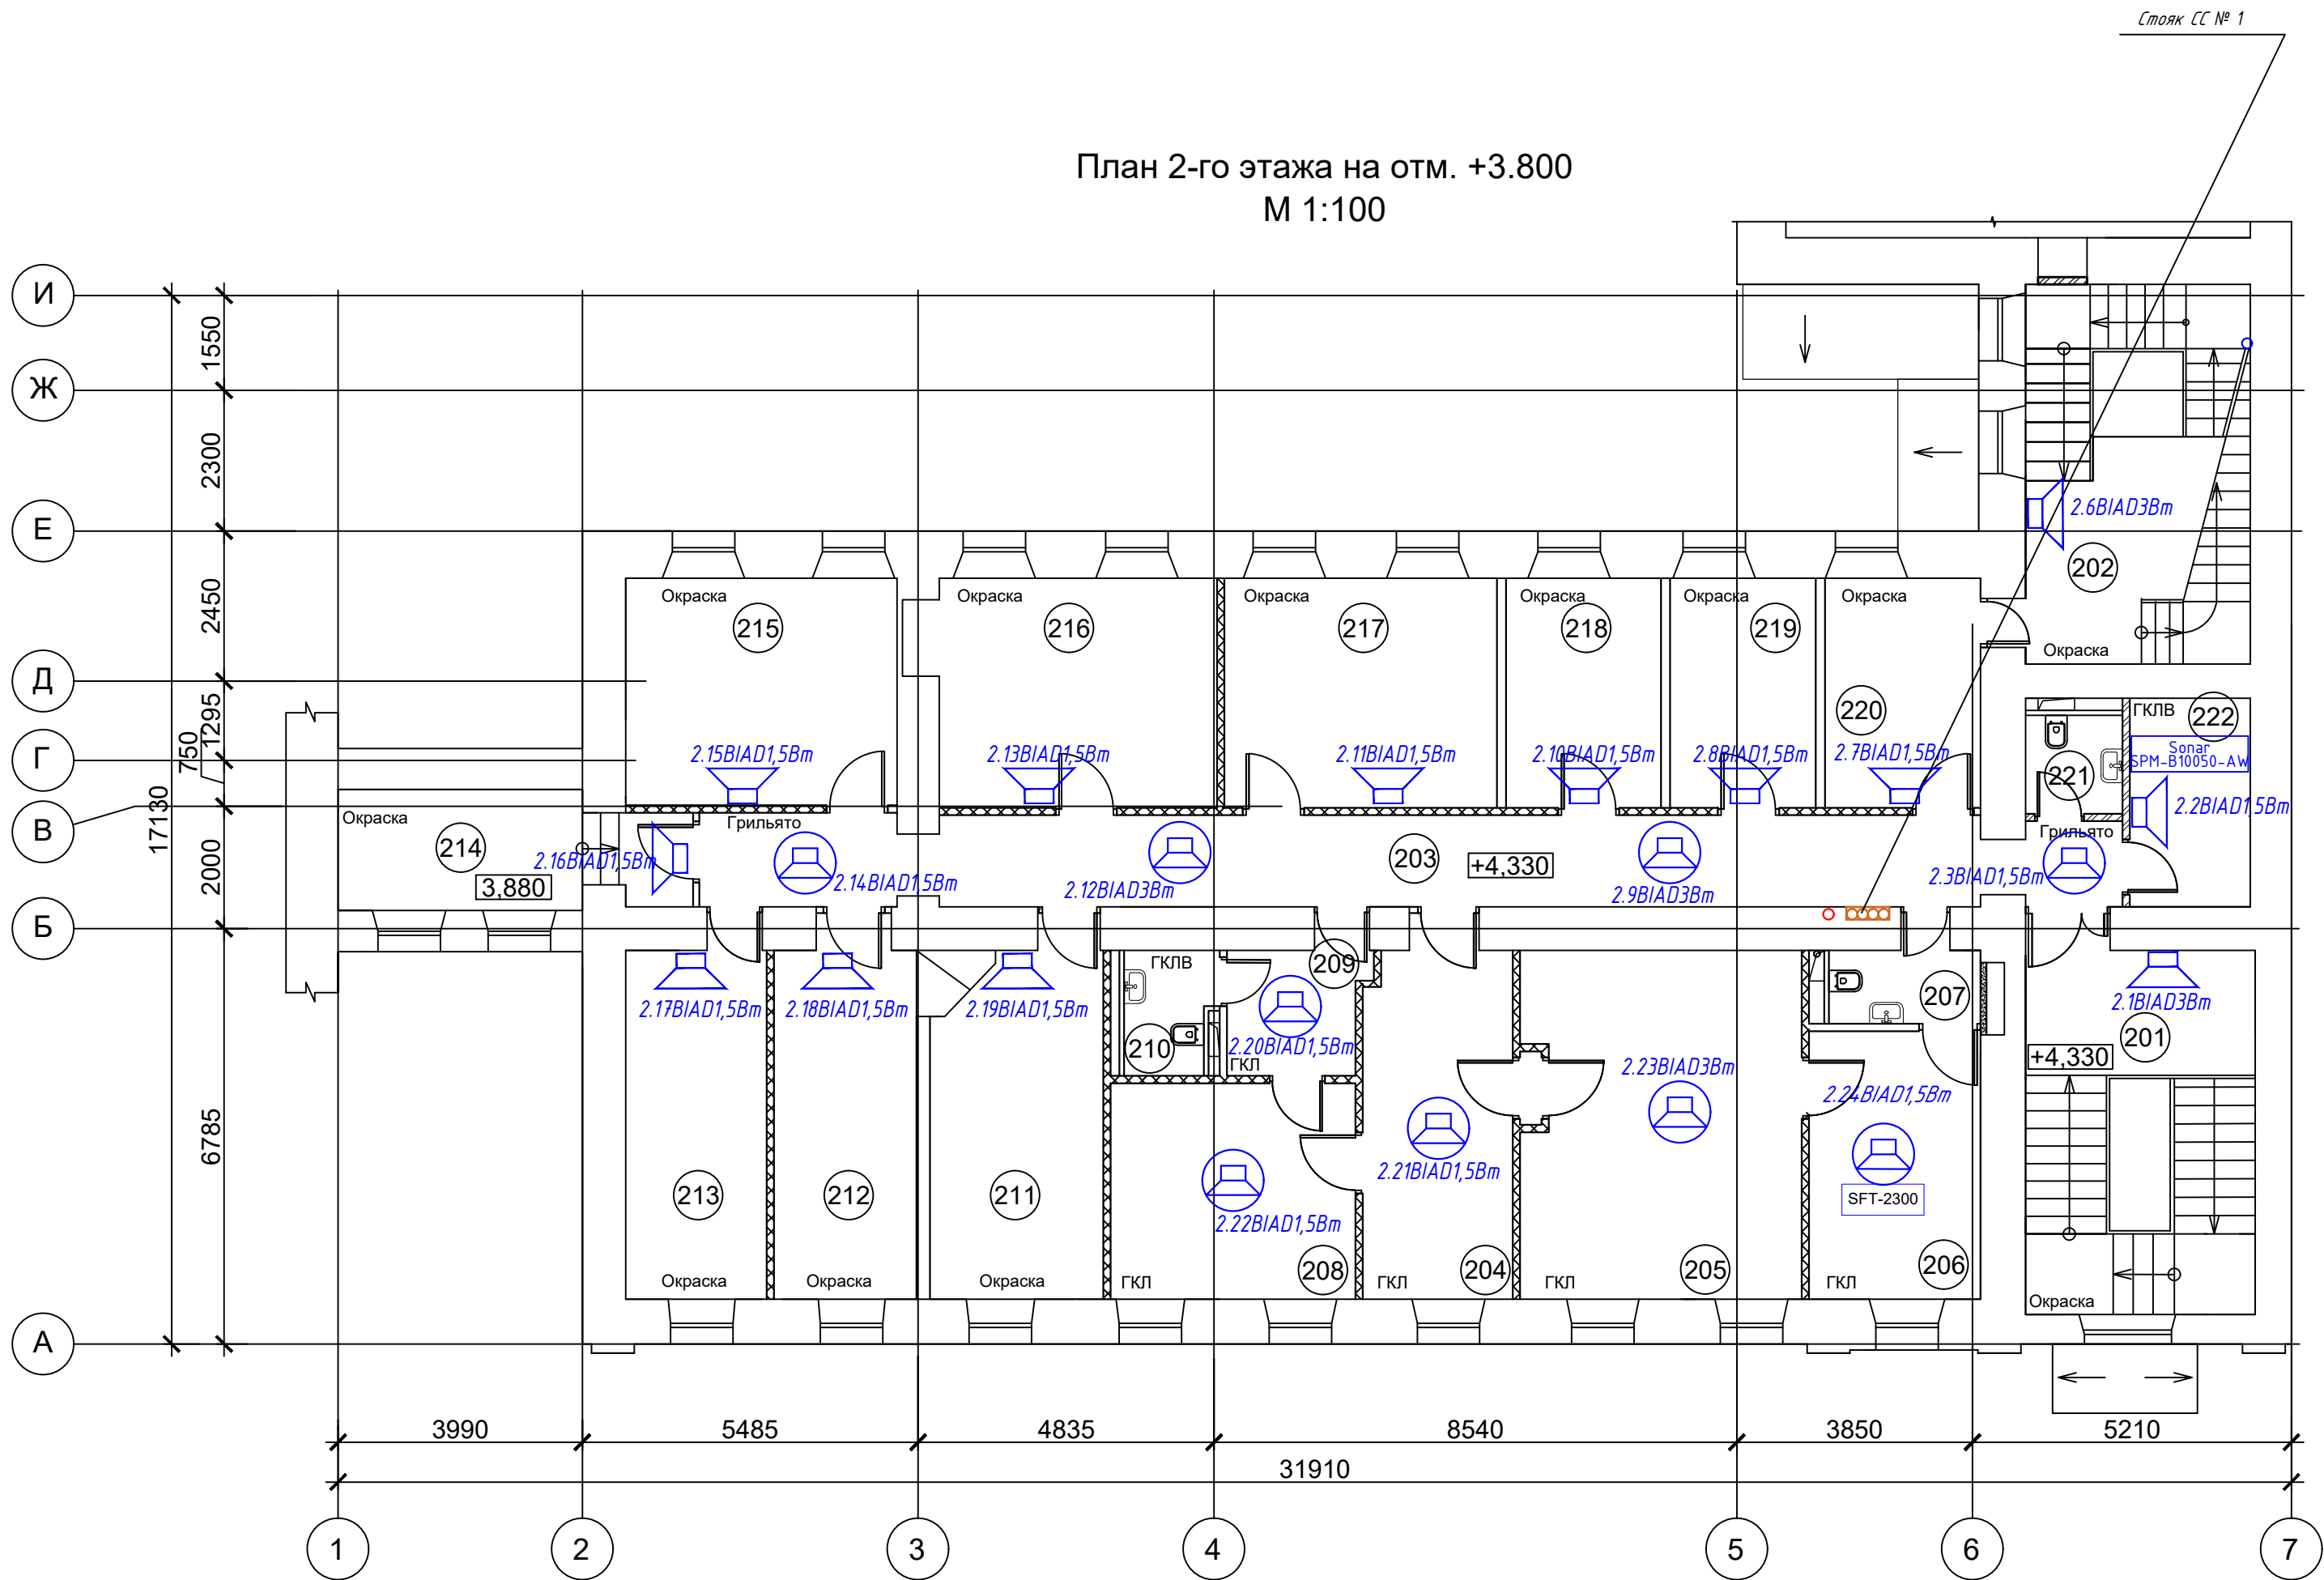

Экспликация помещений 2-го этажа			
N п/п	Наименование помещений	Площадь м²	Кат. пом.
201	Лестница № 1 (ЛК тип 1)	23,1	
202	Лестница № 2 (ЛК тип 1)	22,8	
203	Коридор	34,2	
204	Приемная прокурора	14,5	
205	Кабинет прокурора / видеонаблюдение	25,9	
206	Комната отдыха прокурора	12,3	
207	Сан. узел прокурора	3,5	
208	Кабинет 1-го заместителя прокурора	14,1	
209	Комната отдыха 1-го заместителя прокурора	5,0	
210	Сан. узел 1-го заместителя прокурора	2,6	
211	Кабинет помощника прокурора	15,9	
212	Кабинет помощника прокурора	14,0	
213	Кабинет помощника прокурора	13,7	
214	Архив	10,3	ВЗ
215	Кабинет помощника прокурора	16,4	
216	Кабинет помощника прокурора	17,0	
217	Зал совещаний	16,7	
218	Кабинет помощника прокурора	9,5	
219	Кабинет помощника прокурора	8,9	
220	Комната прирема пищи	9,5	
221	Санузел	2,5	
222	Серверная	7,6	ВЗ
Итого:		300	

- Условные обозначения:
- Пульт управления оповещением Sonar SPM
 - Громкоговоритель настенный
 - Громкоговоритель потолочный
 - Фильтр оконечный
 - Пульт микрофонный

						2025-00224-01-0-ИОС 5.2			
						Капитальный ремонт здания и помещений по адресу г. Москва, ул. Мясницкая, д. 44, стр. 1.			
Изм.	Кол.уч.	Лист	Изд.	Подпись	Дата	Капитальный ремонт	Стадия	Лист	Листов
Разраб.	Короткова К.Н.	03.2026					П	4	4
Зав.сектор.	Роянцева А.А.	03.2026							
Н.Контроль	Роянцева А.А.	03.2026				План 2-го этажа Расстановка оповещателей			
Нач.ОПИС №1	Белоусова Д.П.	03.2026							

Позиция	Наименование и техническая характеристика	Тип, марка, обозначение документа, опросного листа	Код оборудования, изделия, материала	Завод-изготовитель	Единица измерения	Количество	Масса единицы, кг	Примечание
1	2	3	4	5	6	7	8	9
	СОУЭ							
1	Прибор управления оповещением Sonar	SPM-A01025-AW			шт	1		
2	Пульт микрофонный	Sonar SRM-7001C			шт	1		
3	Оповещатель настенный 3/1,5Вт	Sonar SWP-103			шт	14		
4	Оповещатель потолочный 3/1,5Вт	Sonar SCS-103			шт	21		
5	Фильтр оконечный	SFT-2300-M			шт	2		
6	Блок резервного питания	Sonar SPM-Box			шт	1		
7	Аккумуляторы 12В 40Ач				шт	2		
8	Кожух для моноблоков серии SPM настенного исполнения	Sonar SPM-Cover			шт	1		
	ОКЛ RTK							
9	Кабель КПСнз(А)-FRHF 1x2x1.5		RTK-1-3-806		м	180		
10	Кабель ParLan U/UTP Cat5e PVCLСнз(А)-FRHF 4x2x0,52				м	20		
11	Труба гофрированная самозатухающая «ТГ ПВХ» 20 мм с зондом		RTK-2-5-02		м	200		
12	Муфта соединительная для труб 20мм		RTK-4-3-02		шт	10		
13	Коробка монтажная огнестойкая 4к x 2,5 мм		RTK-3-1-04		шт	4		
14	Скоба оцинкованная с одним отверстием, для трубы D20 мм		RTK-4-2-14		шт	600		
15	Гильзы в стенах и перегородках из труб метал.	d-32мм			м	3		
16	Гидроизоляционная огнеупорная мастика	AM-05			кг	3		

						2025-00224-01-0-ИОС 5.2		
Изм.	Кол.уч.	Лист	№док.	Подпись	Дата	Капитальный ремонт здания по адресу: г. Москва, ул.Мясницкая, д.44 стр.1 Спецификация оборудования и материалов		
Разраб.		Короткова К.Н.			03.2026			
Зав.сектор.		Роянцева А.А.			03.2026			
Н.Контроль		Роянцева А.А.			03.2026			
Нач.ОПИС№1		Белусова Д.П.			03.2026			
						Стадия	Лист	Листов
						П	1	1

9710075487-20260216-1017

(регистрационный номер выписки)

16.02.2026

(дата формирования выписки)

ВЫПИСКА

из единого реестра сведений о членах саморегулируемых организаций в области инженерных изысканий и в области архитектурно-строительного проектирования и их обязательствах

Настоящая выписка содержит сведения о юридическом лице (индивидуальном предпринимателе), осуществляющем подготовку проектной документации:

Государственное автономное учреждение города Москвы Московский научно-исследовательский и проектный институт жилищного хозяйства «МосжилНИИпроект»

(полное наименование юридического лица/ФИО индивидуального предпринимателя)

1197746303204

(основной государственный регистрационный номер)

1. Сведения о члене саморегулируемой организации:

1.1	Идентификационный номер налогоплательщика	9710075487
1.2	Полное наименование юридического лица (Фамилия Имя Отчество индивидуального предпринимателя)	Государственное автономное учреждение города Москвы Московский научно-исследовательский и проектный институт жилищного хозяйства «МосжилНИИпроект»
1.3	Сокращенное наименование юридического лица	ГАУ «МосжилНИИпроект»
1.4	Адрес юридического лица Место фактического осуществления деятельности (для индивидуального предпринимателя)	107078, Россия, Москва, г. Москва, Каланчевская, 4/2, 1, -
1.5	Является членом саморегулируемой организации	Ассоциация проектировщиков инженерной инфраструктуры «Инфрадизайн» (СРО-П-218-15012021)
1.6	Регистрационный номер члена саморегулируемой организации	П-218-009710075487-0095
1.7	Дата вступления в силу решения о приеме в члены саморегулируемой организации	18.06.2021
1.8	Дата и номер решения об исключении из членов саморегулируемой организации, основания исключения	

2. Сведения о наличии у члена саморегулируемой организации права осуществлять подготовку проектной документации:

2.1 в отношении объектов капитального строительства (кроме особо опасных, технически сложных и уникальных объектов, объектов использования атомной энергии) (дата возникновения/изменения права)	2.2 в отношении особо опасных, технически сложных и уникальных объектов капитального строительства (кроме объектов использования атомной энергии) (дата возникновения/изменения права)	2.3 в отношении объектов использования атомной энергии (дата возникновения/изменения права)
Да, 18.06.2021	Нет	Нет



3. Компенсационный фонд возмещения вреда

3.1	Уровень ответственности члена саморегулируемой организации по обязательствам по договору подряда на подготовку проектной документации, в соответствии с которым указанным членом внесен взнос в компенсационный фонд возмещения вреда	Третий уровень ответственности (не превышает триста миллионов рублей)
3.2	Сведения о приостановлении / прекращении права осуществлять подготовку проектной документации объектов капитального строительства	

4. Компенсационный фонд обеспечения договорных обязательств

4.1	Дата, с которой член саморегулируемой организации имеет право осуществлять подготовку проектной документации по договорам подряда, заключаемым с использованием конкурентных способов заключения договоров, в соответствии с которым указанным членом внесен взнос в компенсационный фонд обеспечения договорных обязательств	18.06.2021
4.2	Уровень ответственности члена саморегулируемой организации по обязательствам по договорам подряда на подготовку проектной документации, заключаемым с использованием конкурентных способов заключения договоров, в соответствии с которым указанным членом внесен взнос в компенсационный фонд обеспечения договорных обязательств	Четвертый уровень ответственности (составляет триста миллионов рублей и более)
4.3	Дата уплаты дополнительного взноса	Нет
4.4	Сведения о приостановлении / прекращении права осуществлять подготовку проектной документации по договорам подряда, заключаемым с использованием конкурентных способов заключения договоров	

5. Фактический совокупный размер обязательств

5.1	Фактический совокупный размер обязательств по договорам подряда на подготовку проектной документации, заключаемым с использованием конкурентных способов заключения договоров на дату выдачи выписки	399883177 руб.
-----	--	----------------



ДОКУМЕНТ ПОДПИСАН УСИЛЕННОЙ КВАЛИФИЦИРОВАННОЙ
ЭЛЕКТРОННОЙ ПОДПИСЬЮ

Владелец: «НАЦИОНАЛЬНОЕ ОБЪЕДИНЕНИЕ ИЗЫСКАТЕЛЕЙ И
ПРОЕКТИРОВЩИКОВ» «НОПРИЗ»

129090, г. Москва, пр-т Мира, 3, стр.3

СЕРТИФИКАТ 02 A9 64 C2 00 16 B3 DD A0 42 4E 1C 7B 48 A1 7E 77

ДЕЙСТВИТЕЛЕН: с 10.07.2025 по 10.10.2026



9710075487-20260216-1016

(регистрационный номер выписки)

16.02.2026

(дата формирования выписки)

ВЫПИСКА

из единого реестра сведений о членах саморегулируемых организаций в области инженерных изысканий и в области архитектурно-строительного проектирования и их обязательствах

Настоящая выписка содержит сведения о юридическом лице (индивидуальном предпринимателе), выполняющем инженерные изыскания:

Государственное автономное учреждение города Москвы Московский научно-исследовательский и проектный институт жилищного хозяйства "МосжилНИИпроект"

(полное наименование юридического лица/ФИО индивидуального предпринимателя)

1197746303204

(основной государственный регистрационный номер)

1. Сведения о члене саморегулируемой организации:

1.1	Идентификационный номер налогоплательщика	9710075487
1.2	Полное наименование юридического лица (Фамилия Имя Отчество индивидуального предпринимателя)	Государственное автономное учреждение города Москвы Московский научно-исследовательский и проектный институт жилищного хозяйства "МосжилНИИпроект"
1.3	Сокращенное наименование юридического лица	ГАУ "МосжилНИИпроект"
1.4	Адрес юридического лица Место фактического осуществления деятельности (для индивидуального предпринимателя)	107078, Россия, Москва, вн.тер.г. муниципальный округ Красносельский, ул. Каланчевская, д. 4/2, стр. 1
1.5	Является членом саморегулируемой организации	Ассоциация саморегулируемая организация «Центральное объединение организаций по инженерным изысканиям для строительства «Центризыскания» (СРО-И-003-14092009)
1.6	Регистрационный номер члена саморегулируемой организации	И-003-009710075487-0097
1.7	Дата вступления в силу решения о приеме в члены саморегулируемой организации	14.10.2009
1.8	Дата и номер решения об исключении из членов саморегулируемой организации, основания исключения	

2. Сведения о наличии у члена саморегулируемой организации права выполнять инженерные изыскания:

2.1 в отношении объектов капитального строительства (кроме особо опасных, технически сложных и уникальных объектов, объектов использования атомной энергии) (дата возникновения/изменения права)	2.2 в отношении особо опасных, технически сложных и уникальных объектов капитального строительства (кроме объектов использования атомной энергии) (дата возникновения/изменения права)	2.3 в отношении объектов использования атомной энергии (дата возникновения/изменения права)
Да, 14.10.2009	Да, 28.06.2023	Нет



3. Компенсационный фонд возмещения вреда

3.1	Уровень ответственности члена саморегулируемой организации по обязательствам по договору подряда на выполнение инженерных изысканий, в соответствии с которым указанным членом внесен взнос в компенсационный фонд возмещения вреда	Третий уровень ответственности (не превышает триста миллионов рублей)
3.2	Сведения о приостановлении права выполнять инженерные изыскания объектов капитального строительства	

4. Компенсационный фонд обеспечения договорных обязательств

4.1	Дата, с которой член саморегулируемой организации имеет право выполнять инженерные изыскания по договорам подряда, заключаемым с использованием конкурентных способов заключения договоров, в соответствии с которым указанным членом внесен взнос в компенсационный фонд обеспечения договорных обязательств	01.07.2017
4.2	Уровень ответственности члена саморегулируемой организации по обязательствам по договорам подряда на выполнение инженерных изысканий, заключаемым с использованием конкурентных способов заключения договоров, в соответствии с которым указанным членом внесен взнос в компенсационный фонд обеспечения договорных обязательств	Третий уровень ответственности (не превышает триста миллионов рублей)
4.3	Дата уплаты дополнительного взноса	07.03.2019
4.4	Сведения о приостановлении права выполнять инженерные изыскания по договорам подряда, заключаемым с использованием конкурентных способов заключения договоров	

5. Фактический совокупный размер обязательств

5.1	Фактический совокупный размер обязательств по договорам подряда на выполнение инженерных изысканий, заключаемым с использованием конкурентных способов заключения договоров на дату выдачи выписки	7736457.93 руб.
-----	--	-----------------



ДОКУМЕНТ ПОДПИСАН УСИЛЕННОЙ КВАЛИФИЦИРОВАННОЙ
ЭЛЕКТРОННОЙ ПОДПИСЬЮ

Владелец: «НАЦИОНАЛЬНОЕ ОБЪЕДИНЕНИЕ ИЗЫСКАТЕЛЕЙ И
ПРОЕКТИРОВЩИКОВ» «НОПРИЗ»

129090, г. Москва, пр-т Мира, 3, стр.3

СЕРТИФИКАТ 02 A9 64 C2 00 16 B3 DD A0 42 4E 1C 7B 48 A1 7E 77

ДЕЙСТВИТЕЛЕН: с 10.07.2025 по 10.10.2026

