



Департамент капитального ремонта города Москвы Государственное автономное учреждение города Москвы Московский научно-исследовательский и проектный институт жилищного хозяйства «МосжилНИИпроект» (ГАУ «МосжилНИИпроект»)

mgnp@mgnp.mos.ru +7 495 624 40 65 107078, г. Москва, ул. Каланчевская, д. 4/2, стр. 1

Арх. №

**Капитальный ремонт здания, расположенного по
адресу:
г. Москва, улица Мясницкая, дом 44, стр. 1**

ПРОЕКТНАЯ ДОКУМЕНТАЦИЯ

**Раздел 5. Сведения об инженерном оборудовании,
о сетях и системах инженерно-технического обеспечения.**

Подраздел 5. Сети связи

Часть 3. Радиотрансляционная сеть

Том 5.5.3

2025-00224-01-0-ИОС5.3

**Капитальный ремонт здания, расположенного по
адресу:
г. Москва, улица Мясницкая, дом 44, стр. 1**

ПРОЕКТНАЯ ДОКУМЕНТАЦИЯ

**Раздел 5. Сведения об инженерном оборудовании,
о сетях и системах инженерно-технического обеспечения.**

Подраздел 5. Сети связи

Часть 3. Радиотрансляционная сеть

Том 5.5.3

2025-00224-01-0-ИОС5.3

Начальник ОПИС №1

Зам.начальника УКПОЖФ



Д.П. Белоусова

07.04.2026

П.П.Пивторак

07.04.2026

СОДЕРЖАНИЕ РАЗДЕЛА

№п/п	Наименование	стр.
1	Содержание раздела	2
2	Состав проектной документации	3
3	Пояснительная записка	4,5
4	Ситуационный план	6
5	Принципиальная схема системы радиофикации и оповещения ГОЧС	7
6	План 2-го этажа. М1:100. Расположение оконечного оборудования системы РТС.	8
7	План кровли	9
8	Спецификация оборудования, изделий и материалов	10
9		11

Инв. N док	Подпись и дата	Взам. инв. N							2025-00224-01-0-ИОС5.3 Содержание тома		
			Изм.	Кол.уч.	Лист	Ндок.	Подпись	Дата	Стадия	Лист	Листов
			Разработал		Короткова К.Н.			03.2026	П	1	1
			Зав.сектор.		Роянцева А.А.			03.2026			
			Н.Контроль		Роянцева А.А.			03.2026	МОСЖИЛ НИИПРОЕКТ		
			Нач. ОПИС №1		Белюсова Д.П.			03.2026			

Пояснительная записка.

Настоящим комплектом проектной документации предусмотрено оборудование здания по адресу: г. Москва, улица Мясницкая, дом 44, стр. 1 – системами Радиотрансляционной сети и оповещения ГОЧС

Данным проектом выполняются расстановка оконечного оборудования системы радиотрансляционной сети и оповещения о ГОЧС.

Проект разработан на основании архитектурных чертежей стадии проектная документация. Раздел соответствует требованиям действующих нормативных документов:

- СП 2.13130.2012 «Системы противопожарной защиты. Обеспечение огнестойкости объектов защиты»;
- СП 3.13130.2009 «Системы оповещения и управления эвакуацией людей при пожаре»;
- СП 6.13130.2021 «Системы противопожарной защиты. Электрооборудование. Требования пожарной безопасности»;
- СП 134.13330.2022 «Системы электросвязи зданий и сооружений. Основные положения проектирования»;
- ГОСТ 31565-2012 Межгосударственный стандарт «Кабельные изделия. Требования пожарной безопасности»;
- ПУЭ 7 «Правила устройства электроустановок».

Радиофикация

Система разработана в соответствии с ТУ №1995 РФ/О/РСПИ/ТВ-ЕТЦ/2025 "Информтелефонная сеть", ТУ №78848 от 12.12.2025 и ТТ №78846 от 12.12.2025 от ГБУ "Система 112".

Установить в помещении серверной на высоте 1.0 м настенный шкаф с устройством подачи программ проводного вещания "УППВ 1918 М1 исп.У" для организации приема, формирования и подачи сигналов 3-х программно-звукового вещания в домовую распределительную сеть.

В зоне уверенного приема сигналов радиовещания на кровле установить мачту. На мачту установить приемную антенну ЧМ/FM диапазона и коллинеарную антенну 470 МГц. От антенны ЧМ/FM диапазона и коллинеарной антенны до УППВ проложить: коаксиальный кабель типа RG-6 и коаксиальный кабель 50 Ом.

В УППВ, в качестве приемного и каналообразующего устройства, используются блок источников программ БИП-03 с установленным в него модулем для приема интернет вещания радиостанции "Радио Москвы". Эфирные сигналы от антенны и потоковое радио из сети интернет (предусмотрен кабель витая пара кат. 5е) поступают на вход БИП. Далее сигналы радиофикации с выхода блока БИП передаются в блок модулятора-смесителя БМС-03 исп.У шкафа УППВ. Блок БМС-03 исп.У обеспечивает обработку 3-х входных сигналов, их усиление и смешивание для формирования комплексного выходного сигнала. С выхода БМС-03 исп.У транслируется сигнал трехпрограммного проводного вещания 15В/5Вт (рассчитана на 20 абонентов).

Нагрузка сети радиотрансляции принята из расчета обеспечения номинальной мощности на радиорозетку 0,25Вт.

Распределительную сеть выполнить кабелем КАПС 10нг(А)-HF-XЛ 1х2х1,5 исп. РОМ (прокладывается шлейфом безразрывно). Коробки РОН-2 установить в нишах СС на этажах.

Абонентскую сеть выполнить кабелем КПСППнг(А)-HF 1х2х0,5

Радиорозетку предусмотреть в кабинете прокурора. Кабели проложить по потолку и опуски к оконечным точкам в штробах стен – в гофрированных ПВХ трубах.

Взам. инв. N		Подпись и дата	Нагрузка сети радиотрансляции принята из расчета обеспечения номинальной мощности на радиорозетку 0,25Вт. Распределительную сеть выполнить кабелем КАПС 10нг(А)-HF-XЛ 1х2х1,5 исп. РОМ (прокладывается шлейфом безразрывно). Коробки РОН-2 установить в нишах СС на этажах. Абонентскую сеть выполнить кабелем КПСППнг(А)-HF 1х2х0,5 Радиорозетку предусмотреть в кабинете прокурора. Кабели проложить по потолку и опуски к оконечным точкам в штробах стен – в гофрированных ПВХ трубах.									
			2025-00224-01-0-ИОС5.3									
Инв. N док.			Изм.	Кол.уч.	Лист	Ндок.	Подпись	Дата	Пояснительная записка	Стадия	Лист	Листов
			Разработал	Целин С.Р.			04.2025					
			Зав.сектор.	Роянцева А.А.			04.2025					
			Н.Контроль	Роянцева А.А.			04.2025					
			Нач. ОПИС №1	Белюсова Д.П.			04.2025					
											МОСЖИЛ НИИПРОЕКТ	

Оповещение о ЧС

Согласно требованиям ТУ ГБУ "Система 112" о сопряжении объектовой системы оповещения (ОСО) с региональной системой оповещения (РСО) населения г. Москвы о ЧС по 2-м каналам оповещения. Сопряжение ОСО с РСО осуществляется через автоматизированный пульт управления (АПУ) РСО г. Москвы и через комплекс технических средств оповещения (КТСО) РСО г. Москвы.

В помещении №222 Серверной установить устройство сопряжения с РСО г. Москвы "УС-1".

Сигналы управления и речевого оповещения поступают на входы блока БК1-3 исп. К для коммутации и распределения. Далее с выхода-1 блока БК1-3 исп. К сигналы управления и речевого поступают на приоритетный вход БИП-03 для распространения в сети радиофикации.

С выхода 2 блока БК1-3 исп. К сигналы управления и речевого оповещения подаются на соответствующий вход блоков управления СОУЭ (предусмотреть кабель КПСн(А)-FRHF 2х2х0,5 для сопряжения с системой СОУЭ, см. том 2025-00224-01-0-ИОС5.2 СОУЭ).

Радиоканальная система передачи извещений (РСПИ) о пожаре на «пилот 01»

Для организации РСПИ о пожаре на «пульт 01» модуль МВК- RS в объектовой станции ПАК «Стрелец-мониторинг» подключается к релейному входу «Сигнал 01» приемно-контрольного прибора системы АПС «Рубеж» кабелем марки КПСнг(А)-FRHF 2х2х0,5.

В релейном блоке, прибора «Рцбжж» есть реле на выдачу сигналов:

-сигнал «Пожар»;

-сигнал «Неисправность».

Предусмотрен дублирующий сигнал "Пожар" через Стрелец Тандем.

В соответствии с требованиями п.5.2.4 СП 2.13130.2020, места пересечения кабелей, кабеленесущих конструкций со строительными конструкциями с нормируемыми пределами огнестойкости, обеспечиваются проходками не ниже пределов огнестойкости, установленных для пересекаемых конструкций посредством установки гильз из труб с заделкой гидроизоляционной огнеупорной мастикой в соответствии с ГОСТ 30247.1, ГОСТ Р 53306, ГОСТ Р 53310.


Электропитание и заземление

По степени надежности электроснабжения сети связи относятся ко 2-ой категории потребителей. Для оборудования предусмотрены источники бесперебойного питания.


Защита электрических цепей должна быть выполнена в соответствии с ПУЭ.

Защитное заземление электрооборудования, металлических каркасов и конструкций следует выполнить в соответствии с ПУЭ и технической документацией на оборудование.

[illegible]

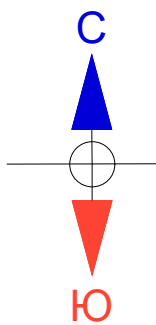

Направление на
ТЦ "Останкино"

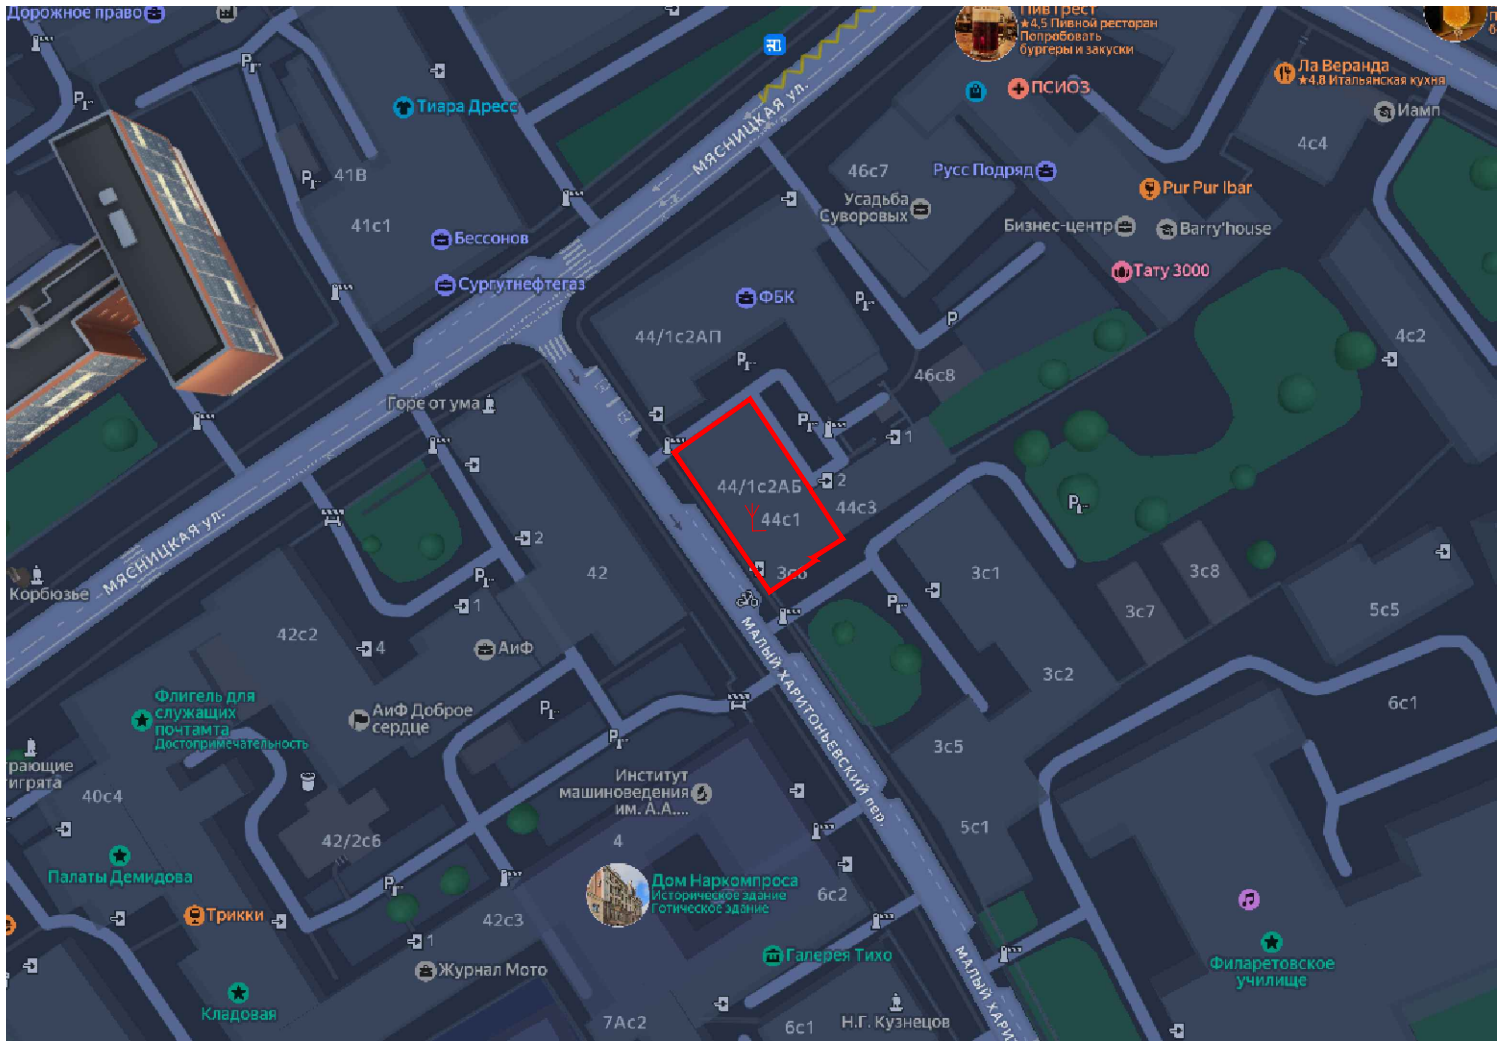

Согласовано

Инв. № подл. Подп. и дата Взам. инв. №

Условные обозначения:
 - Антенна ЧМ/FM и ТВ
 - Площадь капитального ремонта

						2025-00224-01-0-ИОС 5.3			
						Капитальный ремонт г. Москва, ул. Мясницкая д.44 стр.1			
Изм.	Кол.уч.	Лист	№ док.	Подпись	Дата	Капитальный ремонт	Стадия	Лист	Листов
Разработал		Целин С.Р.			03.2026		П	1	4
Зав. сектор		Роянцева А.А.			03.2026				
						Ситуационный план	 МОСЖИЛ НИИПРОЕКТ		
Н. Контроль		Роянцева А.А.			03.2026				
Нач.ОПИС №1		Белюсова Д.П.			03.2026				



Согласовано

Взам. инв. №

Подп. и дата

Инв. № подл.

Стояк СС №1

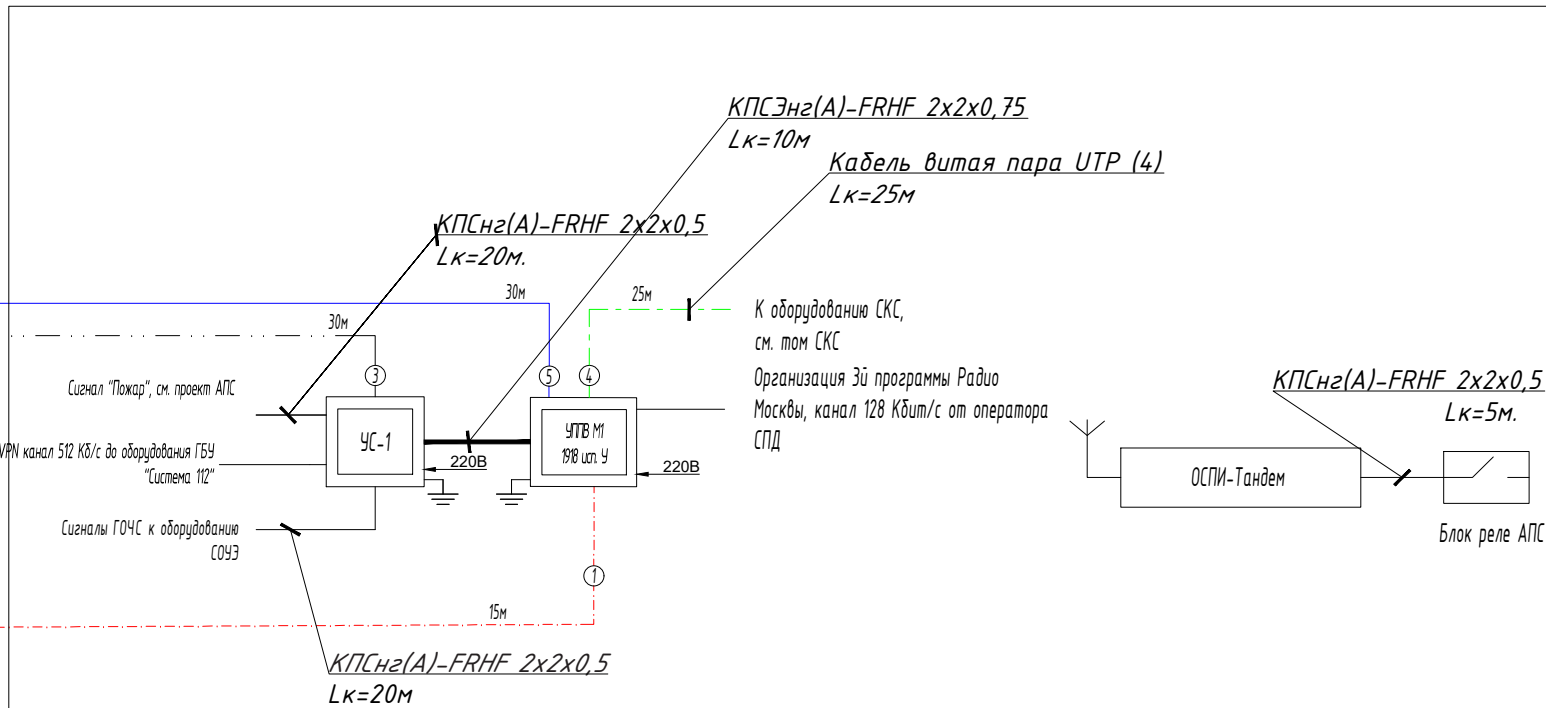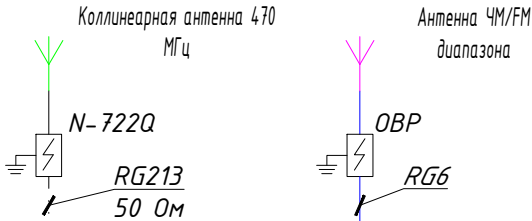

Серверная 222

Условные обозначения:

- Антенна коллинеарная 470 МГц
- Антенна диапазона ЧМ/ФМ
- Ограничительная коробка типа РОН-2
- Радиорозетка
- Кабель распределительный СКАПС 10нз(А)-НФ-ХЛ 1х2х1,5 исп. РОМ (1)
- Кабель абонентский КПСПнз(А)-НФ 1х2х0,5 (2)
- Ограничительная коробка типа КРА-4
- Шкаф устройства подачи программ вещания ЧППВ М1 1918 исп. У
- Устройство сопряжения с РСО г. Москвы "УС-1"
- Грозозащита для коаксиальных кабелей (ОВР и N-722Q)
- Кабель радиочастотный коаксиальный РК50-7-37нз(А)-НФ (3)
- Кабель витая пара КВПнз(А)-НФ -5е 4х2х0,52 (4)
- Радиочастотный коаксиальный кабель РК 75-4,8-33фнз(С)-НФ (5)
- Оборудование резервного канала РСПИ "ОСПИ-ТАНДЕМ"

- Примечание.
1. На кровле здания, установить опору и мачту для антенны ЧМ/ФМ диапазона на плоскую кровлю.
 2. Мачту заземлить к контуру молниезащиты стальным тросом diam. 8,3 мм с наконечниками под опрессовку.
 3. На мачту установить антенну ЧМ/ФМ диапазона, коллинеарную антенну 470 МГц и эфирную антенну СКТ EB45LTE (смотри проект ИОС5.4).
 4. В Серверной (ном. 202) установить на стене по месту телекоммуникационный шкаф ЧППВ и УС-1 на высоте не менее 750 мм от чистового пола.5. Распределительную сеть вести кабелем СКАПС 10нз(А)-НФ-ХЛ 1х2х1,5 исп. РОМ от шкафа ЧППВ до слаботочных ниш. В нишах установить коробки ограничительные РОН-2 и провести кабель на этажах шлейфом без разрыва.
 5. В радиофицируемых помещениях установить радиорозетки, согласно задания на проектирование, не далее 1м от розетки эл. сети 220В.
 6. Абонентскую сеть вести кабелем КПСПнз(А)-НФ 1х2х0,5 от коробки РОН-2 в этажной слаботочном нише до радиорозетки в гофрированной ПВХ трубе.
 7. Сопряжение ГОЧС с РФ от БК1-3 исп.К (в УС-1) до БИП-03 (в ЧППВ) прокладывается кабелем КПСнз(А)-FRHF 2х2х0,5.
 8. Сопряжение ГОЧС с СОУЗ от БК1-3 исп. К (в УС-1) к оборудованию СОУЗ прокладывается кабелем КПСнз(А)-FRHF 2х2х0,5.
 9. Сопряжение АПС с объектовой станцией РСПИ (в УС-1) от блока реле до входа ОС прокладывается КПС3нз(А)-FRHF 2х2х0,75.
 10. Основанием для разработки проекта является ТУ выданными ООО "Корпорация ИнформТелеСеть" и ТУ выданными Департаментом ГБУ система 112.
 11. VPN канал 512 Кб/с оператора до оборудования ГБУ "Система 112"

						2025-00224-01-0-ИОС 5.3			
						Капитальный ремонт г. Москва, ул. Мясницкая д.44 стр.1			
Изм.	Кол.уч.	Лист	№ док.	Подпись	Дата	Капитальный ремонт	Стадия	Лист	Листов
Разработал	Целин С.Р.				03.2026				
Зав. сектор	Роянцева А.А.				03.2026	Принципиальная схема системы радиофикации и оповещения ГОЧС	П	2	4
Н. Контроль	Роянцева А.А.				03.2026				
Нач.ОПИС №1	Белуцова Д.П.				03.2026				

Формат

Architectural floor plan of a building, scale 1:100. The plan shows a grid system with letters А through И and numbers 1 through 7. Dimensions are provided for various sections. Rooms are numbered 201 through 222. A staircase is located in the bottom right corner. A red stamp is visible in room 222.

Экспликация помещений 2-го этажа			
№ п/п	Наименование помещений	Площадь м ²	Кат. пом.
201	Лестница № 1 (ЛК тип 1)	23,1	
202	Лестница № 2 (ЛК тип 1)	22,8	
203	Коридор	34,2	
204	Приемная прокурора	14,5	
205	Кабинет прокурора / видеонаблюдение	25,9	
206	Комната отдыха прокурора	12,3	
207	Сан. узел прокурора	3,5	
208	Кабинет 1-го заместителя прокурора	14,1	
209	Комната отдыха 1-го заместителя прокурора	5,0	
210	Сан. узел 1-го заместителя прокурора	2,6	
211	Кабинет помощника прокурора	15,9	
212	Кабинет помощника прокурора	14,0	
213	Кабинет помощника прокурора	13,7	
214	Архив	10,3	ВЗ
215	Кабинет помощника прокурора	16,4	
216	Кабинет помощника прокурора	17,0	
217	Зал совещаний	16,7	
218	Кабинет помощника прокурора	9,5	
219	Кабинет помощника прокурора	8,9	
220	Комната приrema пищи	9,5	
221	Санузел	2,5	
222	Серверная	7,6	ВЗ
	Итого:	300	

- Радиорозетка
- Кабель распределительный СКАПС 10нз(А)-HF-X/1 1х2х1,5 исп. РОМ (1)
- Кабель абонентский КПСП7нз(А)-HF 1х2х0,5 (2)

Шкаф устройства подачи программ вещания ЦПТВ 1918 М1 исп.

УС-1 - Устройство сопряжения с РСО г. Москвы "УС-1"

						2025-00224-01-0-ИОС.5.3			
						Капитальный ремонт г. Москва, ул. Мясницкая д.44 стр.1			
Изм.	Кол.уч.	Лист	№ док.	Подпись	Дата	Капитальный ремонт	Стадия	Лист	Листов
Разработал	Целин С.Р.				03.2026		П	3	4
Зав. сектор	Роянцева А.А.				03.2026				
						План 2-го этажа.		МОСЖИЛ НИИПРОЕКТ	
Н. Контроль	Роянцева А.А.				03.2026				
Нач.ОПИС №1	Белосузова Д.П.				03.2026				

Согласовано


Инв. № подл.	Подп. и дата	Взам. инв. №
--------------	--------------	--------------

Подп. и дата

Инв. № подл.

Согласовано			
Инв. № подл.	Подп. и дата	Взам. инв. №	


План кровли М 1:100

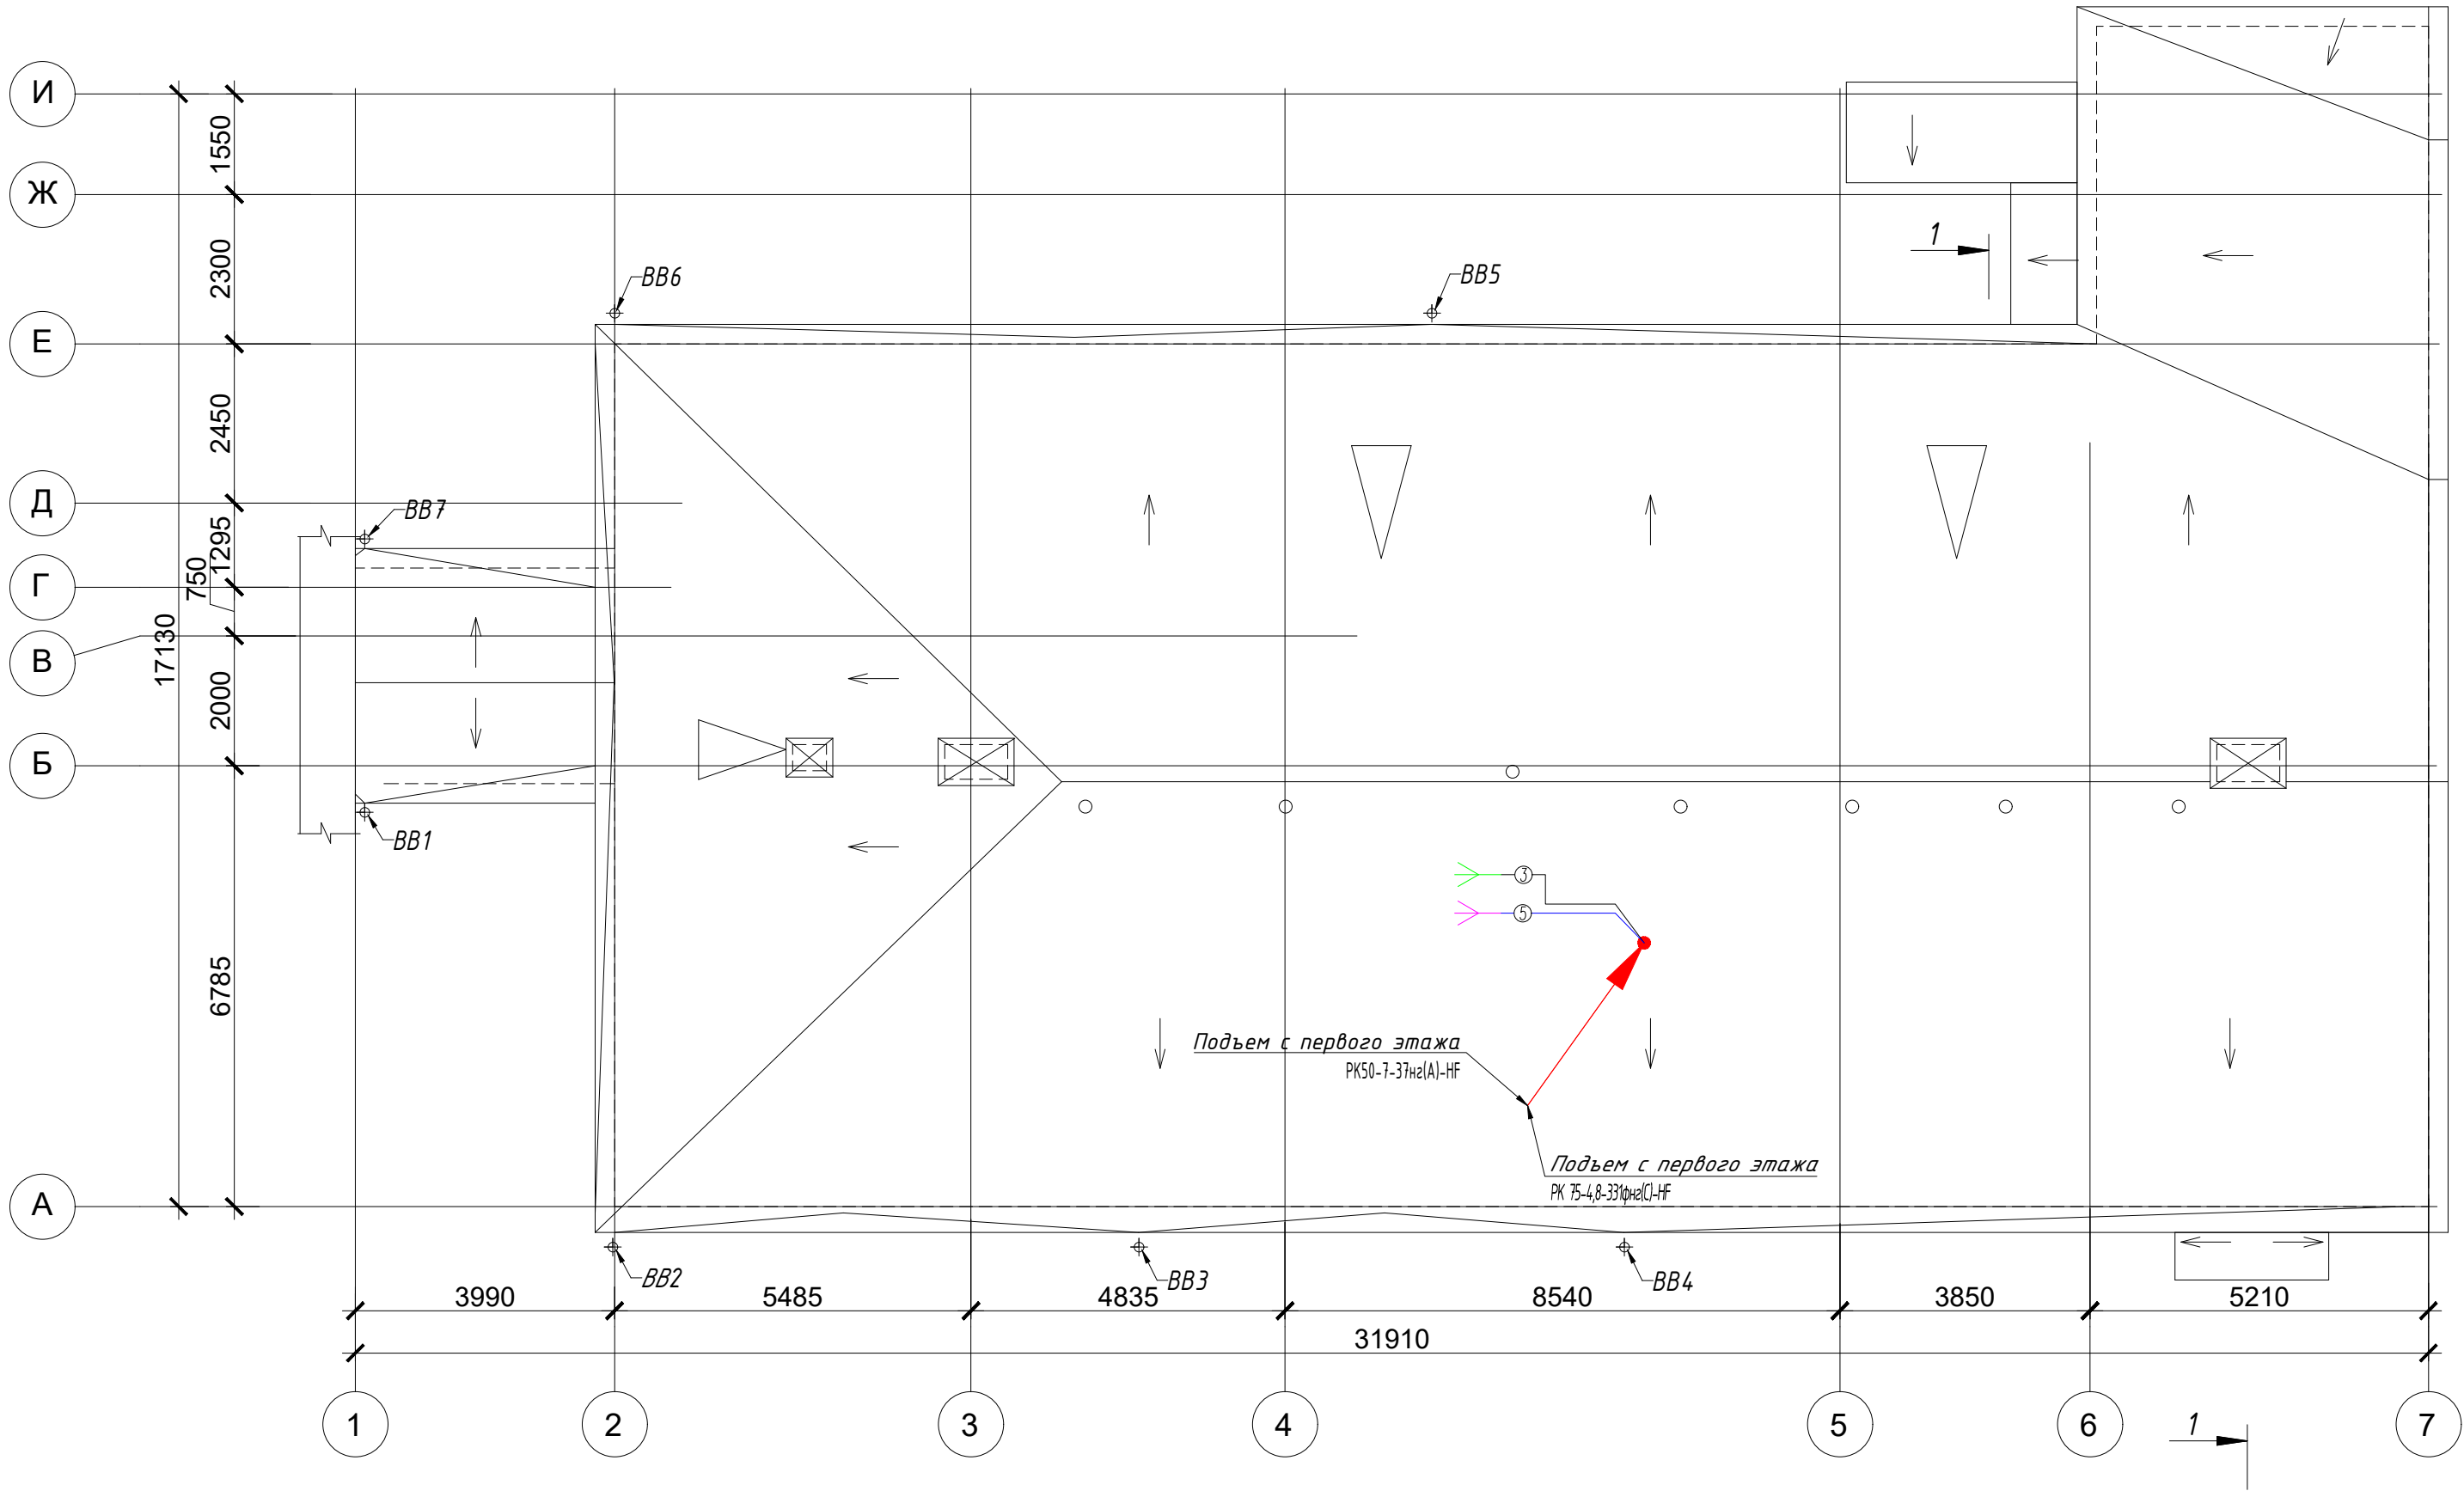


Условные обозначения:

- Антенна коллинеарная 470 МГц
- Антенна диапазона ЧМ/FM
- Кабель радиочастотный коаксиальный РК50-7-37нг(А)-HF (3)
- Радиочастотный коаксиальный кабель РК 75-4,8-33гн(С)-HF (5)

Эскиз крепления мачты на скатную кровлю

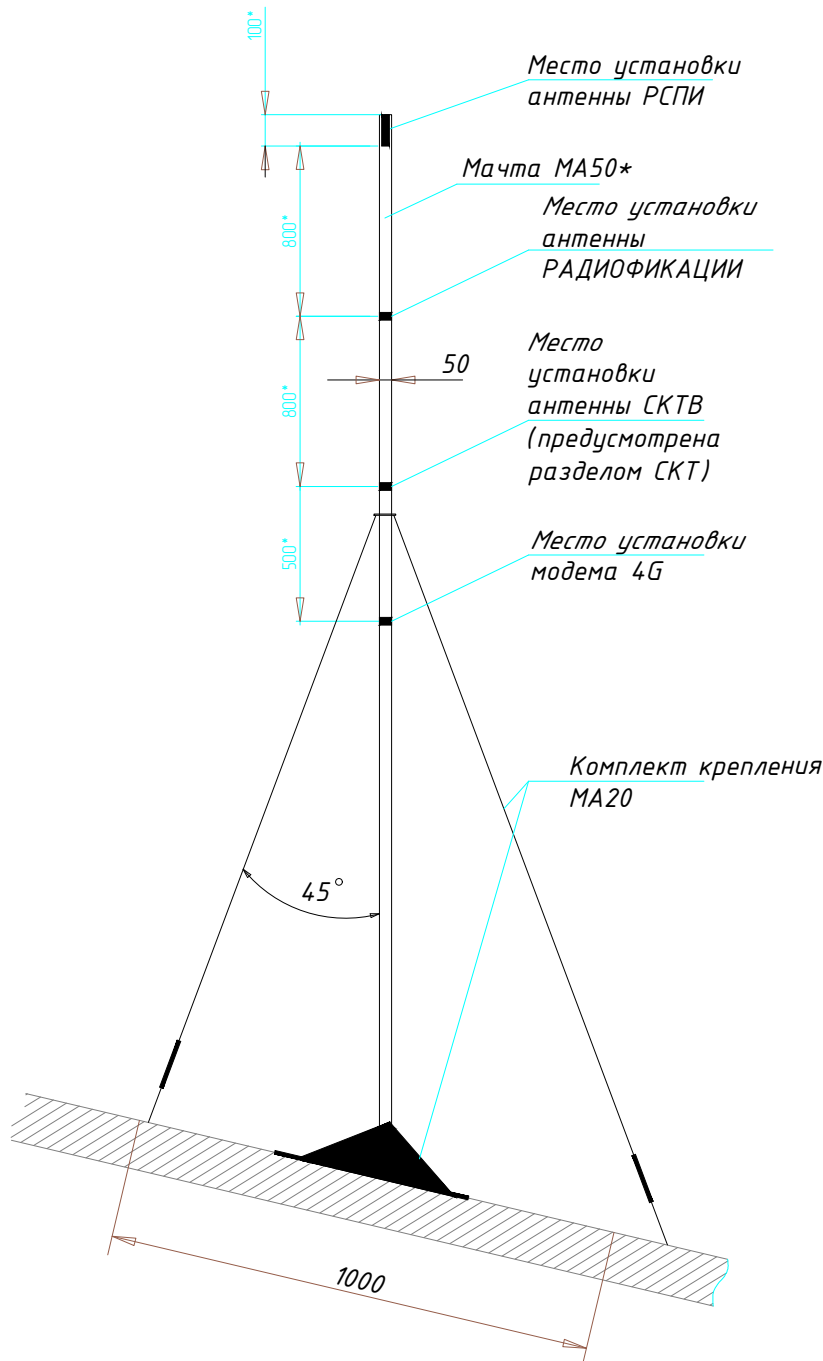

* - высоту мачты установить по месту после установки всех необходимых антенн

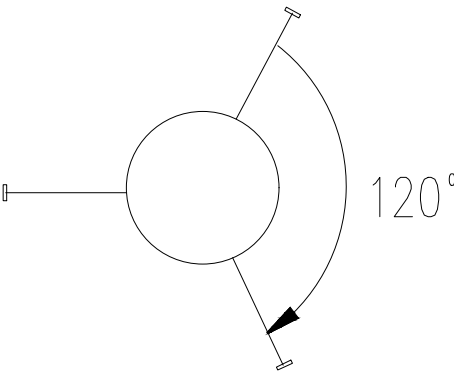

- Примечание.
- Мачта МА50 устанавливается на кровле по месту используя комплект крепления МА20 в зоне уверенного приема каналов радиоразвязки.
 - Мачту заземлить к контуру молниезащиты стальным тросом диам. 8,3 мм.
 - Антенны устанавливаются на мачте МА50.
 - Коаксиальный кабель вести от антенн к УППВ и УС-1.
 - После ввода кабеля в здание отверстие ввода загерметизировать.

						2025-00224-01-0-ИОС5.3				
						Капитальный ремонт г. Москва, ул. Мясницкая д.44 стр.1				
Изм.	Кол.уч.	Лист	№ док.	Подпись	Дата	Капитальный ремонт		Стадия	Лист	Листов
Разработал	Целин С.Р.				03.2026			П	4	4
Зав. сектор	Роянцева А.А.				03.2026					
						План кровли			МОСЖИЛ НИИПРОЕКТ	
Н. Контроль	Роянцева А.А.				03.2026					
Нач.ОПИС №1	Белюсцова Д.П.				03.2026					

Инв. N док. Подпись и дата Взам. инв. N	13											
	Позиция	Наименование и техническая характеристика	Тип, марка, обозначение документа, опросного листа	Код оборудования, изделия, материала	Завод-изготовитель	Единица измерения	Количество	Масса, единицы, кг	Примечание			
	1	2	3	4	5	6	7	8	9			
		Оборудование:										
	1	Устройство подачи программ вещания	УППВ 1918 М1 исп. У (исп. 2022)		ООО"Корпорация ИнформТелеСеть"	компл.	1					
	2	Модуль для приема потокового вещания «Радио Москвы»			ООО"Корпорация ИнформТелеСеть"	шт.	1					
	3	Устройство сопряжения с РСО г. Москвы	УС-1 (БАО-РСПИ+БСМС)		ООО"Корпорация ИнформТелеСеть"	компл.	1					
	4	Объектовая станция "ОСПИ-ТАНДЕМ" (резервный канал РСПИ) в шкафу 600х450х200мм	ОСПИ-Тандем		ООО"Корпорация ИнформТелеСеть"	компл.	1					
	5	Радиоприемник трехпрограммный	Россия ПТ-222		ООО"Корпорация ИнформТелеСеть"	шт.	1					
		Изделия:										
	1	Радиорозетка	АРС-003		ООО ТОР-Электромонтаж	шт.	1					
		Кабельные изделия:										
	1	Кабель распределительный (1)	СКАПС 10нз(А)-HF-ХЛ 1х2х1,5 исп. РОМ		ООО "НПП Спецкабель"	м.	20					
	2	Кабель абонентский (2)	КПСПнз(А)-HF 1х2х0,5		ЗАО "СПКБ Техно"	м.	15					
	3	Кабель витая пара UTP кат. 5е	КВПнз(А)-HF -5е 4х2х0.52		ООО "НПП Спецкабель"	м.	10					
	4	Кабель коаксиальный RG-6	РК 75-4,8-331фнз(С)-HF		ООО "НПП Спецкабель"	м.	30					
	5	Кабель сопряжения с СОУЭ	КПСЭнз(А)-FRHF 2х2х0,75		ООО "НПП Спецкабель"	м.	20					
	6	Кабель коаксиальный для объектовой станции	РК50-7-37нз(А)-HF		ООО "НПП Спецкабель"	м.	30					
	7	Кабель коммутации передачи сигнала на "Пульт 01" ЛОУТОКС	КПСнз(А)-FRHF 2х2х0,5		ООО "НПП Спецкабель"	м.	20					
	8	Кабель сопряжения оборудования СОЧС и ОСО	КПСЭнз(А)-FRHF 2х2х0,75		ООО "НПП Спецкабель"	м.	10					
		Материалы:										
	1											
	2	Коробка ограничительная абонентская на 2 отвода	РОН-2			шт.	1					
	3	Антенна ЧМ/FM диапазона	UE01R		ООО "Сателлит ЛТД"	шт.	1					
	4	Антенна коллинеарная 470 МГц	A-200 MU		ООО "Сателлит ЛТД"	шт.	1					
	5	Мачта	МА50		ООО "Сателлит ЛТД"	шт.	1					
	6	Комплект крепления мачты МА50	МА20		ООО «ПФ АКТ»	компл.	1					
	7	Комплект заземления мачты	КЗМ		ЗАО МТО "Электромонтаж"	компл.	1					
	8	Грозозащита на 75 Ом	ОВР		ООО "Сателлит ЛТД"	шт.	1					
9	Разъем ВЧ на кабель типа RG-6				шт.	10						
10	Коннектор RJ-45	PLUG-8P8C-U-C5		ИТК	шт.	4						
11	Металлорукав в ПВХ изоляции Ø20 мм			Металанг	м.	30						
12	Труба гофрированная из самозатухающего ПВХ-пластиката, Ø 20 мм	91920		ДКС	м.	15						
13	Разъем N-типа на кабель РК50-7-37нз(А)-HF	N-112/8D		RADIOLAB	шт.	3						
14	Разъем TNC-типа на кабель РК50-7-37нз(А)-HF	T-112/8D		RADIOLAB	шт.	1						
15	Грозозащита N-типа на 50 Ом	N-722Q		RADIOLAB	шт.	1						
16	Коробка установочная	10180		ЗАО "Рубинил"	шт.	1						
						2025-00224-01-0-ИОС 5.3.СО						
					Изм.	Кол.уч.	Лист	N док.	Подпись	Дата		
					Разработал	Целин С.Р.				04.2025		
					Зав.сектор.	Роянцева А.А.				04.2025		
					Н.Контроль	Роянцева А.А.				04.2025		
					Нач. ОПИС №1	Белоусова Д.П.				04.2025		
					Спецификация оборудования, изделий и материалов					Статус	Лист	Листов
										П	1	1
												

9710075487-20260114-1539

(регистрационный номер выписки)

14.01.2026

(дата формирования выписки)

ВЫПИСКА

из единого реестра сведений о членах саморегулируемых организаций в области инженерных изысканий и в области архитектурно-строительного проектирования и их обязательствах

Настоящая выписка содержит сведения о юридическом лице (индивидуальном предпринимателе), осуществляющем подготовку проектной документации:

Государственное автономное учреждение города Москвы Московский научно-исследовательский и проектный институт жилищного хозяйства «МосжилНИИпроект»

(полное наименование юридического лица/ФИО индивидуального предпринимателя)

1197746303204

(основной государственный регистрационный номер)

1. Сведения о члене саморегулируемой организации:

1.1	Идентификационный номер налогоплательщика	9710075487
1.2	Полное наименование юридического лица (Фамилия Имя Отчество индивидуального предпринимателя)	Государственное автономное учреждение города Москвы Московский научно-исследовательский и проектный институт жилищного хозяйства «МосжилНИИпроект»
1.3	Сокращенное наименование юридического лица	ГАУ «МосжилНИИпроект»
1.4	Адрес юридического лица Место фактического осуществления деятельности (для индивидуального предпринимателя)	107078, Россия, Москва, г. Москва, Каланчевская, 4/2, 1, -
1.5	Является членом саморегулируемой организации	Ассоциация проектировщиков инженерной инфраструктуры «Инфрадизайн» (СРО-П-218-15012021)
1.6	Регистрационный номер члена саморегулируемой организации	П-218-009710075487-0095
1.7	Дата вступления в силу решения о приеме в члены саморегулируемой организации	18.06.2021
1.8	Дата и номер решения об исключении из членов саморегулируемой организации, основания исключения	

2. Сведения о наличии у члена саморегулируемой организации права осуществлять подготовку проектной документации:

2.1 в отношении объектов капитального строительства (кроме особо опасных, технически сложных и уникальных объектов, объектов использования атомной энергии) (дата возникновения/изменения права)	2.2 в отношении особо опасных, технически сложных и уникальных объектов капитального строительства (кроме объектов использования атомной энергии) (дата возникновения/изменения права)	2.3 в отношении объектов использования атомной энергии (дата возникновения/изменения права)
Да, 18.06.2021	Нет	Нет



3. Компенсационный фонд возмещения вреда

3.1	Уровень ответственности члена саморегулируемой организации по обязательствам по договору подряда на подготовку проектной документации, в соответствии с которым указанным членом внесен взнос в компенсационный фонд возмещения вреда	Третий уровень ответственности (не превышает триста миллионов рублей)
3.2	Сведения о приостановлении / прекращении права осуществлять подготовку проектной документации объектов капитального строительства	

4. Компенсационный фонд обеспечения договорных обязательств

4.1	Дата, с которой член саморегулируемой организации имеет право осуществлять подготовку проектной документации по договорам подряда, заключаемым с использованием конкурентных способов заключения договоров, в соответствии с которым указанным членом внесен взнос в компенсационный фонд обеспечения договорных обязательств	18.06.2021
4.2	Уровень ответственности члена саморегулируемой организации по обязательствам по договорам подряда на подготовку проектной документации, заключаемым с использованием конкурентных способов заключения договоров, в соответствии с которым указанным членом внесен взнос в компенсационный фонд обеспечения договорных обязательств	Четвертый уровень ответственности (составляет триста миллионов рублей и более)
4.3	Дата уплаты дополнительного взноса	Нет
4.4	Сведения о приостановлении / прекращении права осуществлять подготовку проектной документации по договорам подряда, заключаемым с использованием конкурентных способов заключения договоров	

5. Фактический совокупный размер обязательств

5.1	Фактический совокупный размер обязательств по договорам подряда на подготовку проектной документации, заключаемым с использованием конкурентных способов заключения договоров на дату выдачи выписки	399883177 руб.
-----	--	----------------

Руководитель аппарата



ДОКУМЕНТ ПОДПИСАН УСИЛЕННОЙ КВАЛИФИЦИРОВАННОЙ
ЭЛЕКТРОННОЙ ПОДПИСЬЮ

Владелец: «НАЦИОНАЛЬНОЕ ОБЪЕДИНЕНИЕ ИЗЫСКАТЕЛЕЙ И
ПРОЕКТИРОВЩИКОВ» «НОПРИЗ»

129090, г. Москва, пр-т Мира, 3, стр.3

СЕРТИФИКАТ 02 A9 64 C2 00 16 B3 DD A0 42 4E 1C 7B 48 A1 7E 77

ДЕЙСТВИТЕЛЕН: с 10.07.2025 по 10.10.2026

А.О. Кожуховский



9710075487-20260114-1537

(регистрационный номер выписки)

14.01.2026

(дата формирования выписки)

ВЫПИСКА

из единого реестра сведений о членах саморегулируемых организаций в области инженерных изысканий и в области архитектурно-строительного проектирования и их обязательствах

Настоящая выписка содержит сведения о юридическом лице (индивидуальном предпринимателе), выполняющем инженерные изыскания:

Государственное автономное учреждение города Москвы Московский научно-исследовательский и проектный институт жилищного хозяйства "МосжилНИИпроект"

(полное наименование юридического лица/ФИО индивидуального предпринимателя)

1197746303204

(основной государственный регистрационный номер)

1. Сведения о члене саморегулируемой организации:

1.1	Идентификационный номер налогоплательщика	9710075487
1.2	Полное наименование юридического лица (Фамилия Имя Отчество индивидуального предпринимателя)	Государственное автономное учреждение города Москвы Московский научно-исследовательский и проектный институт жилищного хозяйства "МосжилНИИпроект"
1.3	Сокращенное наименование юридического лица	ГАУ "МосжилНИИпроект"
1.4	Адрес юридического лица Место фактического осуществления деятельности (для индивидуального предпринимателя)	107078, Россия, Москва, вн.тер.г. муниципальный округ Красносельский, ул. Каланчевская, д. 4/2, стр. 1
1.5	Является членом саморегулируемой организации	Ассоциация саморегулируемая организация «Центральное объединение организаций по инженерным изысканиям для строительства «Центризыскания» (СРО-И-003-14092009)
1.6	Регистрационный номер члена саморегулируемой организации	И-003-009710075487-0097
1.7	Дата вступления в силу решения о приеме в члены саморегулируемой организации	14.10.2009
1.8	Дата и номер решения об исключении из членов саморегулируемой организации, основания исключения	

2. Сведения о наличии у члена саморегулируемой организации права выполнять инженерные изыскания:

2.1 в отношении объектов капитального строительства (кроме особо опасных, технически сложных и уникальных объектов, объектов использования атомной энергии) (дата возникновения/изменения права)	2.2 в отношении особо опасных, технически сложных и уникальных объектов капитального строительства (кроме объектов использования атомной энергии) (дата возникновения/изменения права)	2.3 в отношении объектов использования атомной энергии (дата возникновения/изменения права)
Да, 14.10.2009	Да, 28.06.2023	Нет

