



Департамент капитального ремонта города Москвы Государственное автономное учреждение города Москвы Московский научно-исследовательский и проектный институт жилищного хозяйства «МосжилНИИпроект» (ГАУ «МосжилНИИпроект»)

mgnp@mgnp.mos.ru +7 495 624 40 65 107078, г. Москва, Каланчевская, д. 4/2, стр. 1

Капитальный ремонт здания, расположенного по
адресу:
г. Москва, улица Мясницкая, дом 44, стр. 1

ПРОЕКТНАЯ ДОКУМЕНТАЦИЯ

**Раздел 5. Сведения об инженерном оборудовании,
о сетях и системах инженерно-технического обеспечения.**

Подраздел 5. Сети связи

Часть 4. Система кабельного телевидения

Том 5.5.4

2025-00224-01-0-ИОС5.4



Департамент капитального ремонта города Москвы Государственное автономное учреждение города Москвы Московский научно-исследовательский и проектный институт жилищного хозяйства «МосжилНИИпроект» (ГАУ «МосжилНИИпроект»)

mgnp@mgnp.mos.ru +7 495 624 40 65 107078, г. Москва, Каланчевская, д. 4/2, стр. 1

Капитальный ремонт здания, расположенного по
адресу:
г. Москва, улица Мясницкая, дом 44, стр. 1

ПРОЕКТНАЯ ДОКУМЕНТАЦИЯ

Раздел 5. Сведения об инженерном оборудовании,
о сетях и системах инженерно-технического обеспечения.

Подраздел 5. Сети связи

Часть 4. Система кабельного телевидения

Том 5.5.4

2025-00224-01-0-ИОС5.4

Начальник ОПИС №1

Зам.начальника УКПОЖФ



Д.П. Белоусова

07.04.2026

П.П.Пивторак

07.04.2026

Москва 2026г.

СОДЕРЖАНИЕ РАЗДЕЛА

№п/п	Наименование	стр.
1	Содержание раздела	2
2	Состав проектной документации	3
3	Пояснительная записка	4,5
4	Ситуационный план	6
5	Принципиальная схема системы СКТ	7
6	План 2-го этажа. М1:100. Расположение оконечного оборудования системы СКТ.	8
7	План кровли. М1:100. Расположение оконечного оборудования системы СКТ.	9
8	Спецификация оборудования, изделий и материалов	10



Инв. N док.	Подпись и дата	Взам. инв. N									
			2025-00224-01-0-ИОС5.4								
			Изм.	Кол.уч.	Лист	Ндок.	Подпись	Дата			
			Разработал	Короткова К.Н.				03.2026			
			Зав.сектор.	Роянцева А.А.				03.2026			
			Н.Контроль	Роянцева А.А.				03.2026			
			Нач. ОПИС №1	Белюсова Д.П.				03.2026			
Содержание тома									Стадия	Лист	Листов
									П	1	1
									 МОСЖИЛ НИИПРОЕКТ		

Состав проектной документации

Смотри том 1.1, 2025-00224-01-0-СП, Часть1. Раздел1. Состав проектной документации.


Согласовано							2025-00224-01-0-ИОС5.4	Капитальный ремонт здания и помещений по адресу г. Москва, ул. Мясницкая, д.44, стр.1	Стадия	Лист	Листов	
									П	1	1	
	Инв. № подл.	Изм.	Кол.уч	Лист	№ док.	Подп.			Дата			
Инв. № подл.	Разработал		Роянцева А.А		<i>Роянцева</i>	03.2026						
	Зав.сектора		Роянцева А.А		<i>Роянцева</i>	03.2026						
	Н.контр.		Роянцева А.А		<i>Роянцева</i>	03.2026						
	Нач.ОПИСН№1		Белоусова Д.П.		<i>Белоусова</i>	03.2026						

**МОСЖИЛ
НИИПРОЕКТ**

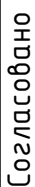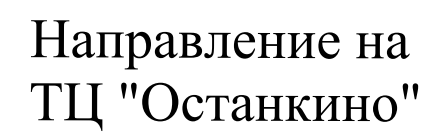

- Антенна ЧМ/FM и ТВ
- Площадь капитального ремонта


Формат

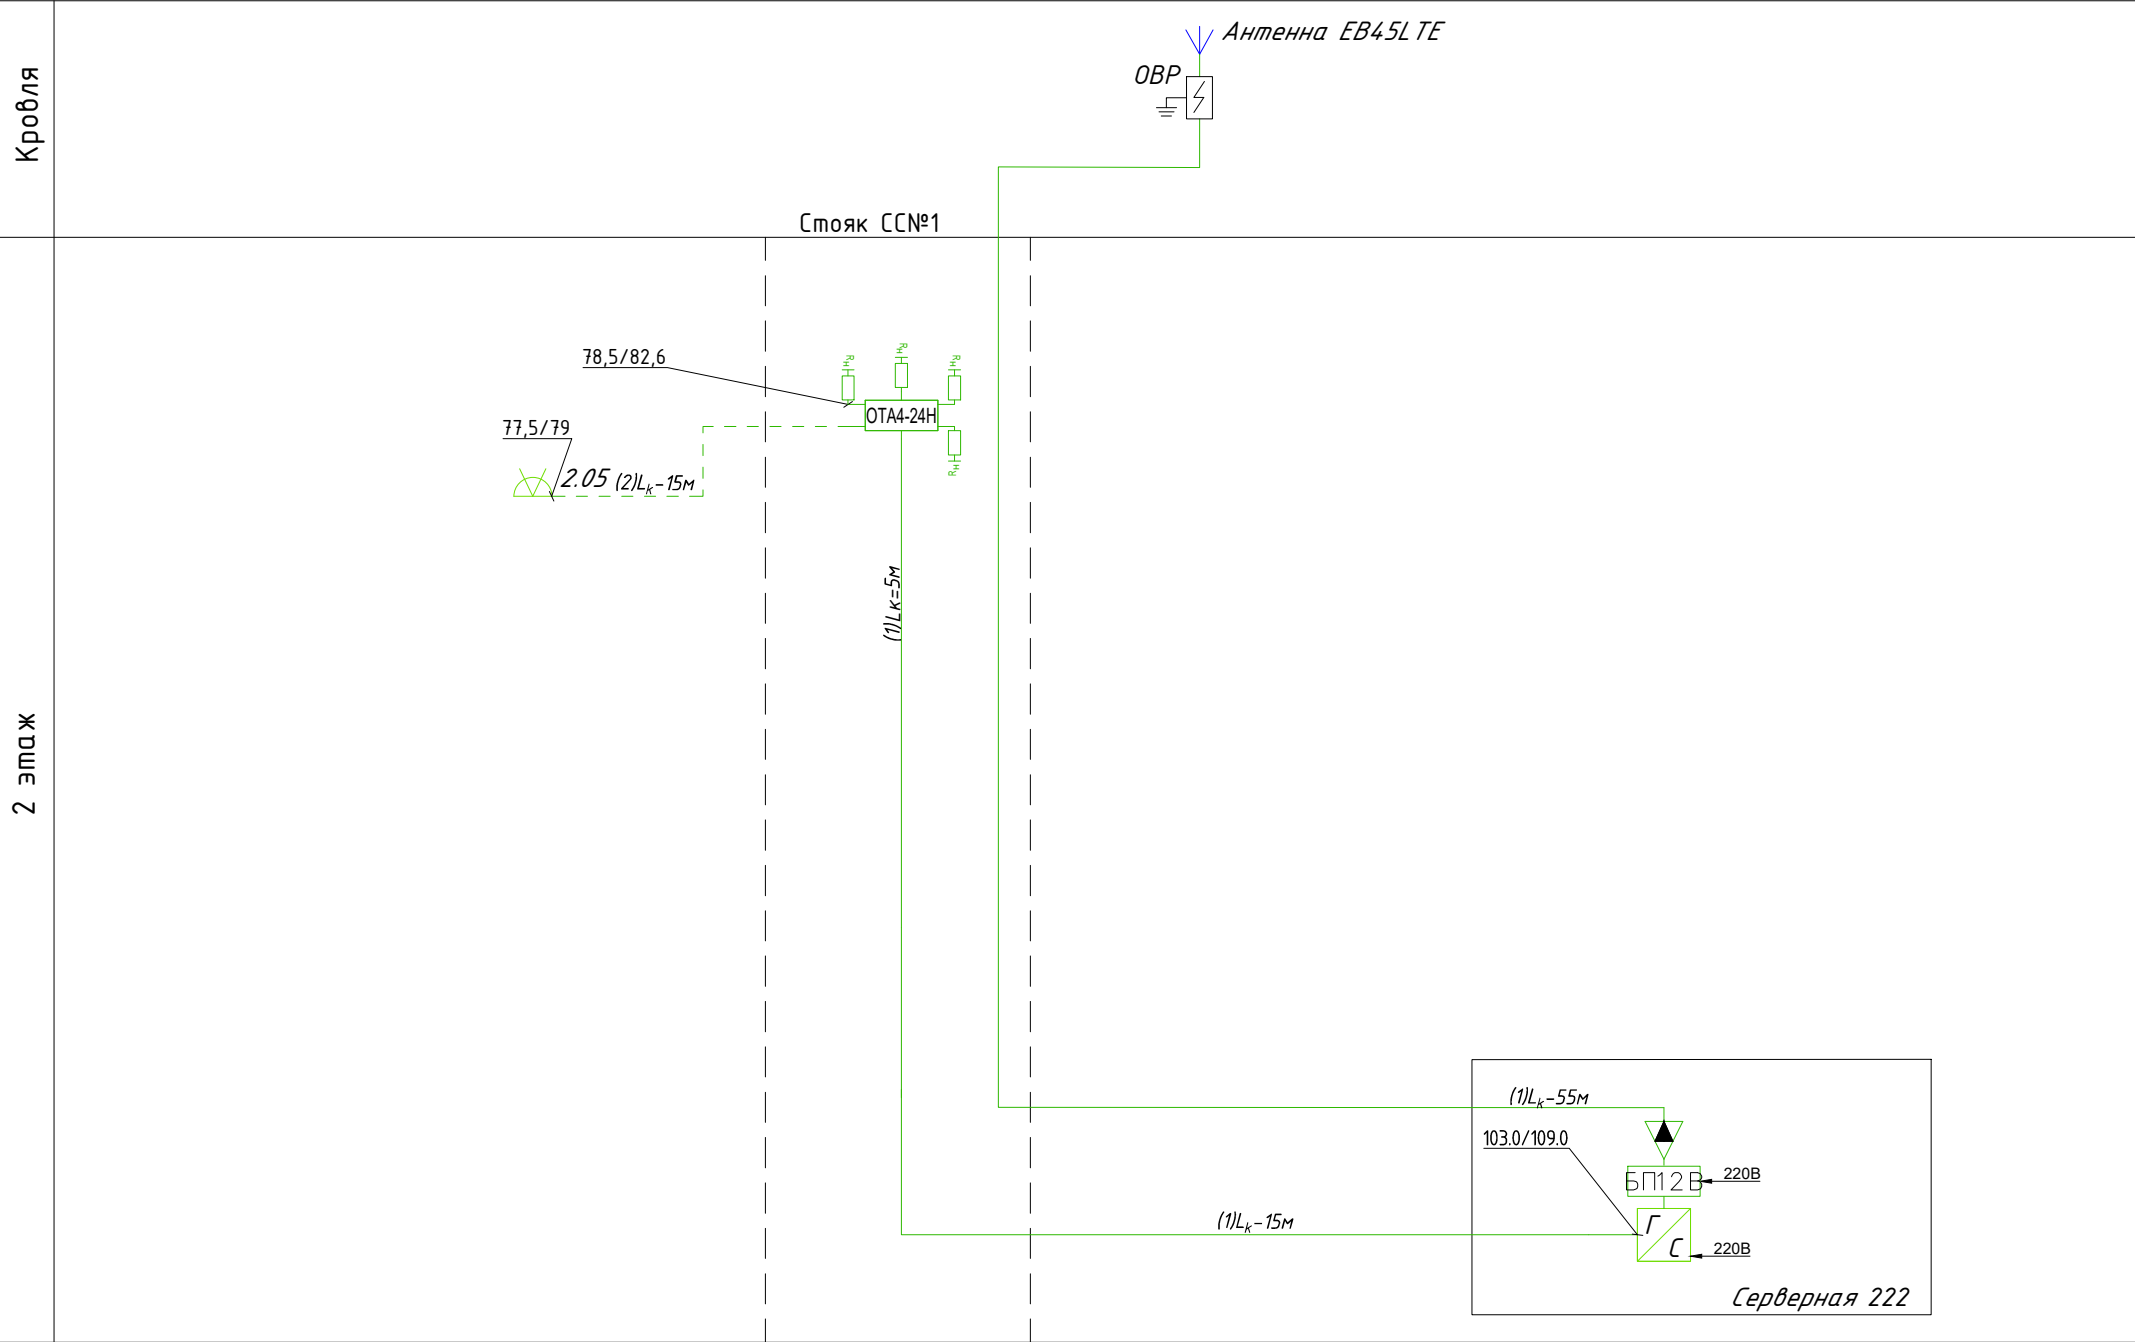


Примечание.

1. На кровле установить на существующей мачте (установка учтена разделом ИОС5.3) установить антенну ДМВ диапазона EV45LTE.
2. В пом. серверной (первый этаж пом. 202) установить на стене шкаф Мини-ГС (600x450x200мм). Корпус шкафа заземлить.
3. Антенный усилитель АВ011 установить при недостаточном уровне сигнала на входе Мини ГС менее 60 дБ.
4. Домовая распределительная сеть выполняется кабелем марки РК 75-7-327нз(А)-HF.
5. Абонентская распределительная сеть выполняется кабелем марки РК 75-3,7-319 нз(А)-HF.
6. Участки, где длина кабеля не указана, выполнить кабелем РК 75-7-327нз(А)-HF из расчета 0,2-0,5 м.
7. В слаботоочных шкафах каждого этажа установить абонентские ответвители типа ОТА серии "Н" на 2, 3, 4, 6 отводов.
8. Оконечные ТВ розетки устанавливаются в помещениях согласно задания.
9. Расчет СКТ произведен из условий обеспечения уровней сигнала на отводах абонентских ответвителей в пределах 72-84 дБ/мкВ и на абонентских ТВ розетках в пределах 60-80 дБ/мкВ на 10. Обеспечить технологический запас не менее 3 дБ в диапазоне частот 47-862 МГц на отводе абонентского ответвителя.
11. Перед нарезкой кабелей, их длины уточняются промером трасс прокладки групп на месте монтажа.
12. Основанием для разработки проекта является ТУ выданными ООО "Корпорация ИнформТелеСеть".

Условные обозначения:

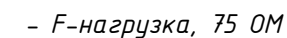


- Телевизионная розетка

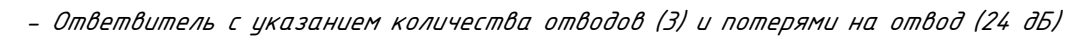

- Кабель коаксиальный РК 75-7-327нз(А)-HF (1), 50/862 МГц - 2,97/12,56 дБ на 100 м

- Кабель коаксиальный РК 75-3,7-319 нз(А)-HF (2), 50/862 МГц - 3,94/17,23 дБ на 100 м

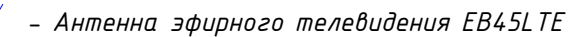

						2025-00224-01-1-ИОС 5.4			
						Здания и помещения по адресу: г. Москва ул. Мясницкая, д.44, стр.1			
Изм.	Кол.уч.	Лист	№ док.	Подпись	Дата	Капитальный ремонт	Стадия	Лист	Листов
Разработал	Роянцева А.А				26.01.26		П	2	4
Зав.сектора	Роянцева А.А				26.01.26				
						Принципиальная схема СКТ	 МОСЖИЛ НИИПРОЕКТ		
Норм.Контр.	Роянцева А.А.				26.01.26				
Нач.ОПИС №1	Белоусова Д.П.				26.01.26				

Экспликация помещений 2-го этажа			
№ п/п	Наименование помещений	Площадь м ²	Кат. пом.
201	Лестница № 1 (ЛК тип 1)	23,1	
202	Лестница № 2 (ЛК тип 1)	22,8	
203	Коридор	34,2	
204	Приемная прокурора	14,5	
205	Кабинет прокурора / видеонаблюдение	25,9	
206	Комната отдыха прокурора	12,3	
207	Сан. узел прокурора	3,5	
208	Кабинет 1-го заместителя прокурора	14,1	
209	Комната отдыха 1-го заместителя прокурора	5,0	
210	Сан. узел 1-го заместителя прокурора	2,6	
211	Кабинет помощника прокурора	15,9	
212	Кабинет помощника прокурора	14,0	
213	Кабинет помощника прокурора	13,7	
214	Архив	10,3	ВЗ
215	Кабинет помощника прокурора	16,4	
216	Кабинет помощника прокурора	17,0	
217	Зал совещаний	16,7	
218	Кабинет помощника прокурора	9,5	
219	Кабинет помощника прокурора	8,9	
220	Комната приrema пищи	9,5	
221	Санузел	2,5	
222	Серверная	7,6	ВЗ
	Итого:	300	

-  - Телевизионная розетка
-  - Кабель коаксиальный РК 75-7-327нз(А)-HF (1), 50/862 МГц - 2,97/12,56 дБ на 100 м
-  - Кабель коаксиальный РК 75-3,7-319 нз(А)-HF (2), 50/862 МГц - 3,94/17,23 дБ на 100 м

						2025-00224-01-1-ИОС 5.4			
						Здания и помещения по адресу: г. Москва ул. Мясницкая, д.44, стр.1			
Изм.	Кол.уч.	Лист	№ док.	Подпись	Дата	Капитальный ремонт	Стадия	Лист	Листов
Разработал	Роянцева А.А				26.01.26		П	3	4
Зав.сектора	Роянцева А.А				26.01.26				
						План 2-го этажа.		МОСЖИЛ НИИПРОЕКТ	
Норм.Контр.	Роянцева А.А.				26.01.26				
Нач.ОПИС №1	Белюсова Д.П.				26.01.26				

Согласовано

Взам. инв. №

Подн. у дана

Инв. № подл.

Architectural floor plan of the first floor of a building. The plan is overlaid with a grid system (A-I, 1-7). Dimensions are provided for various sections: 3990, 5485, 4835, 31910, 8540, 3850, 5210, 6785, 2000, 1295, 750, 2450, 2300, 1550. The plan includes labels for equipment: BB1, BB2, BB3, BB4, BB5, BB6, BB7. A red arrow points to a location labeled "Подъем с первого этажа RG11 (антенный)". The plan also shows various rooms, including a kitchen (Кухня), a dining area (Зона столовой), a living area (Зона гостиной), a bedroom (Спальня), a bathroom (Ванная), a toilet (Туалет), a hallway (Коридор), and a staircase (Лестница). The plan is oriented with North (Север) at the top.

Место установки антенны РСПИ

Мачта МА50*

Место установки антенны РАДИОФИКАЦИИ

50

Место установки антенны СКТВ (предусмотрена разделом СКТ)

Место установки модема 4G

Комплект крепления МА20

45°

1000

A diagram of a circle with three radii drawn from the center to the circumference. The radii are positioned at the 9 o'clock, 1 o'clock, and 5 o'clock positions. An arc between the 1 o'clock and 5 o'clock radii is labeled 120° .

EB45LTE  - Антенна эфирного телевидения
 - RG11 кабель

Формат ФОРМАТ

Инв. N док

Подпись и дата

Взам. инв. N

Позиция	Наименование и техническая характеристика	Тип, марка, обозначение документа, опросного листа	Код оборудования, изделия, материала	Завод-изготовитель	Единица измерения	Количество	Масса, единицы, кг	Примечание
1	2	3	4	5	6	7	8	9
	Оборудование:							
1	Головная станция СКТ "Мини-ГС" на базе оборудования VS50Pro в шкафу 600х450х200мм (частотный план согласно ТУ)	СКТ "Мини ГС"		ООО "Корпорация ИнформТелеСеть"	комп.	1		
2	Антенный усилитель с БП 12В, Ku= 14/27	AB011		Terra	шт.	1		
3	Ответвитель на 4 отвода	ОТА4-24Н		ООО "Сателлит ЛТД"	шт.	1		
	Изделия:							
1	F-разъем для RG-11	DV54		ООО "Сателлит ЛТД"	шт.	20		
2	F -разъём на кабель (RG6) обжимной	FF7		ООО "Сателлит ЛТД"	шт.	15		
3	ТВ розетка, оконечная 1Дб			Россия	шт.	2		
4	F-нагрузка, 75 Ом	FF20		ООО "Сателлит ЛТД"	шт.	29		
	Кабельные изделия:							
1	Кабель коаксиальный RG-11	PK 75-7-327Hz(A)-HF	109528	ООО "Паритет"	м.	20		
2	Кабель коаксиальный RG-6	PK 75-3,7-319 Hz(A)-HF	101316	ООО "Паритет"	м.	28		
	Материалы:							
1	Антенна СКТВ	EB45LTE		ООО "Сателлит ЛТД"	шт.	1		
2	Грозозащита на 75 Ом	OBP		ООО "Сателлит ЛТД"	шт.	1		
3	Металлорукав в ПВХ изоляции Ø20 мм			Металанг	м.	10		
4	Труба гофрированная из самозатухающего ПВХ-пластиката, Ø 20 мм	91920		ДКС	м.	30		
5	Коробка установочная	10180		ЗАО "Рувинил"	шт.	1		

Изм.

Кол.уч.

Лист

N док

Подпись

Дата

Разработал

Целин С.Р.

04.2025

Зав.сектор.

Роянцева А.А.

04.2025

Н.Контроль

Роянцева А.А.

04.2025

Нач. ОПИС №1

Белоусова Д.П.

04.2025

2025-00224-01-0-ИОС 5.4.СО

Спецификация оборудования, изделий и материалов

Стадия

Лист

Листов

П

1

1

МОСЖИЛ
НИИПРОЕКТ

9710075487-20260114-1539

(регистрационный номер выписки)

14.01.2026

(дата формирования выписки)

ВЫПИСКА

из единого реестра сведений о членах саморегулируемых организаций в области инженерных изысканий и в области архитектурно-строительного проектирования и их обязательствах

Настоящая выписка содержит сведения о юридическом лице (индивидуальном предпринимателе), осуществляющем подготовку проектной документации:

Государственное автономное учреждение города Москвы Московский научно-исследовательский и проектный институт жилищного хозяйства «МосжилНИИпроект»

(полное наименование юридического лица/ФИО индивидуального предпринимателя)

1197746303204

(основной государственный регистрационный номер)

1. Сведения о члене саморегулируемой организации:

1.1	Идентификационный номер налогоплательщика	9710075487
1.2	Полное наименование юридического лица (Фамилия Имя Отчество индивидуального предпринимателя)	Государственное автономное учреждение города Москвы Московский научно-исследовательский и проектный институт жилищного хозяйства «МосжилНИИпроект»
1.3	Сокращенное наименование юридического лица	ГАУ «МосжилНИИпроект»
1.4	Адрес юридического лица Место фактического осуществления деятельности (для индивидуального предпринимателя)	107078, Россия, Москва, г. Москва, Каланчевская, 4/2, 1, -
1.5	Является членом саморегулируемой организации	Ассоциация проектировщиков инженерной инфраструктуры «Инфрадизайн» (СРО-П-218-15012021)
1.6	Регистрационный номер члена саморегулируемой организации	П-218-009710075487-0095
1.7	Дата вступления в силу решения о приеме в члены саморегулируемой организации	18.06.2021
1.8	Дата и номер решения об исключении из членов саморегулируемой организации, основания исключения	

2. Сведения о наличии у члена саморегулируемой организации права осуществлять подготовку проектной документации:

2.1 в отношении объектов капитального строительства (кроме особо опасных, технически сложных и уникальных объектов, объектов использования атомной энергии) (дата возникновения/изменения права)	2.2 в отношении особо опасных, технически сложных и уникальных объектов капитального строительства (кроме объектов использования атомной энергии) (дата возникновения/изменения права)	2.3 в отношении объектов использования атомной энергии (дата возникновения/изменения права)
Да, 18.06.2021	Нет	Нет



3. Компенсационный фонд возмещения вреда

3.1	Уровень ответственности члена саморегулируемой организации по обязательствам по договору подряда на подготовку проектной документации, в соответствии с которым указанным членом внесен взнос в компенсационный фонд возмещения вреда	Третий уровень ответственности (не превышает триста миллионов рублей)
3.2	Сведения о приостановлении / прекращении права осуществлять подготовку проектной документации объектов капитального строительства	

4. Компенсационный фонд обеспечения договорных обязательств

4.1	Дата, с которой член саморегулируемой организации имеет право осуществлять подготовку проектной документации по договорам подряда, заключаемым с использованием конкурентных способов заключения договоров, в соответствии с которым указанным членом внесен взнос в компенсационный фонд обеспечения договорных обязательств	18.06.2021
4.2	Уровень ответственности члена саморегулируемой организации по обязательствам по договорам подряда на подготовку проектной документации, заключаемым с использованием конкурентных способов заключения договоров, в соответствии с которым указанным членом внесен взнос в компенсационный фонд обеспечения договорных обязательств	Четвертый уровень ответственности (составляет триста миллионов рублей и более)
4.3	Дата уплаты дополнительного взноса	Нет
4.4	Сведения о приостановлении / прекращении права осуществлять подготовку проектной документации по договорам подряда, заключаемым с использованием конкурентных способов заключения договоров	

5. Фактический совокупный размер обязательств

5.1	Фактический совокупный размер обязательств по договорам подряда на подготовку проектной документации, заключаемым с использованием конкурентных способов заключения договоров на дату выдачи выписки	399883177 руб.
-----	--	----------------

Руководитель аппарата



ДОКУМЕНТ ПОДПИСАН УСИЛЕННОЙ КВАЛИФИЦИРОВАННОЙ
ЭЛЕКТРОННОЙ ПОДПИСЬЮ

Владелец: «НАЦИОНАЛЬНОЕ ОБЪЕДИНЕНИЕ ИЗЫСКАТЕЛЕЙ И
ПРОЕКТИРОВЩИКОВ» «НОПРИЗ»

129090, г. Москва, пр-т Мира, 3, стр.3

СЕРТИФИКАТ 02 A9 64 C2 00 16 B3 DD A0 42 4E 1C 7B 48 A1 7E 77

ДЕЙСТВИТЕЛЕН: с 10.07.2025 по 10.10.2026

А.О. Кожуховский



9710075487-20260114-1537

(регистрационный номер выписки)

14.01.2026

(дата формирования выписки)

ВЫПИСКА

из единого реестра сведений о членах саморегулируемых организаций в области инженерных изысканий и в области архитектурно-строительного проектирования и их обязательствах

Настоящая выписка содержит сведения о юридическом лице (индивидуальном предпринимателе), выполняющем инженерные изыскания:

Государственное автономное учреждение города Москвы Московский научно-исследовательский и проектный институт жилищного хозяйства "МосжилНИИпроект"

(полное наименование юридического лица/ФИО индивидуального предпринимателя)

1197746303204

(основной государственный регистрационный номер)

1. Сведения о члене саморегулируемой организации:

1.1	Идентификационный номер налогоплательщика	9710075487
1.2	Полное наименование юридического лица (Фамилия Имя Отчество индивидуального предпринимателя)	Государственное автономное учреждение города Москвы Московский научно-исследовательский и проектный институт жилищного хозяйства "МосжилНИИпроект"
1.3	Сокращенное наименование юридического лица	ГАУ "МосжилНИИпроект"
1.4	Адрес юридического лица Место фактического осуществления деятельности (для индивидуального предпринимателя)	107078, Россия, Москва, вн.тер.г. муниципальный округ Красносельский, ул. Каланчевская, д. 4/2, стр. 1
1.5	Является членом саморегулируемой организации	Ассоциация саморегулируемая организация «Центральное объединение организаций по инженерным изысканиям для строительства «Центризыскания» (СРО-И-003-14092009)
1.6	Регистрационный номер члена саморегулируемой организации	И-003-009710075487-0097
1.7	Дата вступления в силу решения о приеме в члены саморегулируемой организации	14.10.2009
1.8	Дата и номер решения об исключении из членов саморегулируемой организации, основания исключения	

2. Сведения о наличии у члена саморегулируемой организации права выполнять инженерные изыскания:

2.1 в отношении объектов капитального строительства (кроме особо опасных, технически сложных и уникальных объектов, объектов использования атомной энергии) (дата возникновения/изменения права)	2.2 в отношении особо опасных, технически сложных и уникальных объектов капитального строительства (кроме объектов использования атомной энергии) (дата возникновения/изменения права)	2.3 в отношении объектов использования атомной энергии (дата возникновения/изменения права)
Да, 14.10.2009	Да, 28.06.2023	Нет



3. Компенсационный фонд возмещения вреда

3.1	Уровень ответственности члена саморегулируемой организации по обязательствам по договору подряда на выполнение инженерных изысканий, в соответствии с которым указанным членом внесен взнос в компенсационный фонд возмещения вреда	Третий уровень ответственности (не превышает триста миллионов рублей)
3.2	Сведения о приостановлении права выполнять инженерные изыскания объектов капитального строительства	

4. Компенсационный фонд обеспечения договорных обязательств

4.1	Дата, с которой член саморегулируемой организации имеет право выполнять инженерные изыскания по договорам подряда, заключаемым с использованием конкурентных способов заключения договоров, в соответствии с которым указанным членом внесен взнос в компенсационный фонд обеспечения договорных обязательств	01.07.2017
4.2	Уровень ответственности члена саморегулируемой организации по обязательствам по договорам подряда на выполнение инженерных изысканий, заключаемым с использованием конкурентных способов заключения договоров, в соответствии с которым указанным членом внесен взнос в компенсационный фонд обеспечения договорных обязательств	Третий уровень ответственности (не превышает триста миллионов рублей)
4.3	Дата уплаты дополнительного взноса	07.03.2019
4.4	Сведения о приостановлении права выполнять инженерные изыскания по договорам подряда, заключаемым с использованием конкурентных способов заключения договоров	

5. Фактический совокупный размер обязательств

5.1	Фактический совокупный размер обязательств по договорам подряда на выполнение инженерных изысканий, заключаемым с использованием конкурентных способов заключения договоров на дату выдачи выписки	7736457.93 руб.
-----	--	-----------------

Руководитель аппарата



ДОКУМЕНТ ПОДПИСАН УСИЛЕННОЙ КВАЛИФИЦИРОВАННОЙ
ЭЛЕКТРОННОЙ ПОДПИСЬЮ

Владелец: «НАЦИОНАЛЬНОЕ ОБЪЕДИНЕНИЕ ИЗЫСКАТЕЛЕЙ И
ПРОЕКТИРОВЩИКОВ» «НОПРИЗ»

129090, г. Москва, пр-т Мира, 3, стр.3

СЕРТИФИКАТ 02 A9 64 C2 00 16 B3 DD A0 42 4E 1C 7B 48 A1 7E 77

ДЕЙСТВИТЕЛЕН: с 10.07.2025 по 10.10.2026

А.О. Кожуховский

