



Департамент капитального ремонта города Москвы Государственное автономное учреждение города Москвы Московский научно-исследовательский и проектный институт жилищного хозяйства «МосжилНИИпроект» (ГАУ «МосжилНИИпроект»)

mgnp@mgnp.mos.ru +7 495 624 40 65 107078, г. Москва, ул. Каланчевская, д. 4/2, стр. 1

Арх. №

**Капитальный ремонт здания,  
расположенного по адресу:  
г. Москва, улица Мясницкая, дом 44, стр. 1**

## **ПРОЕКТНАЯ ДОКУМЕНТАЦИЯ**

### **Раздел 5.**

**Сведения об инженерном оборудовании, о сетях и системах  
инженерно-технического обеспечения.**

### **Подраздел 3.**

**Система водоотведения.**

**2025-00224-01-1-ИОС3**

**Том 5.3**

**Капитальный ремонт здания,  
расположенного по адресу:  
г. Москва, улица Мясницкая, дом 44, стр. 1**

**ПРОЕКТНАЯ ДОКУМЕНТАЦИЯ**

**Раздел 5.**

**Сведения об инженерном оборудовании, о сетях и системах  
инженерно-технического обеспечения.**

**Подраздел 3.**

**Система водоотведения.**

**2025-00224-01-1-ИОСЗ**

**Том 5.3**

Начальник отдела УКПООН



*Е.Ю. Клопова*  
12.25

Е.Ю. Клопова

Начальник отдела

*Е.А. Трофимцев*  
12.25

Е.А. Трофимцев

## Содержание раздела

| №п-п | Наименование проектных материалов                         | Марка листа | Стр. |
|------|-----------------------------------------------------------|-------------|------|
| 1    | Содержание раздела                                        | 1 лист      |      |
| 2    | Состав проектной документации                             | 1 лист      |      |
| 3    | Текстовая часть                                           | На 2 листах |      |
| 4    | План 1-го этажа с сетями канализации. М1:100              | ИОС3-1      |      |
| 5    | План 2-го этажа с сетями канализации. М1:100              | ИОС3-2      |      |
| 6    | План чердака с сетями канализации. М1:100                 | ИОС3-3      |      |
| 7    | План кровли с сетями канализации. М1:100                  | ИОС3-4      |      |
| 8    | Принципиальная схема канализации.                         | ИОС3-5      |      |
| 9    | Спецификация оборудования и материалов                    | ИОС3.СО     |      |
| 10   | Выписка из реестра членов<br>саморегулируемой организации | На 4 листах |      |

|  |  |  |
|--|--|--|
|  |  |  |
|  |  |  |
|  |  |  |
|  |  |  |
|  |  |  |

|              |  |  |  |
|--------------|--|--|--|
| Согласовано  |  |  |  |
|              |  |  |  |
|              |  |  |  |
|              |  |  |  |
| Взам. инв. № |  |  |  |
|              |  |  |  |
|              |  |  |  |
|              |  |  |  |
| Подп. и дата |  |  |  |
|              |  |  |  |
|              |  |  |  |
|              |  |  |  |
| Инв. № подл. |  |  |  |
|              |  |  |  |
|              |  |  |  |
|              |  |  |  |

|          |             |      |       |                                                                                     |       |   |      |        |
|----------|-------------|------|-------|-------------------------------------------------------------------------------------|-------|---|------|--------|
|          |             |      |       |                                                                                     |       | 2025-00224-01-1-ИОС3.С                                                                                            |      |        |
| Изм.     | Кол.уч      | Лист | № док | Подпись                                                                             | Дата  | Капитальный ремонт здания<br>по адресу г. Москва,<br>ул. Мясницкая, д.44, стр.1.                                  |      |        |
| Инженер  | Герасименко |      |       |  | 12.25 |   |      |        |
| Н.Контр. | Миляева     |      |       |  | 12.25 |   |      |        |
| Нач. ОИО | Белоусова   |      |       |  | 12.25 |   |      |        |
|          |             |      |       |                                                                                     |       | Стадия   | Лист | Листов |
|          |             |      |       |                                                                                     |       | П   | 1    | 1      |
|          |             |      |       |                                                                                     |       |  <b>МОСЖИЛ<br/>НИИПРОЕКТ</b> |      |        |

### **Подраздел 5.3 Система водоотведения.**

Раздел «Система водоотведения» разработан на основании «Технического заключения» и «Технического задания» с учетом действующих нормативных документов.

Здание – административное (не жилое)

Этажность – 2-х этажное с чердаком.

*Капитальный ремонт производится только в обозначенных на планах кабинетах.*

Помещения, не входящие в зону ремонта, заштрихованы.

### **Существующая система канализации**

*В здании смонтирована система внутренней канализации из чугунных раструбных канализационных труб 100, 50мм с выпуском в наружную канализационную сеть.*

Система експлуатується з моменту вводу будівлі в експлуатацію.

Магистральные трубопроводы выполнены из чугунных раструбных труб  $D=100\text{ мм}$ , проложены скрыто под полом 1 этажа. Имеются частые засоры, трещины в раструбных соединениях, значительная внешняя коррозия на видимых участках; Стояк и отводные трубы от санитарно-технических приборов  $D=100, 50\text{ мм}$  из чугунных раструбных канализационных труб проложены открыто, частично за облицовкой стен. Имеется значительная внешняя коррозия на отдельных участках труб, трещины в раструбах, протечки через раструбные соединения из-за их разгерметизации.

С учетом срока эксплуатации и выявленных при проведении обследования дефектов согласно ГОСТ 31937-2024 и СП 454.1325800.2019 «Здания жилые многоквартирные», система внутренней канализации здания находится в ограниченно-работоспособном состоянии. При проведении в здании ремонта необходимо заменить систему внутренней канализации на новую.

### **Существующая система внутреннего водостока**

Здание имеет скатную кровлю. Отвод дождевых и талых вод с кровли осуществляется трубами по фасаду здания.

### **Основные решения по канализации.**

Проектом предусматривается замена системы канализации по сущ. схеме. Отвод сточных вод от санитарно-технических приборов, установленных в помещениях, осуществляется в сущ. выпуск канализации ф100 под полом 1 этажа здания.

Для прочистки сети предусмотрена установка ревизий и прочисток в местах, удобных для их обслуживания. Для замены/ремонта трубопровода требуется осуществить разбор конструкции пола (ЦСП, гидроизоляции, фанеры, пароизоляции) 1 этажа.

*Проектируемые нагрузки на канализацию не превышают существующие.*

**Внутренние сети канализации проектируются:**

- из раструбных канализационных труб ПВХ ф110-50 стояки и отводы от сантехприборов.

- из чугунных раструбных труб ф100 под полом 1 этажа здания.

Отводы от сантехприборов прокладываются над полом помещения.

Монтаж трубопроводов выполнять с соответствующим уклоном  $i=0,02-0,03$  (для труб  $\phi 110-50$ ) по ходу движения жидкости. Для прочистки и промывки системы канализации проектом предусмотрена установка прочисток и ревизий

При проходе канализационных стояков из труб ПВХ наружным диаметром Ø110-50мм сквозь перекрытия, на каждом стояке, на каждом этаже под перекрытием (в проеме перекрытия) зданий высотой до 75 м, следует устанавливать противопожарную муфту типа «ОГРАКС-ПМ-110»-«ОГРАКС-ПМ-50» длиной 60мм с огнезащитным и терморасширяющимся материалом «ОГРАКС-Л».

|              |              |   |        |      |       |          |      |
|--------------|--------------|---|--------|------|-------|----------|------|
| Взам. инв. № | Подп. и дата | <p>Внутренние сети канализации проектируются:</p> <p>- из раструбных канализационных труб ПВХ ф110-50 стояки и отводы от сантехприборов.</p> <p>- из чугунных раструбных труб ф100 под полом 1 этажа здания.</p> <p>Отводы от сантехприборов прокладываются над полом помещения.</p> <p>Монтаж трубопроводов выполнять с соответствующим уклоном <math>i=0,02-0,03</math> (для труб ф110-50) по ходу движения жидкости. Для прочистки и промывки системы канализации проектом предусмотрена установка прочисток и ревизий</p> <p>При проходе канализационных стояков из труб ПВХ наружным диаметром Ø110-50мм сквозь перекрытия, на каждом стояке, на каждом этаже под перекрытием (в проеме перекрытия) зданий высотой до 75 м, следует устанавливать противопожарную муфту типа «ОГРАКС-ПМ-110»-«ОГРАКС-ПМ-50» -длиной 60мм с огнезащитным и терморасширяющимся материалом «ОГРАКС-Л».</p> |        |      |       |          | Лист |
|              |              | 2025-00224-01-1-ИОСЗ   |        |      |       |          |      |
| Инв. № подл. |              |   |        |      |       |          |      |
|              |              |   |        |      |       | 12.12.25 |      |
|              |              | Изм.   | Кол.уч | Лист | Недок | Подп.    | Дата |

Сеть бытовой канализации вентилируется через стояки, выводимые на 0,20 м от скатной неэксплуатируемой кровли, в случае выхода стояка рядом с вентиляцией – на 0,1 м выше обреза вентиляционной шахты.

Проектом предусмотрена установка двухоборотных сифонов на стояках канализации для отвода конденсата от кондиционеров (по заданию подраздела ОВ).

Присоединение труб для отвода конденсата от кондиционеров к системе внутренней канализации предусматривается через двухоборотный сифон с разрывом струи 20 мм.

Проектом предусматривается замена санитарно-технических приборов.

Предусматривается крепление всех трубопроводов в необходимых местах к строительным конструкциям.

Средства крепления трубопроводов и расстояние между ними принимаются в соответствии СП 73.13330.2016. Стояки прокладываются скрыто в специально отведенных для этого нишах.

Для прочистки сети предусмотрена установка ревизий и прочисток в местах, удобных для их обслуживания.

На стояках и коллекторах применены косые фасонные части, включая отводы, тройники, крестовины.

### Мероприятия по энергосбережению

1. Предусмотрена установка новой водосберегающей сантехнической запорной арматуры.

### Общие указания.

При сверлении отверстий в стенах и перекрытиях необходимо соблюдать меры по сохранению рабочей арматуры, плит перекрытий, венткоробов и электропроводки.

Монтаж и приемку систем производить в соответствии с СП 73.13330.2016

При проходе канализационного стояка наружным диаметром Ø100мм сквозь перекрытия на каждом стояке, на каждом этаже под перекрытием (в проеме перекрытия) зданий высотой до 75м, следует устанавливать противопожарную муфту типа «ОГРАКС-ПМ-110» длиной 60мм с огнезащитным и терморасширяющимся материалом «ОГРАКС-Л».

### Перечень нормативных документов, использованных при разработке проектной документации

- ГОСТ Р 21.1101-2013 «Система проектной документации для строительства (СПДС). Основные требования к проектной и рабочей документации»
  - Постановление № 87 от 16.02.2008 «О составе разделов проектной документации и требования к их содержанию» (с изменениями на 23 января 2016 г.)
  - СП 30.13330.2020 «Внутренний водопровод и канализация зданий»
  - СП 10.13130.2020 «Внутренний противопожарный водопровод»
- СП 73.13330.2016 «Внутренние санитарно-технические системы зданий»

|      |        |      |       |       |          |                      |      |
|------|--------|------|-------|-------|----------|----------------------|------|
| Изм. | Коп.уч | Лист | Недок | Подп. | Дата     | 2025-00224-01-1-ИОСЗ | Лист |
|      |        |      |       |       |          |                      |      |
|      |        |      |       |       | 12.12.25 |                      |      |
|      |        |      |       |       |          |                      |      |

|      |        |      |       |       |      |
|------|--------|------|-------|-------|------|
| Изм. | Коп.уч | Лист | Недок | Подп. | Дата |
|------|--------|------|-------|-------|------|

|      |
|------|
| Изм. |
|------|

[illegible]

Помещения, не входящие в зону ремонта

| Экспликация помещений 1-го этажа |                                                    |                           |              |
|----------------------------------|----------------------------------------------------|---------------------------|--------------|
| № п/п                            | Наименование помещений                             | Площадь<br>м <sup>2</sup> | Кат.<br>пом. |
| 101                              | Лестница №1 (ЛК ти 1)                              | 22,9                      |              |
| 101А                             | Пост охраны                                        |                           |              |
| 102                              | Лестница № 2 (ЛК тип 1)                            | 17,7                      |              |
| 103                              | Коридор                                            | 39,4                      |              |
| 104                              | Кабинет заместителя прокурора                      | 15,9                      |              |
| 105                              | Комната отдыха заместителя прокурора               | 5,3                       |              |
| 106                              | Кабинет помощника прокурора / прием граждан<br>МГН | 25,6                      |              |
| 107                              | Кабинет*                                           | 4,8                       |              |
| 108                              | Архив                                              | 7,9                       | В4           |
| 109                              | Ввод водопровода                                   | 4,3                       |              |
| 110                              | Кабинет для приема граждан                         | 4,9                       |              |
| 111                              | Санузел                                            | 1,8                       |              |
| 112                              | Санузел МГН                                        | 6,7                       |              |
| 113                              | Санузел заместителя прокурора                      | 2,8                       |              |
|                                  | ИТОГО:                                             | 160                       |              |

| Помещения не входящие в зону ремонта |                        |                           |              |
|--------------------------------------|------------------------|---------------------------|--------------|
| N п/п                                | Наименование помещений | Площадь<br>м <sup>2</sup> | Кат.<br>пом. |
| 114                                  | Офисное помещение      | 15,7                      |              |
| 115                                  | Офисное помещение      | 15,6                      |              |
| 116                                  | Офисное помещение      | 23,0                      |              |
| 117                                  | Офисное помещение      | 13,8                      |              |
| 118                                  | Офисное помещение      | 13,8                      |              |
| 119                                  | Офисное помещение      | 17,0                      |              |
| 120                                  | Офисное помещение      | 9,4                       |              |
| 121                                  | Офисное помещение      | 10,1                      |              |
|                                      | ИТОГО:                 | 118,4                     |              |

\* - кабинет для работы с секретными документами


1. В здании предусматривается капитальный ремонт, размеры проемов в капитальных стенах увеличению не подлежат.

|              |         |                 |                        |                         |         |                                                                            |  |                                                                                       |                     |        |  |  |
|--------------|---------|-----------------|------------------------|-------------------------|---------|----------------------------------------------------------------------------|--|---------------------------------------------------------------------------------------|---------------------|--------|--|--|
|              |         |                 |                        |                         |         | 2025-00224-01-1-ИОСЗ                                                       |  |                                                                                       |                     |        |  |  |
|              |         |                 |                        |                         |         | Капитальный ремонт здания по адресу г. Москва, ул. Мясницкая, д.44, стр.1. |  |                                                                                       |                     |        |  |  |
| Изм.         | Кол.уч. | Лист            | № док.                 | Подпись                 | Дата    | Капитальный ремонт                                                         |  | Стадия                                                                                | Лист                | Листов |  |  |
| Разработал   |         |                 | Герасименко Н.С.       | <i>Н.С. Герасименко</i> | 12.2025 |                                                                            |  | П                                                                                     | 1                   |        |  |  |
|              |         |                 |                        |                         |         |                                                                            |  |                                                                                       |                     |        |  |  |
|              |         |                 |                        |                         |         | План 1-го этажа с сетями канализации. М1:100                               |  |  | МОСЖИЛ<br>НИИПРОЕКТ |        |  |  |
| Н. контроль  |         | Миляева О.А.    | <i>О.А. Миляева</i>    | 12.2025                 |         |                                                                            |  |                                                                                       |                     |        |  |  |
| Нач. ОПИС №1 |         | Белосухова Д.С. | <i>Д.С. Белосухова</i> | 12.2025                 |         |                                                                            |  |                                                                                       |                     |        |  |  |

Согласовано

|              |              |              |
|--------------|--------------|--------------|
| Инв. № подл. | Подп. и дата | Взам. инв. № |
|--------------|--------------|--------------|

План 2-го этажа на отм. +3.800  
М 1:100

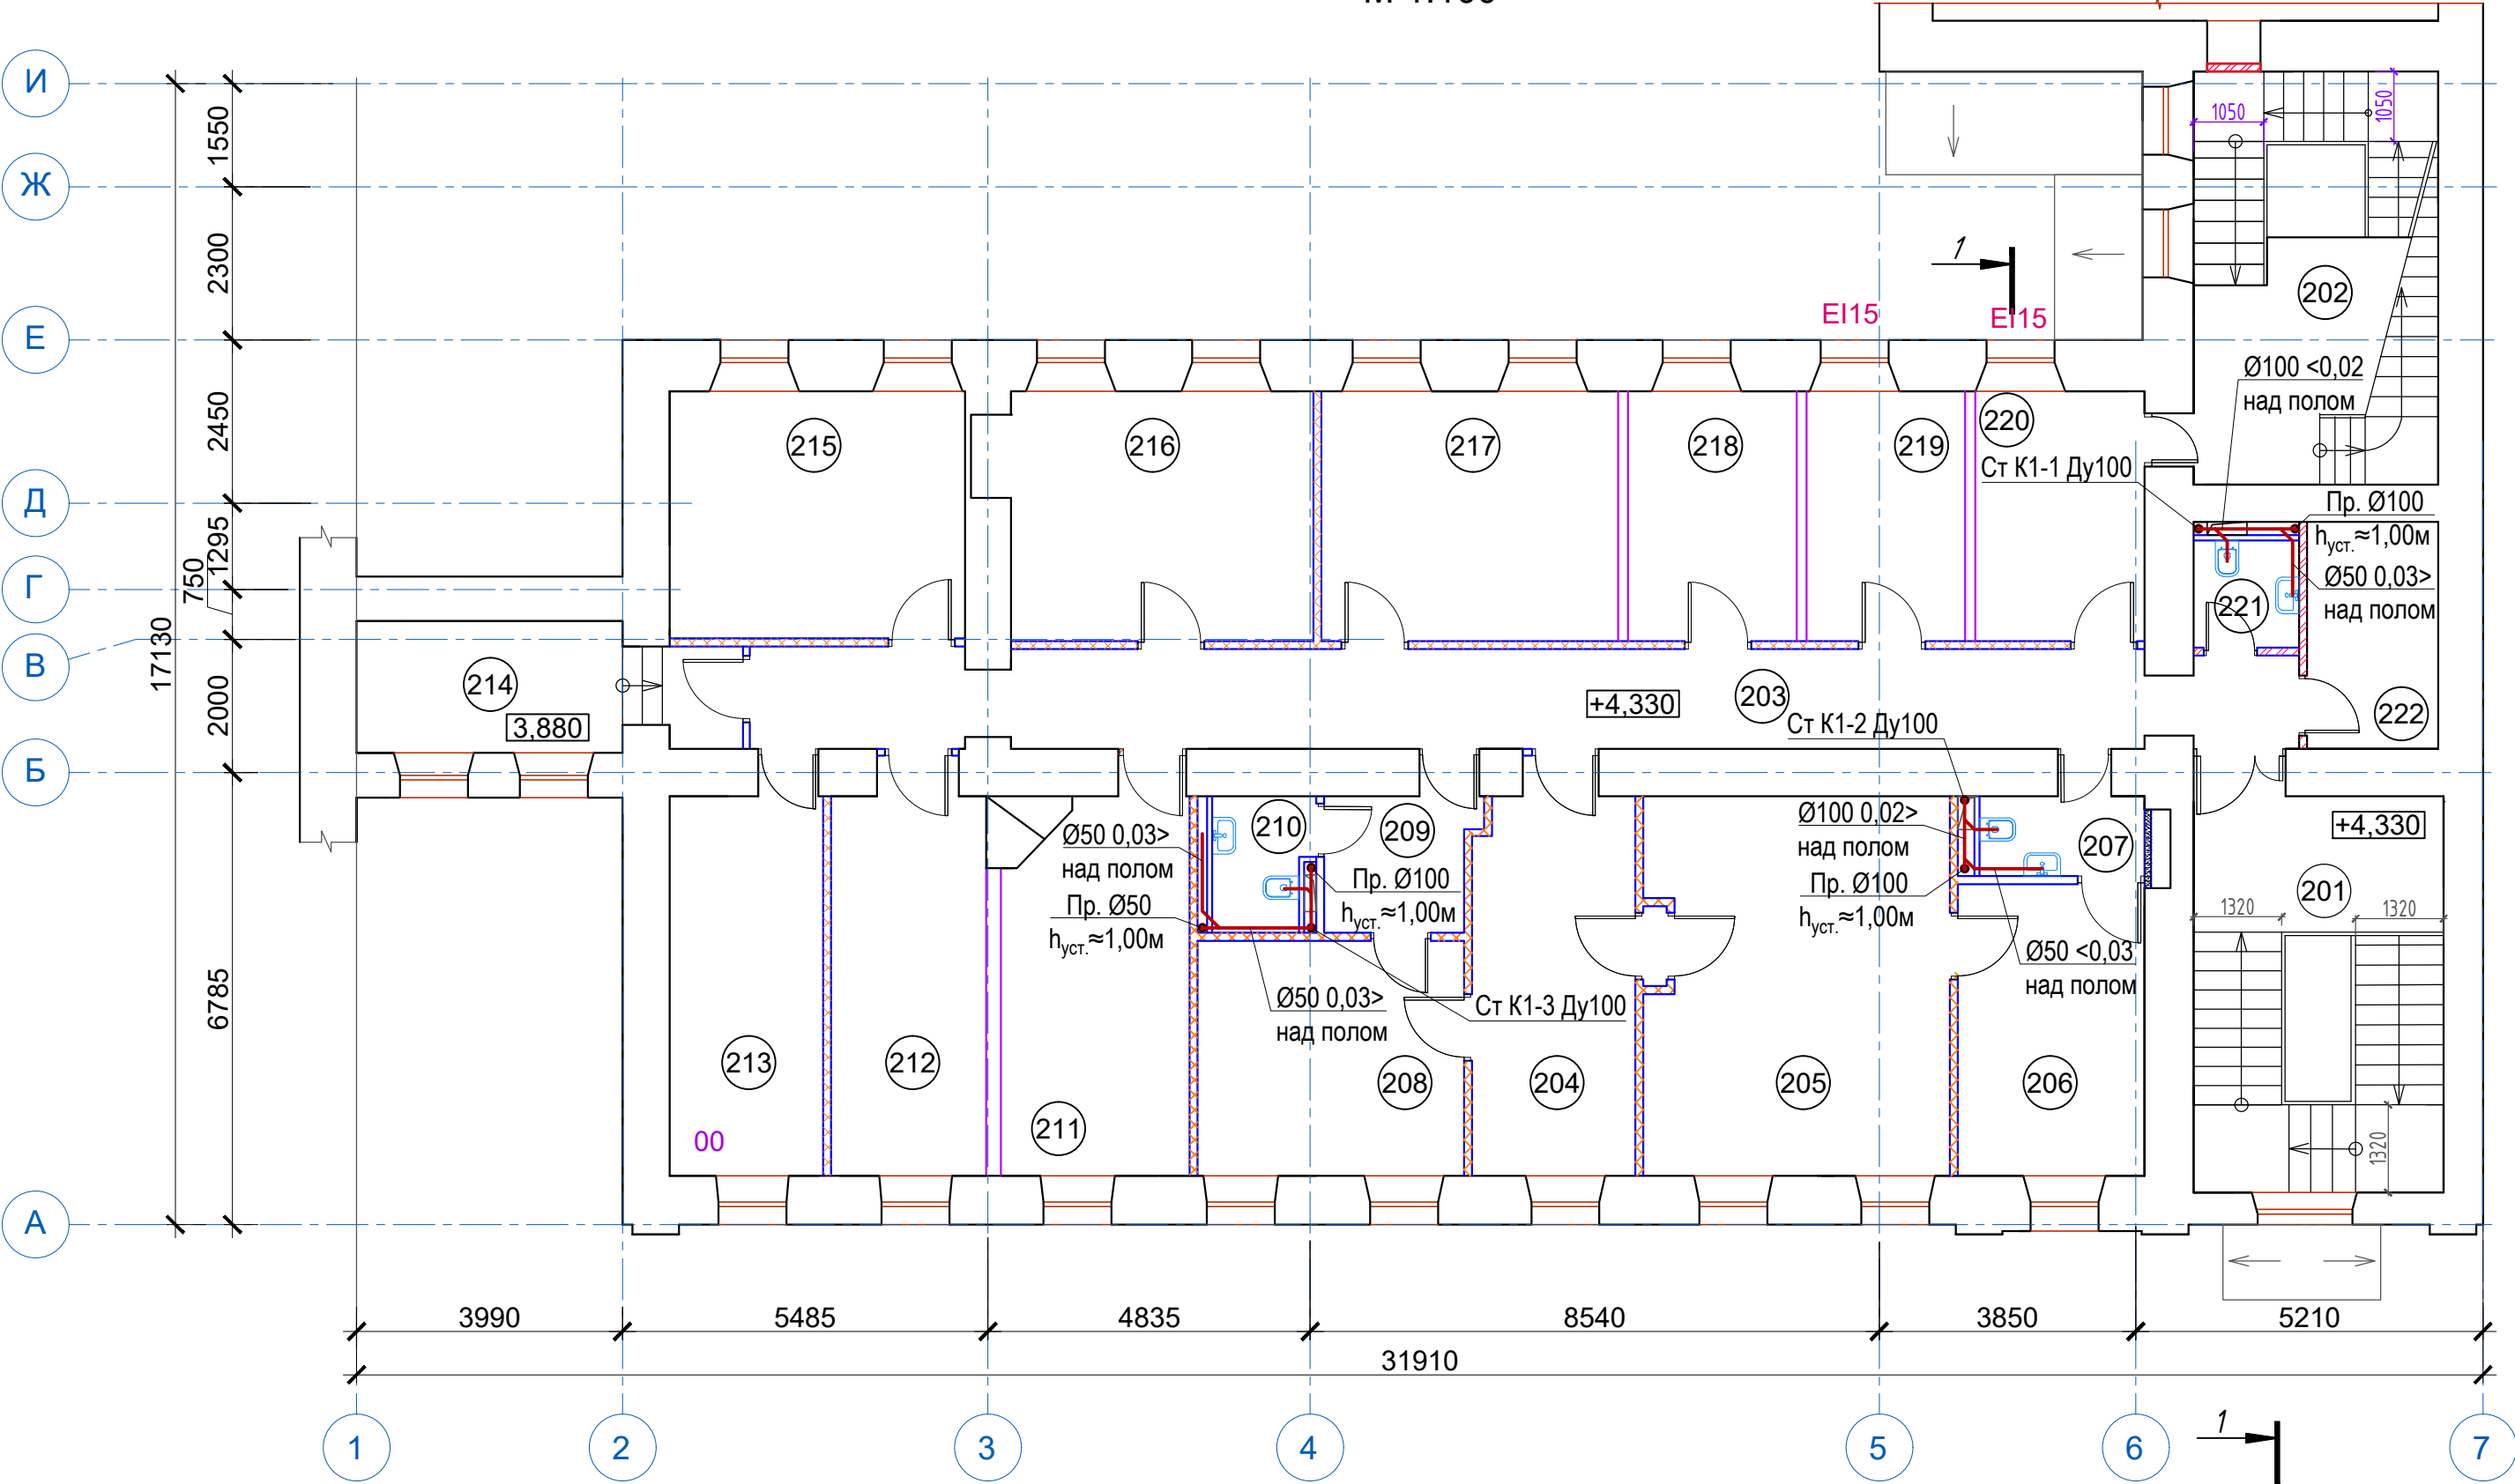


| Экспликация помещений 2-го этажа |                                           |            |           |
|----------------------------------|-------------------------------------------|------------|-----------|
| N п/п                            | Наименование помещений                    | Площадь м² | Кат. пом. |
| 201                              | Лестница № 1 (ЛК тип 1)                   | 23,1       |           |
| 202                              | Лестница № 2 (ЛК тип 1)                   | 22,8       |           |
| 203                              | Коридор                                   | 34,2       |           |
| 204                              | Приемная прокурора                        | 14,5       |           |
| 205                              | Кабинет прокурора / видеонаблюдение       | 25,9       |           |
| 206                              | Комната отдыха прокурора                  | 12,3       |           |
| 207                              | Сан. узел прокурора                       | 3,5        |           |
| 208                              | Кабинет 1-го заместителя прокурора        | 14,1       |           |
| 209                              | Комната отдыха 1-го заместителя прокурора | 5,0        |           |
| 210                              | Сан. узел 1-го заместителя прокурора      | 2,6        |           |
| 211                              | Кабинет помощника прокурора               | 15,9       |           |
| 212                              | Кабинет помощника прокурора               | 14,0       |           |
| 213                              | Кабинет помощника прокурора               | 13,7       |           |
| 214                              | Архив                                     | 10,3       | ВЗ        |
| 215                              | Кабинет помощника прокурора               | 16,4       |           |
| 216                              | Кабинет помощника прокурора               | 17,0       |           |
| 217                              | Зал совещаний                             | 16,7       |           |
| 218                              | Кабинет помощника прокурора               | 9,5        |           |
| 219                              | Кабинет помощника прокурора               | 8,9        |           |
| 220                              | Комната приёма пищи                       | 9,5        |           |
| 221                              | Санузел                                   | 2,5        |           |
| 222                              | Серверная                                 | 7,6        | ВЗ        |
| Итого:                           |                                           | 300        |           |

|              |  |  |  |  |  |
|--------------|--|--|--|--|--|
| Создано      |  |  |  |  |  |
|              |  |  |  |  |  |
| Взам. инв. № |  |  |  |  |  |
|              |  |  |  |  |  |
| Подп. и дата |  |  |  |  |  |
|              |  |  |  |  |  |
| Инв. № подл. |  |  |  |  |  |
|              |  |  |  |  |  |

|                                                                            |                  |         |         |                  |      |
|----------------------------------------------------------------------------|------------------|---------|---------|------------------|------|
| 2025-00224-01-1-ИОС 3                                                      |                  |         |         |                  |      |
| Капитальный ремонт здания по адресу г. Москва, ул. Мясницкая, д.44, стр.1. |                  |         |         |                  |      |
| Изм.                                                                       | Колуч.           | Лист    | № док.  | Подпись          | Дата |
| Разработал                                                                 | Герасименко Н.С. | Мерас   | 12.2025 |                  |      |
| Капитальный ремонт                                                         |                  |         |         | Стадия           | Лист |
|                                                                            |                  |         |         | 17               | 2    |
| План 2-го этажа с сетями канализации. М1:100                               |                  |         |         | МОСЖИЛ НИИПРОЕКТ |      |
| Н. контроль                                                                | Милеева О.А.     | 12.2025 |         |                  |      |
| Нач. ОПИС №1                                                               | Белоусова Д.П.   | 12.2025 |         |                  |      |

План чердака М 1:100

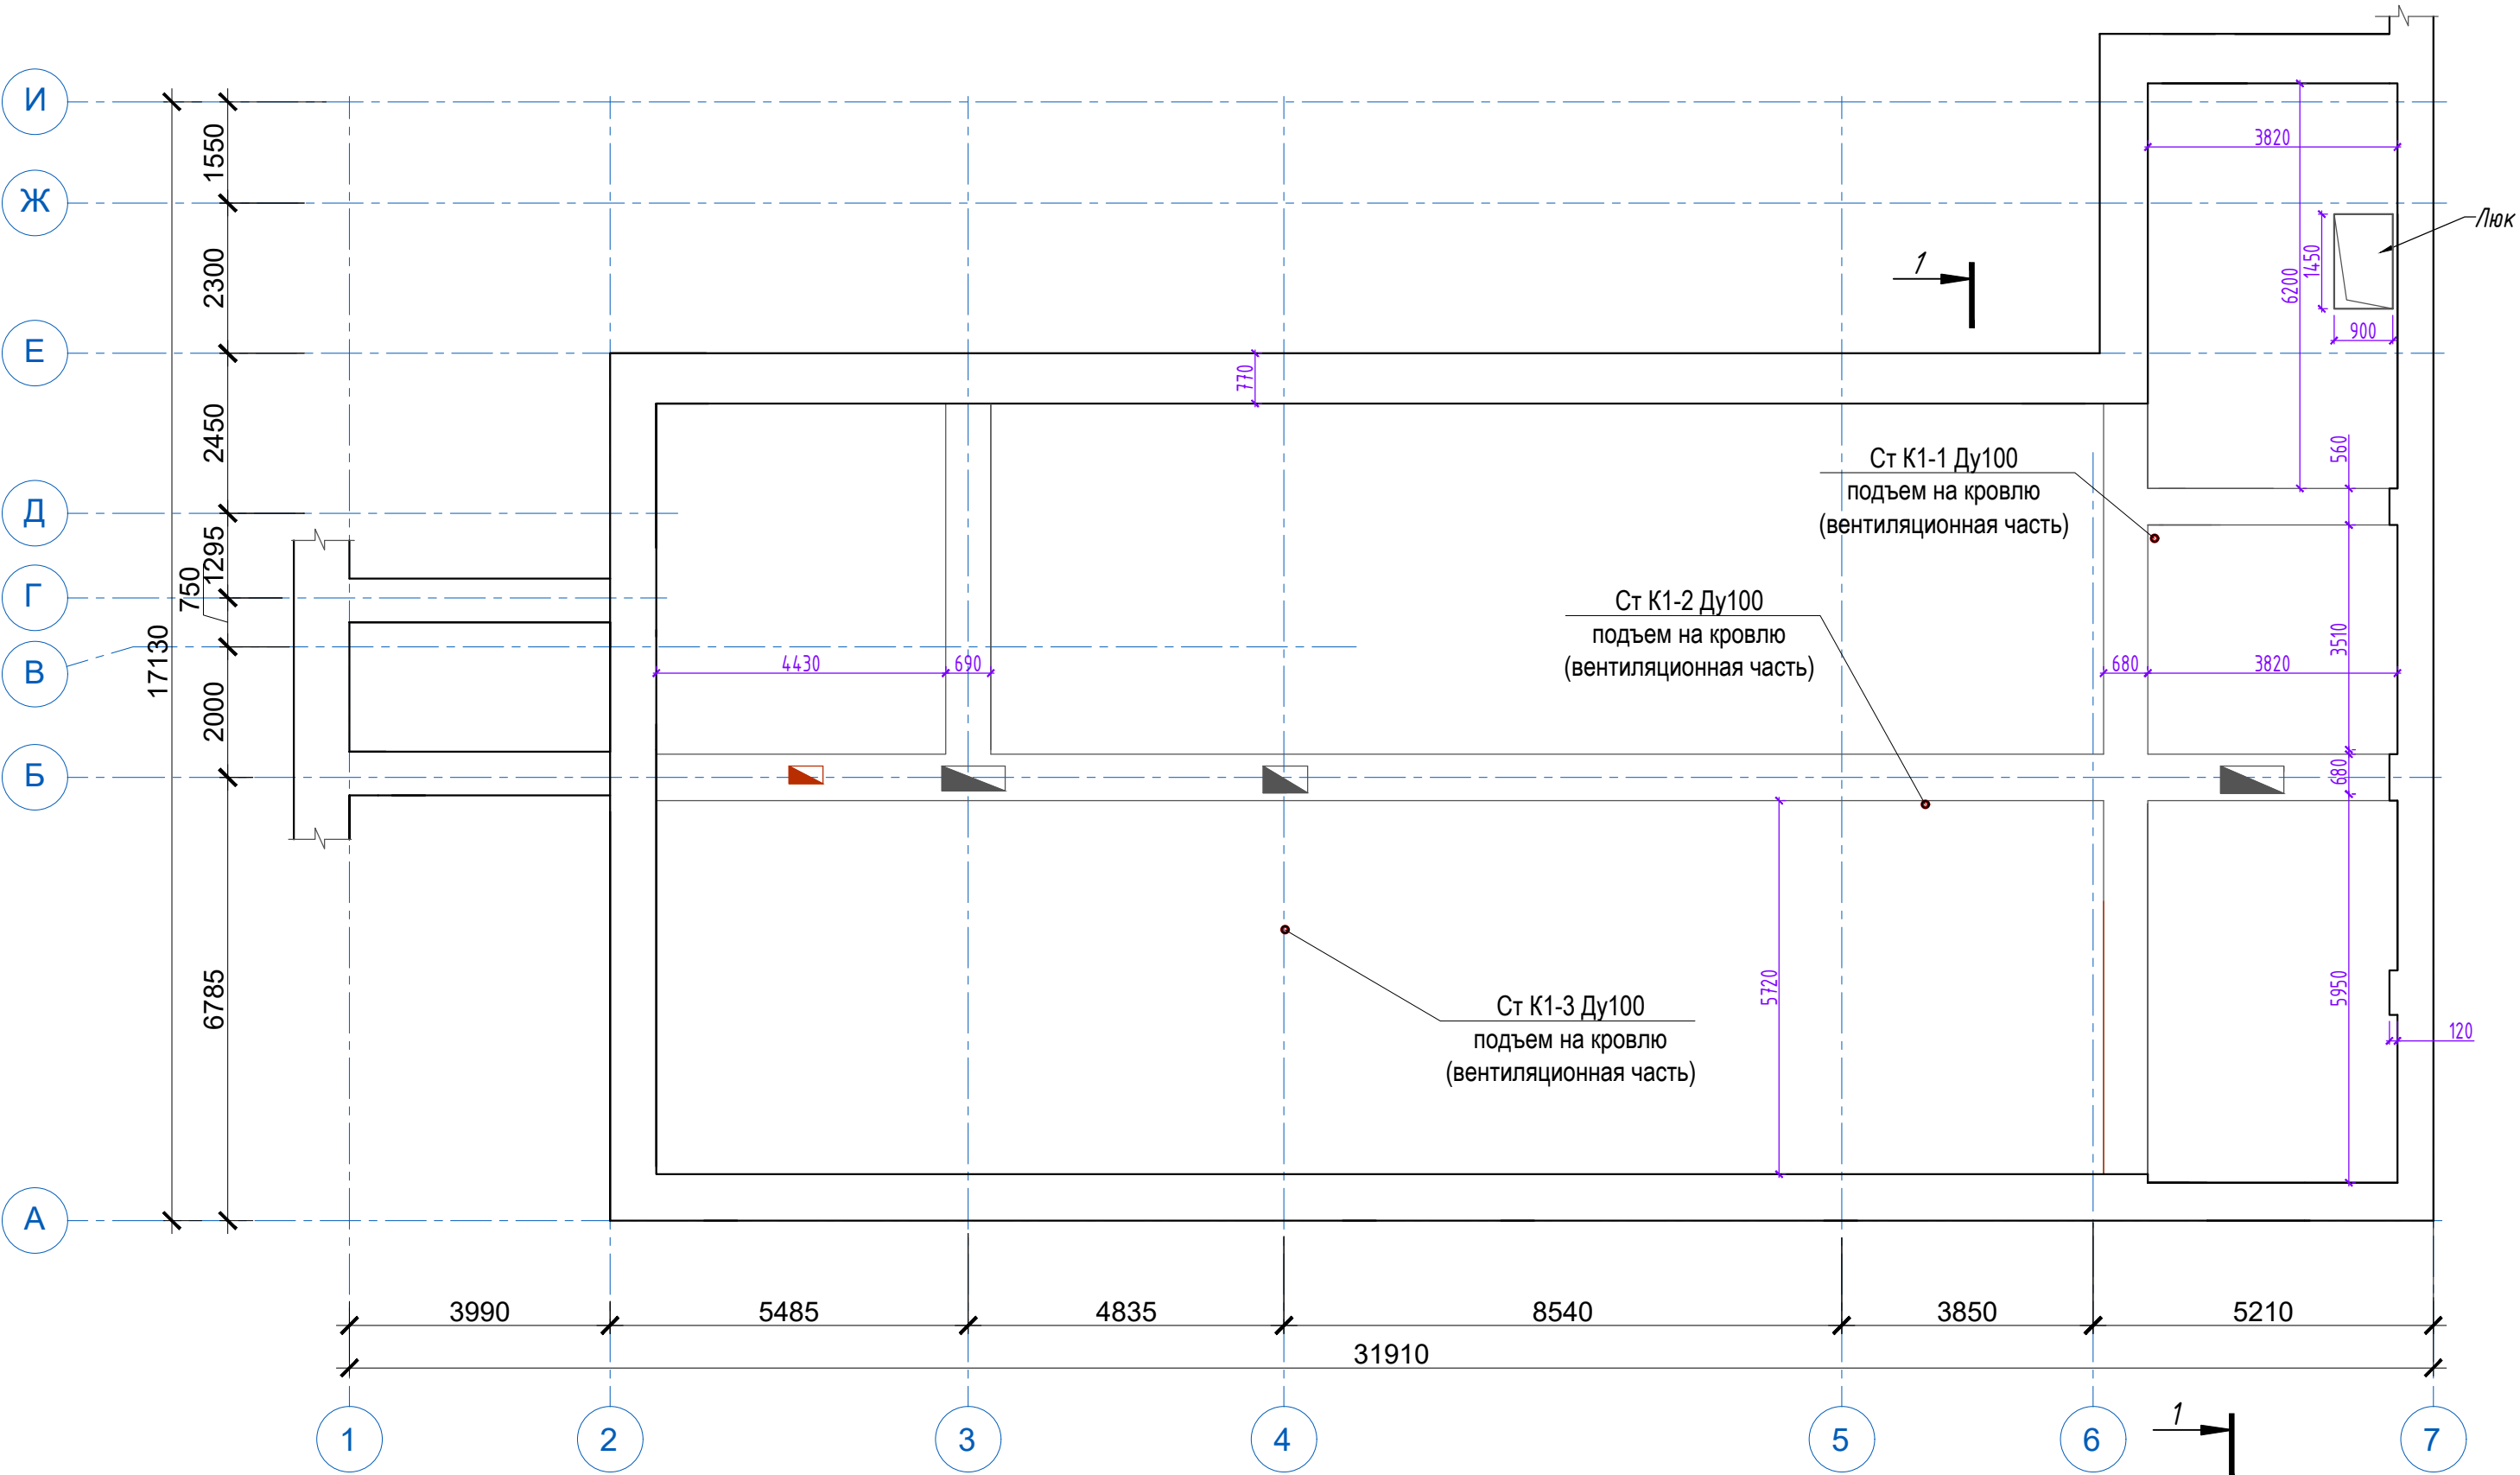


|              |  |  |  |
|--------------|--|--|--|
| Создано      |  |  |  |
|              |  |  |  |
| Взам. инв. № |  |  |  |
|              |  |  |  |
| Подп. и дата |  |  |  |
|              |  |  |  |
| Инв. № подл. |  |  |  |
|              |  |  |  |

|                                                                            |                  |         |         |         |      |                                            |
|----------------------------------------------------------------------------|------------------|---------|---------|---------|------|--------------------------------------------|
| 2025-00224-01-1-ИОС 3                                                      |                  |         |         |         |      |                                            |
| Капитальный ремонт здания по адресу г. Москва, ул. Мясницкая, д.44, стр.1. |                  |         |         |         |      |                                            |
| Изм.                                                                       | Колуч.           | Лист    | № док.  | Подпись | Дата | Капитальный ремонт                         |
| Разработал                                                                 | Герасименко Н.С. | Мерас   | 12.2025 |         |      |                                            |
|                                                                            |                  |         |         |         |      | План чердака с сетями канализации. М1:100. |
| Н. контроль                                                                | Миляева О.А.     | 12.2025 |         |         |      |                                            |
| Нач. ОПИС №1                                                               | Белоусова Д.П.   | 12.2025 |         |         |      |                                            |
|                                                                            |                  |         |         |         |      | Стадия                                     |
|                                                                            |                  |         |         |         |      | Лист                                       |
|                                                                            |                  |         |         |         |      | Листов                                     |
|                                                                            |                  |         |         |         |      | 17                                         |
|                                                                            |                  |         |         |         |      | 3                                          |
|                                                                            |                  |         |         |         |      |                                            |




План кровли М 1:100

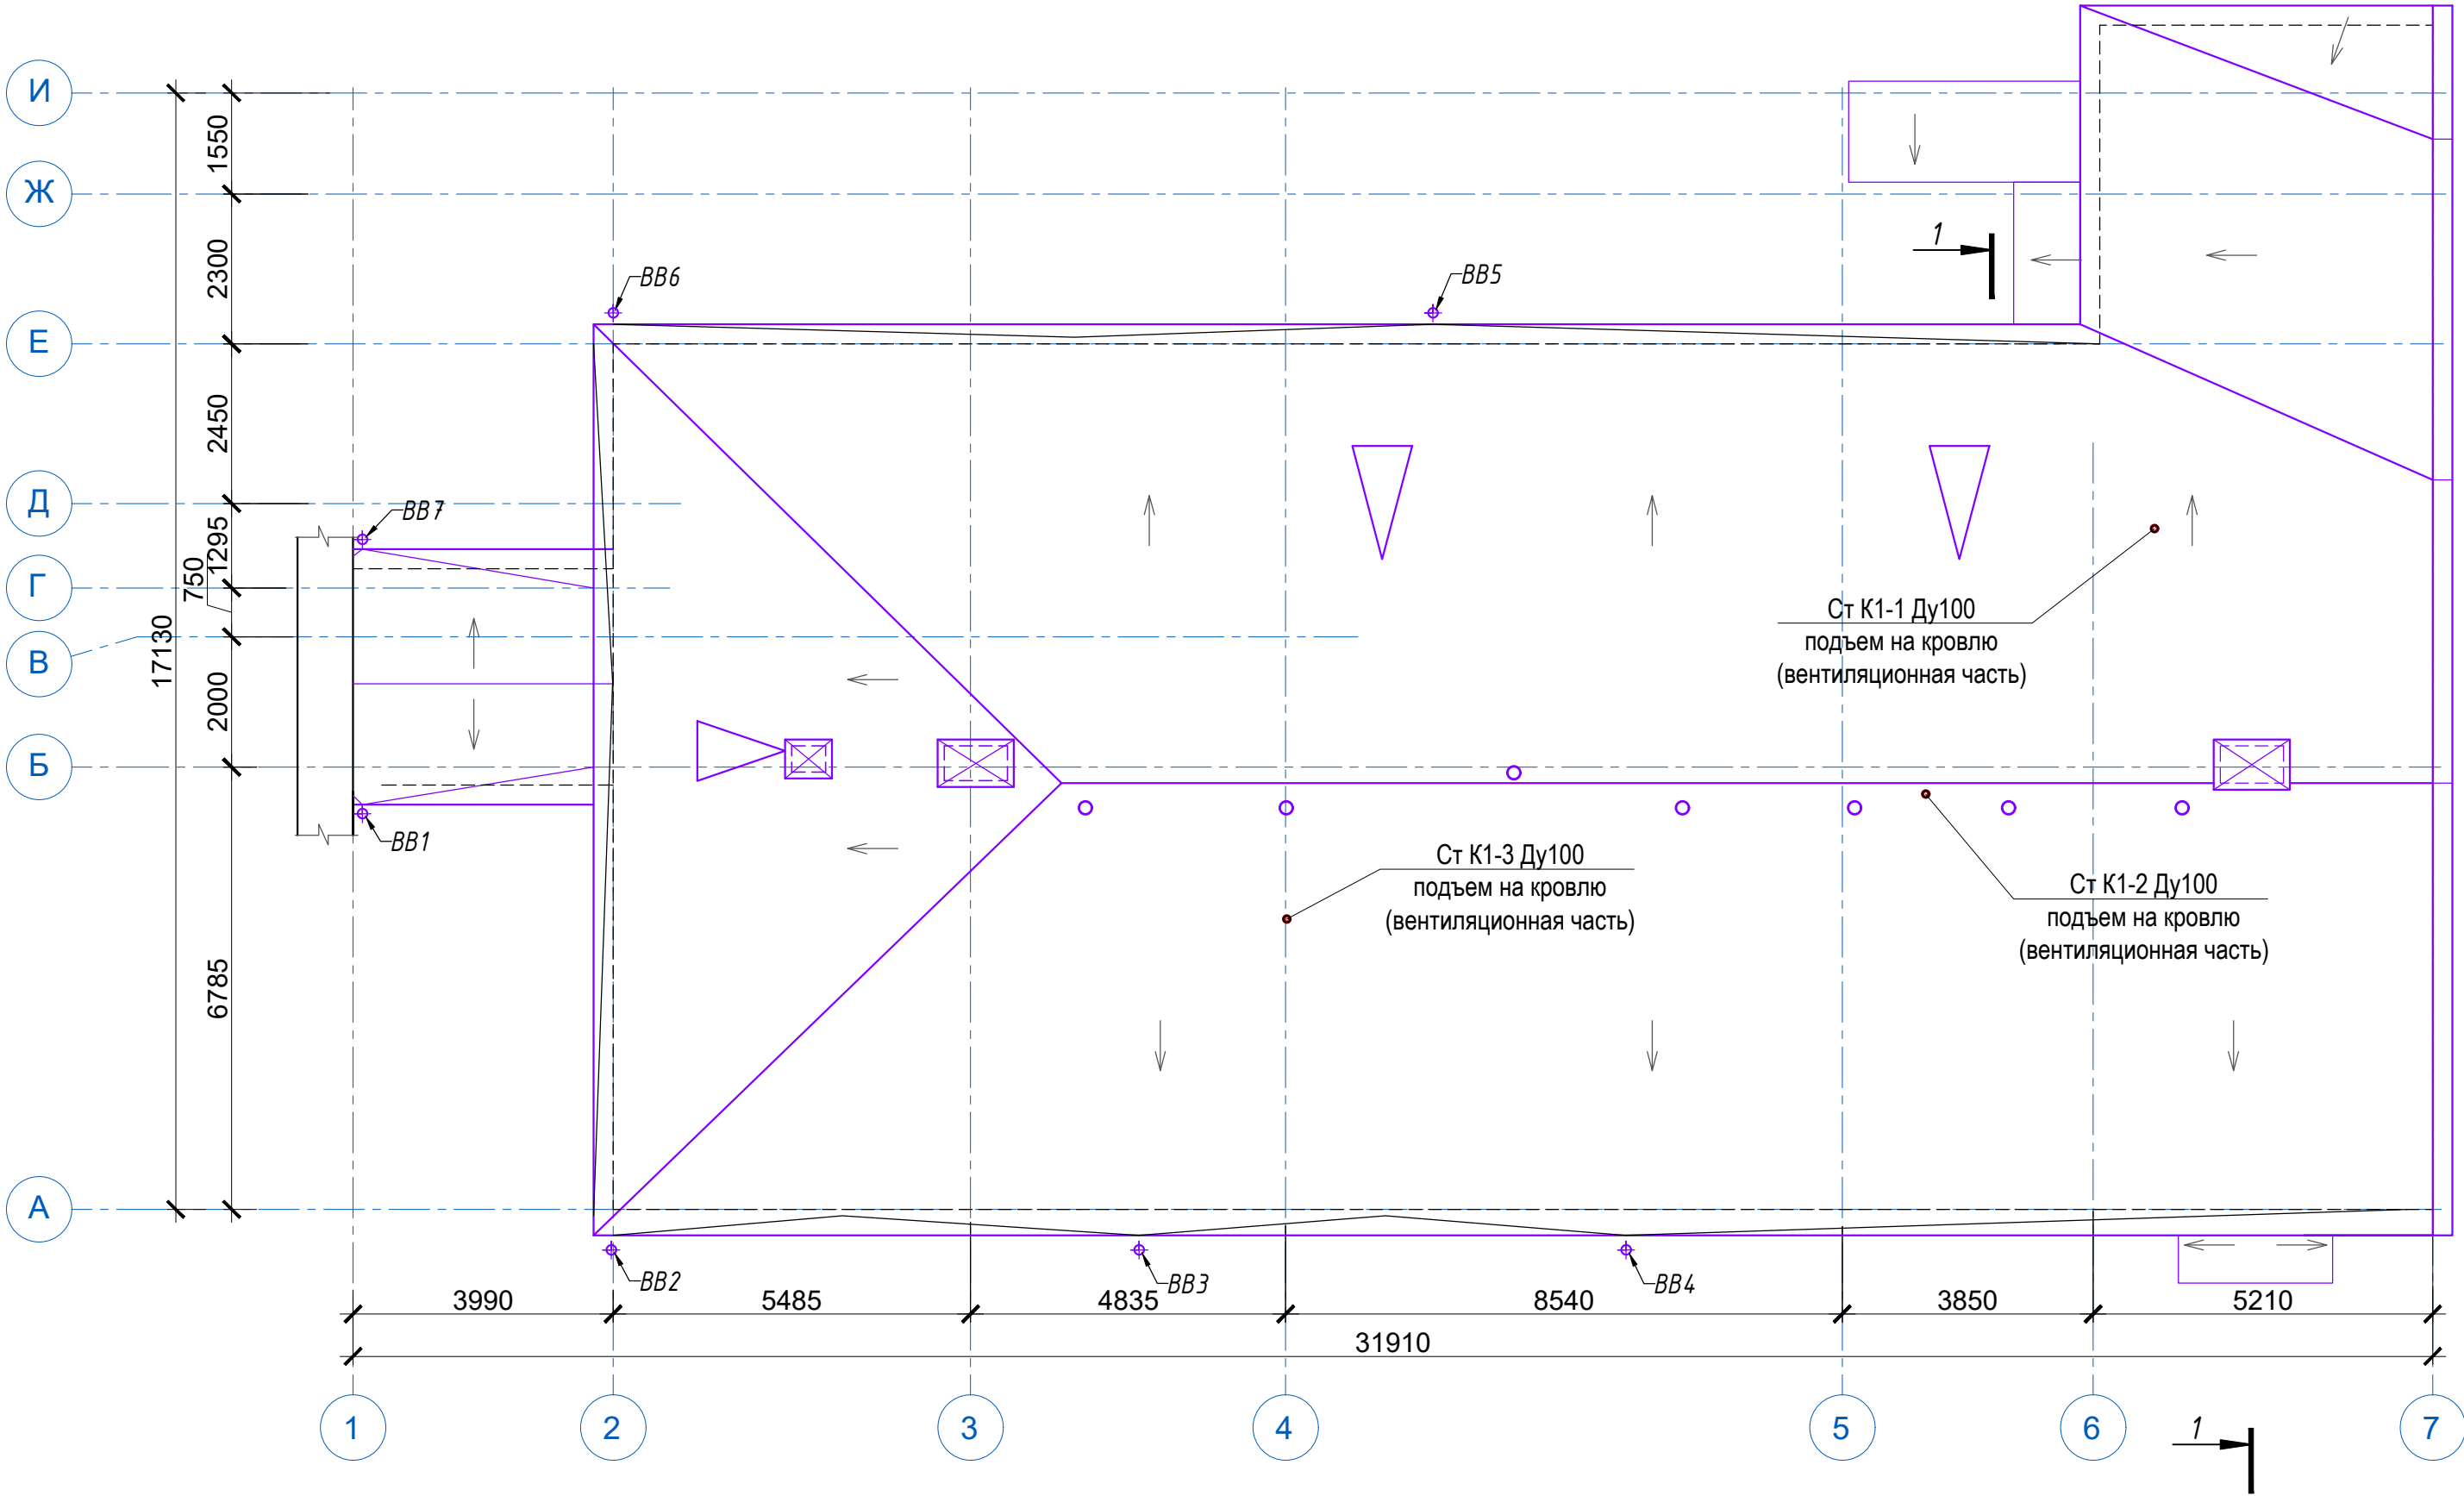

|              |  |  |  |
|--------------|--|--|--|
| Создано      |  |  |  |
|              |  |  |  |
|              |  |  |  |
|              |  |  |  |
| Взам. инв. № |  |  |  |
|              |  |  |  |
|              |  |  |  |
|              |  |  |  |
| Подп. и дата |  |  |  |
|              |  |  |  |
|              |  |  |  |
|              |  |  |  |
| Инв. № подл. |  |  |  |
|              |  |  |  |
|              |  |  |  |
|              |  |  |  |

|                                                                            |                  |         |                                           |         |      |                    |
|----------------------------------------------------------------------------|------------------|---------|-------------------------------------------|---------|------|--------------------|
| 2025-00224-01-1-ИОС 3                                                      |                  |         |                                           |         |      |                    |
| Капитальный ремонт здания по адресу г. Москва, ул. Мясницкая, д.44, стр.1. |                  |         |                                           |         |      |                    |
| Изм.                                                                       | Колуч.           | Лист    | № док.                                    | Подпись | Дата | Капитальный ремонт |
| Разработал                                                                 | Герасименко Н.С. | Мерасел | 12.2025                                   |         |      |                    |
|                                                                            |                  |         |                                           |         |      | Стадия             |
|                                                                            |                  |         |                                           |         |      | Лист               |
|                                                                            |                  |         |                                           |         |      | Листов             |
|                                                                            |                  |         |                                           |         |      | 17                 |
|                                                                            |                  |         |                                           |         |      | 4                  |
|                                                                            |                  |         |                                           |         |      |                    |
| Н. контроль                                                                | Миляева О.А.     | 12.2025 | План кровли с сетями канализации. М1:100. |         |      |                    |
| Нач. ОПИС №1                                                               | Белоусова Д.П.   | 12.2025 |                                           |         |      |                    |
|                                                                            |                  |         |                                           |         |      | МОСЖИЛ НИИПРОЕКТ   |

Принципиальная схема канализации.

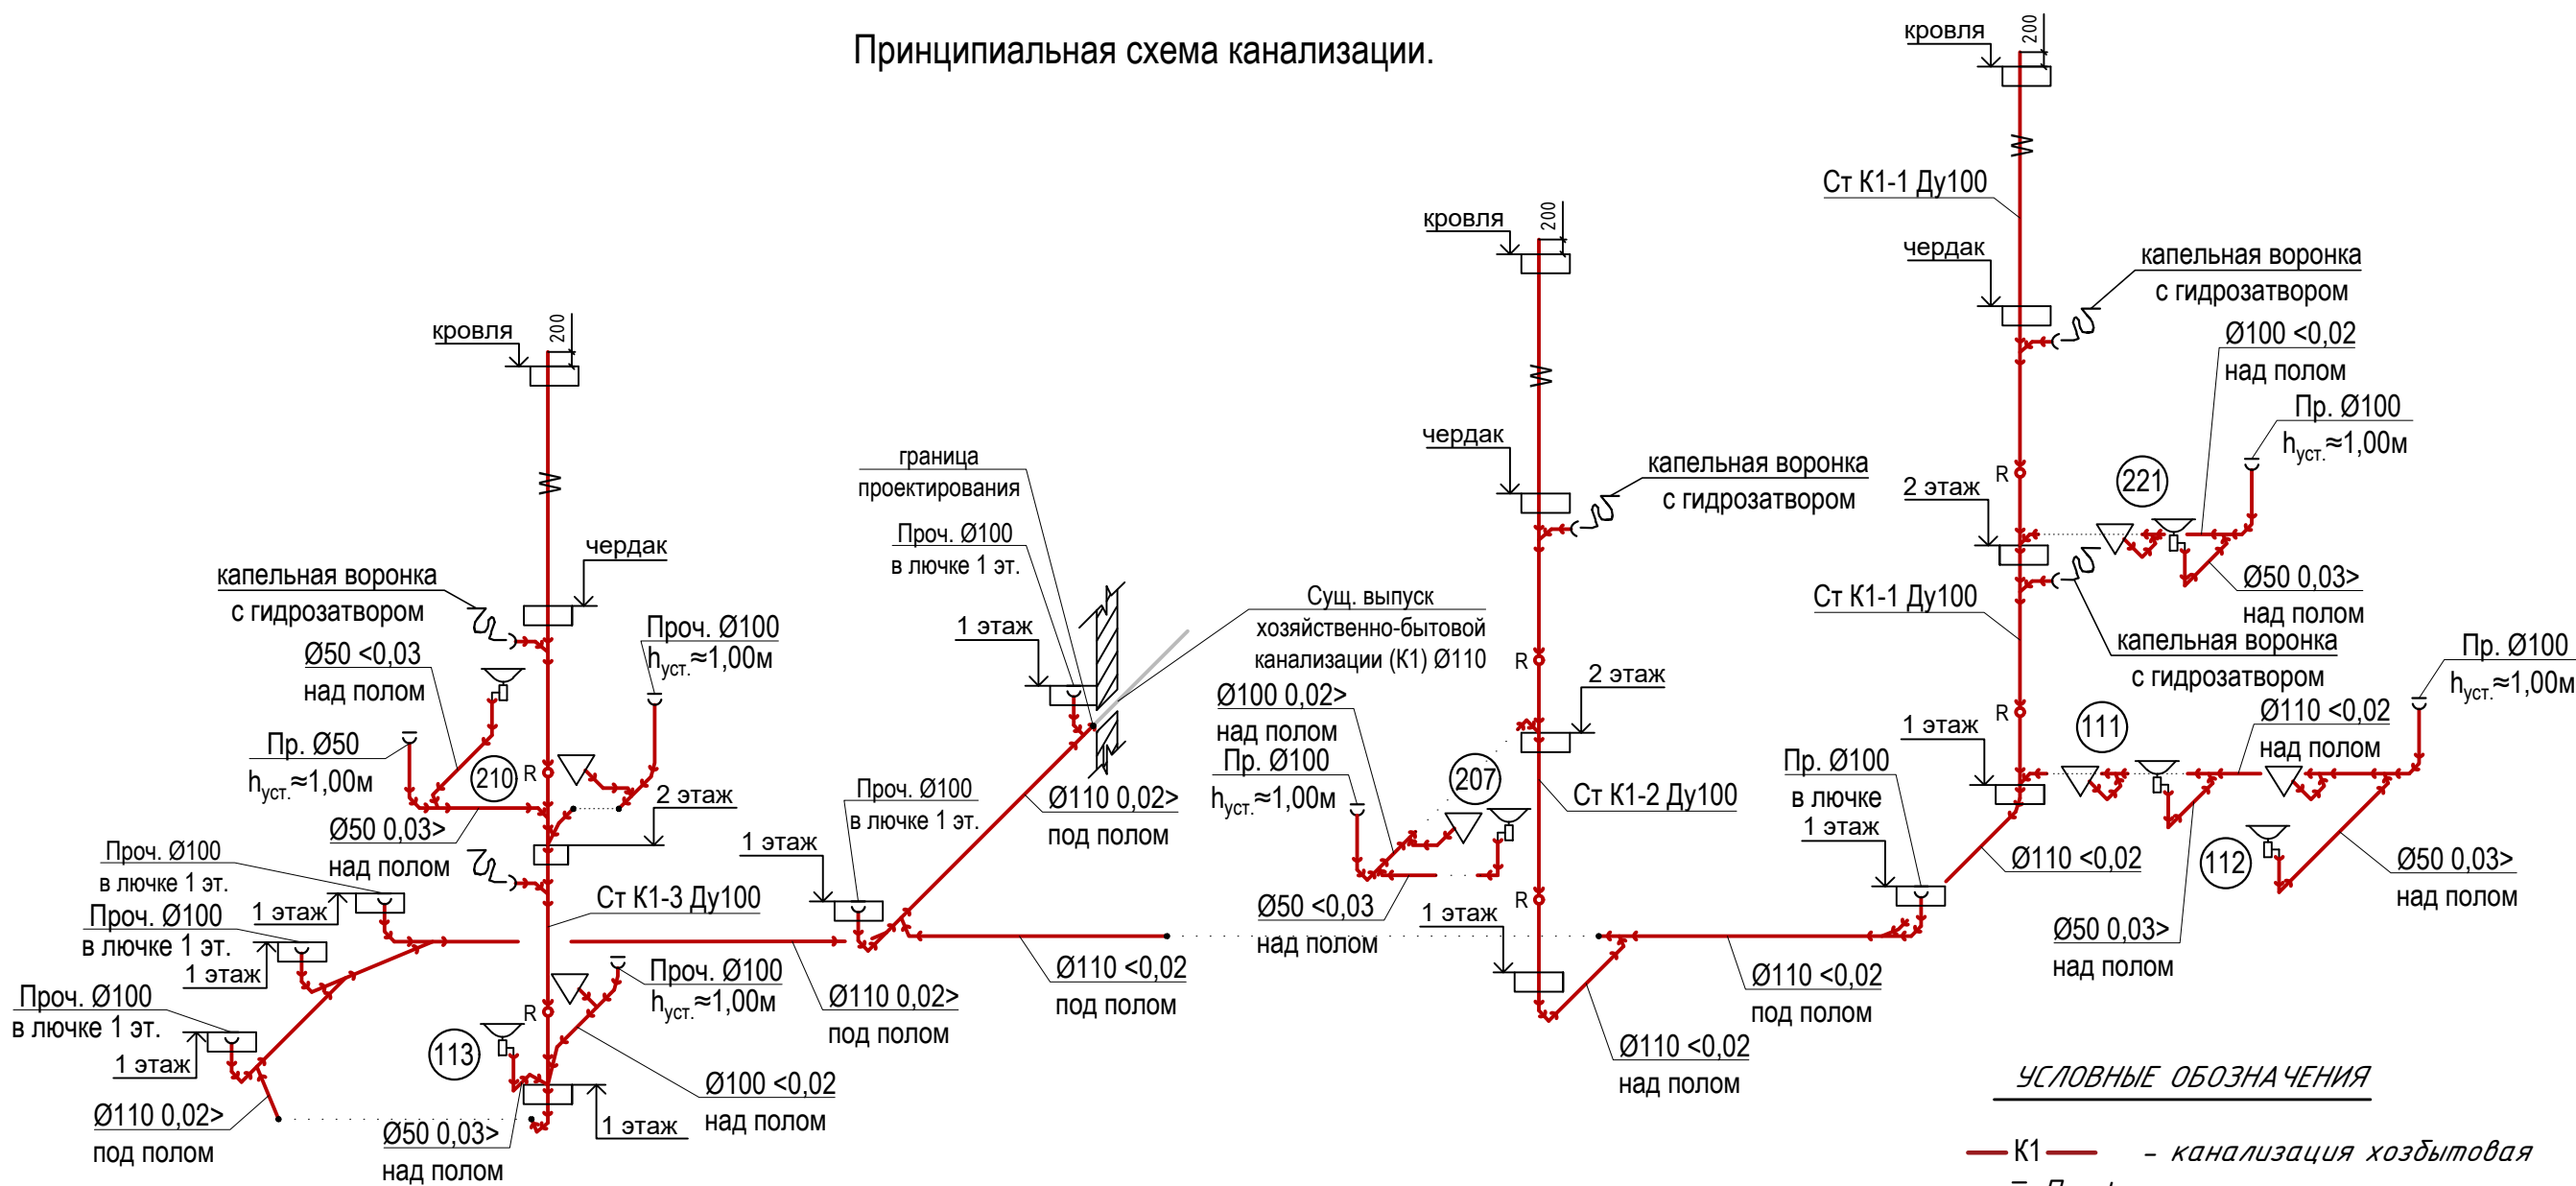


УСЛОВНЫЕ ОБОЗНАЧЕНИЯ

- K1 — канализация хозяйственная
- ↓ Пр. ф — прочистка на сети
- ⌘ R — ревизия
- φ, L, i — диаметр, длина, уклон
- ▽ — унитаз
- ▽ — умывальник

ПРИМЕЧАНИЯ:

1. Монтаж канализации вести косыми фасонными частями (тройниками, крестовинами, отводами).

Монтаж противопожарной манжеты  
(ТУ 5728-002-58088301-2005)

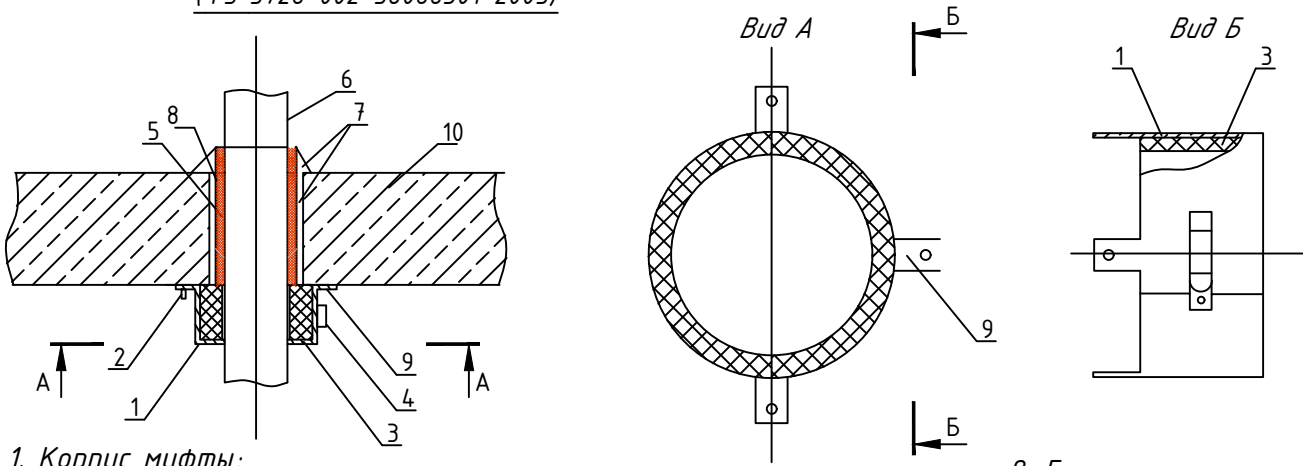

- 1. Корпус муфты;
- 2. Крепежный элемент (Дюбель/саморез);
- 3. Вкладыш из резиноподобного терморасширяющегося материала;
- 4. Замок-стяжка;
- 5. Негорючий утеплитель толщиной 30мм с фольгированным покрытием;
- 6. Труба;
- 7. Заделка цементным раствором на всю толщину перекрытия;
- 8. Гильза стальная
- 9. Лепестки для крепления муфты
- 10. Перекрытие железобетонное

|              |                  |      |        |          |         |                                                                            |   |      |        |
|--------------|------------------|------|--------|----------|---------|----------------------------------------------------------------------------|---|------|--------|
|              |                  |      |        |          |         | 2025-00224-01-1-ИОСЗ                                                       |   |      |        |
|              |                  |      |        |          |         | Капитальный ремонт здания по адресу г. Москва, ул. Мясницкая, д.44, стр.1. |   |      |        |
| Изм.         | Кол.уч.          | Лист | № док. | Подпись  | Дата    | Капитальный ремонт                                                         | Стадия   | Лист | Листов |
| Разработал   | Герасименко Н.С. |      |        | Нерас    | 12.2025 |                                                                            | П   | 5    |        |
|              |                  |      |        |          |         |                                                                            |   |      |        |
|              |                  |      |        |          |         | Принципиальная схема канализации                                           |  МОСЖИЛ<br>НИИПРОЕКТ |      |        |
| Н. контроль  | Миляева О.А.     |      |        | Миляева  | 12.2025 |                                                                            |   |      |        |
| Нач. ОПИС №1 | Белюсова Д.П.    |      |        | Белюсова | 12.2025 |                                                                            |   |      |        |

|                |  |
|----------------|--|
| Взам. инв. №   |  |
| Подпись и дата |  |
| Инв. №подл.    |  |

| Позиция                               | Наименование и техническая характеристика                                                     | Тип, марка, обозначение документа, опросного листа | Код оборудования, изделия, материала | Завод-изготовитель  | Единица измерения                                        | Количество  | Масса единицы, кг | Примечание |
|---------------------------------------|-----------------------------------------------------------------------------------------------|----------------------------------------------------|--------------------------------------|---------------------|----------------------------------------------------------|-------------|-------------------|------------|
| 1                                     | 2                                                                                             | 3                                                  | 4                                    | 5                   | 6                                                        | 7           | 8                 | 9          |
| Канализация хозяйственно-бытовая (К1) |                                                                                               |                                                    |                                      |                     |                                                          |             |                   |            |
| 1                                     | Трубы чугунные канализационные раструбные ТЧК-100-2000 Ø=100                                  | ГОСТ 6942-98                                       |                                      | Россия              | пм.                                                      | 50,0        |                   |            |
|                                       | с учетом фасонных частей                                                                      |                                                    |                                      |                     |                                                          |             |                   |            |
| 2                                     | Прочистка чуг. в лючке ф100                                                                   | ГОСТ 6942-98                                       |                                      | Россия              | шт.                                                      | 6           |                   |            |
|                                       |                                                                                               |                                                    |                                      |                     |                                                          |             |                   |            |
| 3                                     | Врезка Ø=100/100                                                                              |                                                    |                                      |                     | мест                                                     | 1           |                   |            |
| 4                                     | Трубопровод из раструбных канализационных труб марки ПВХ в комплекте с фасонными частями Ø110 | ТУ 6-19-307-86                                     |                                      | производство Россия | м.                                                       | 62,0        |                   |            |
| 5                                     | Трубопровод из раструбных канализационных труб марки ПВХ в комплекте с фасонными частями Ø50  | ТУ 6-19-307-86                                     |                                      | производство Россия | м.                                                       | 17,0        |                   |            |
| 6                                     | Прочистки ПВХ Ø 110                                                                           | ТУ 6-19-307-86                                     |                                      | производство Россия | шт.                                                      | 5           |                   |            |
| 7                                     | Прочистки ПВХ Ø 50                                                                            | ТУ 6-19-307-86                                     |                                      | производство Россия | шт.                                                      | 1           |                   |            |
| 8                                     | Ревизия ПВХ с крышкой Ø110                                                                    |                                                    |                                      | производство Россия | шт.                                                      | 6           |                   |            |
|                                       |                                                                                               |                                                    |                                      |                     |                                                          |             |                   |            |
| 9                                     | Противопожарная муфта типа "ОГРАКС-ПМ" Ø50                                                    | ТУ 5285-027-13267785-04                            |                                      | производство Россия | шт.                                                      | 3           |                   |            |
| 10                                    | Противопожарная муфта типа "ОГРАКС-ПМ" Ø110                                                   | ТУ 5285-027-13267785-04                            |                                      | производство Россия | шт.                                                      | 12          |                   |            |
|                                       |                                                                                               |                                                    |                                      |                     |                                                          |             |                   |            |
| 11                                    | Крепление трубопровода Ø100                                                                   |                                                    |                                      |                     |                                                          |             |                   |            |
|                                       | хомуты Ø100 с резиновой прокладкой                                                            |                                                    |                                      |                     | шт.                                                      | 75          |                   |            |
|                                       | анкерные болты М12 длиной 100мм с гайками                                                     |                                                    |                                      |                     | шт.                                                      | 150         |                   |            |
| 12                                    | Крепление трубопровода Ø50                                                                    |                                                    |                                      |                     |                                                          |             |                   |            |
|                                       | хомуты Ø50 с резиновой прокладкой                                                             |                                                    |                                      |                     | шт.                                                      | 23          |                   |            |
|                                       | анкерные болты М12 длиной 100мм с гайками                                                     |                                                    |                                      |                     | шт.                                                      | 46          |                   |            |
|                                       |                                                                                               |                                                    |                                      |                     |                                                          |             |                   |            |
| 13                                    | Промывка сети и гидравлическое испытание                                                      |                                                    |                                      |                     | м.                                                       | 129,0       |                   |            |
| 14                                    | Промывка сущ. выпусков канализации Ø100 гидродинамическим способом                            |                                                    |                                      |                     | м.                                                       | 10,0        |                   |            |
| 15                                    | Изоляция трубопроводов ф100 по чердаку «Энергофлекс» толщиной 13мм                            |                                                    |                                      |                     | м                                                        | 15,0        |                   |            |
|                                       |                                                                                               |                                                    |                                      |                     |                                                          |             |                   |            |
|                                       |                                                                                               |                                                    |                                      |                     | 2025-00224-01-1-ИОС3.СО                                  |             |                   |            |
|                                       |                                                                                               |                                                    |                                      |                     | Здание по адресу: г. Москва, ул. Мясницкая, д.44, стр.1. |             |                   |            |
|                                       |                                                                                               |                                                    |                                      | Изм.                | Кол.уч                                                   | Лист        | Ндок              | Подпись    |
|                                       |                                                                                               |                                                    |                                      |                     |                                                          |             |                   | Дата       |
|                                       |                                                                                               |                                                    |                                      |                     |                                                          |             |                   |            |
|                                       |                                                                                               |                                                    |                                      | Разработал          |                                                          | Герасименко |                   | 12.25      |
|                                       |                                                                                               |                                                    |                                      |                     |                                                          |             |                   |            |
|                                       |                                                                                               |                                                    |                                      |                     |                                                          |             |                   |            |
|                                       |                                                                                               |                                                    |                                      | Н.Контр.            |                                                          | Миляева     |                   | 12.25      |
|                                       |                                                                                               |                                                    |                                      | Нач.отд.№1          |                                                          | Белоусова   |                   | 12.25      |
|                                       |                                                                                               |                                                    |                                      |                     |                                                          |             |                   |            |
|              |                |              |
|--------------|----------------|--------------|
| Изм. № подл. | Подпись и дата | Взам. инв. № |
|              |                |              |

| Позиция                            | Наименование и техническая характеристика   | Тип, марка, обозначение документа, опросного листа | Код оборудования, изделия, материала | Завод-изготовитель  | Единица измерения | Количество              | Масса единицы, кг | Примечание |
|------------------------------------|---|----------------------------------------------------|--------------------------------------|---------------------|-------------------|-------------------------|-------------------|------------|
| 1                                  | 2   | 3                                                  | 4                                    | 5                   | 6                 | 7                       | 8                 | 9          |
| САНИТАРНО-ТЕХНИЧЕСКОЕ ОБОРУДОВАНИЕ |   |                                                    |                                      |                     |                   |                         |                   |            |
| 1                                  | Безободковый подвесной унитаз (с крышкой-сиденьем с микролифтом и арматурой)<br>форма: минималистичная без выемок на внешней поверхности;<br>материал: санфарфор / керамика;<br>размер: 500±40x380±20x360±20 мм;<br>тип обода: безободковый;<br>тип установки: подвесной;<br>тип креплений для чаши: скрытый;<br>расход воды: ~2,6/4 л.                                           |                                                    |                                      | производство Россия | компл.            | 5                       |                   |            |
| 2                                  | Система инсталляции для подвесного унитаза, кнопка смыва<br>тип монтажа: в капитальную стену и пол;<br>размер: ~500±20x1130±20x300±20 мм (ШxBxГ);<br>тип управления: пневматическое;<br>режимы слива: эконом - две кнопки / "старт-стоп" - одна кнопка;<br>подвод воды: сбоку / сзади;<br>объем бачка: 9 л;<br>материал кнопки слива: пластик, цвет хром (глянцевая поверхность). |                                                    |                                      | производство Россия | компл.            | 5                       |                   |            |
| 3                                  | Унитаз безободковый для маломобильных граждан с бачком с крышкой-сидением   | Российское производство                            |                                      | Россия              | компл.            | 1                       |                   |            |
| 4                                  | Умывальник для маломобильных граждан с выпуском ВcУ и сифоном<br>Форма прямоугольная с выемкой на фронтальной поверхности   | Российское производство                            |                                      | Россия              | компл.            | 1                       |                   |            |
| 5                                  | Умывальник фаянсовый с отверстием для предотвращения перелива, в комплекте с сифоном и выпуском<br>тип монтажа: подвесная;<br>расположение смесителя: посередине;<br>гарантия: не менее 7 лет.   |                                                    |                                      | производство Россия | компл.            | 5                       |                   |            |
| 6                                  | Манжета для подключения унитазов   |                                                    |                                      |                     | шт.               | 6                       |                   |            |
| 7                                  | Гофрированные отводы для унитазов L=0,5   |                                                    |                                      |                     | шт.               | 6                       |                   |            |
| 8                                  | Капельная воронка с гидрозатвором по типу ТП-21 для отвода конденсата от кондиционеров   |                                                    |                                      | производство Россия | шт.               | 5                       |                   |            |
| 9                                  | Сифон с воронкой с разрывом струи   |                                                    |                                      |                     | шт.               | 5                       |                   |            |
|                                    |   |                                                    |                                      |                     |                   |                         |                   |            |
|                                    |   |                                                    |                                      |                     |                   | 2025-00224-01-1-ИОС3.СО |                   | Лист       |
|                                    |   |                                                    |                                      |                     |                   | 12.25                   |                   | 2          |
| Изм. К.уч. Лист Ндок Подпись Дата  |   |                                                    |                                      |                     |                   |                         |                   |            |

**9710075487-20260216-1017**

(регистрационный номер выписки)

**16.02.2026**

(дата формирования выписки)

## ВЫПИСКА

**из единого реестра сведений о членах саморегулируемых организаций в области инженерных изысканий и в области архитектурно-строительного проектирования и их обязательствах**

**Настоящая выписка содержит сведения о юридическом лице (индивидуальном предпринимателе), осуществляющем подготовку проектной документации:**

**Государственное автономное учреждение города Москвы Московский научно-исследовательский и проектный институт жилищного хозяйства «МосжилНИИпроект»**

(полное наименование юридического лица/ФИО индивидуального предпринимателя)

**1197746303204**

(основной государственный регистрационный номер)

### 1. Сведения о члене саморегулируемой организации:

|     |   |   |
|-----|---|---|
| 1.1 | Идентификационный номер налогоплательщика                                                                         | 9710075487   |
| 1.2 | Полное наименование юридического лица<br>(Фамилия Имя Отчество индивидуального предпринимателя)                   | Государственное автономное учреждение города Москвы Московский научно-исследовательский и проектный институт жилищного хозяйства «МосжилНИИпроект» |
| 1.3 | Сокращенное наименование юридического лица                                                                        | ГАУ «МосжилНИИпроект»   |
| 1.4 | Адрес юридического лица<br>Место фактического осуществления деятельности<br>(для индивидуального предпринимателя) | 107078, Россия, Москва, г. Москва, Каланчевская, 4/2, 1, -                                                                                         |
| 1.5 | Является членом саморегулируемой организации                                                                      | Ассоциация проектировщиков инженерной инфраструктуры «Инфрадизайн» (СРО-П-218-15012021)                                                            |
| 1.6 | Регистрационный номер члена саморегулируемой организации                                                          | П-218-009710075487-0095   |
| 1.7 | Дата вступления в силу решения о приеме в члены саморегулируемой организации                                      | 18.06.2021   |
| 1.8 | Дата и номер решения об исключении из членов саморегулируемой организации, основания исключения                   |   |

### 2. Сведения о наличии у члена саморегулируемой организации права осуществлять подготовку проектной документации:

|   |   |                                                                                                |
|---|---|------------------------------------------------------------------------------------------------|
| 2.1 в отношении объектов капитального строительства (кроме особо опасных, технически сложных и уникальных объектов, объектов использования атомной энергии)<br>(дата возникновения/изменения права) | 2.2 в отношении особо опасных, технически сложных и уникальных объектов капитального строительства (кроме объектов использования атомной энергии)<br>(дата возникновения/изменения права) | 2.3 в отношении объектов использования атомной энергии<br>(дата возникновения/изменения права) |
| Да, 18.06.2021   | Нет   | Нет                                                                                            |



### 3. Компенсационный фонд возмещения вреда

|     |   |                                                                          |
|-----|---|--------------------------------------------------------------------------|
| 3.1 | Уровень ответственности члена саморегулируемой организации по обязательствам по договору подряда на подготовку проектной документации, в соответствии с которым указанным членом внесен взнос в компенсационный фонд возмещения вреда | Третий уровень ответственности<br>(не превышает триста миллионов рублей) |
| 3.2 | Сведения о приостановлении / прекращении права осуществлять подготовку проектной документации объектов капитального строительства   |                                                                          |

### 4. Компенсационный фонд обеспечения договорных обязательств

|     |   |                                                                                   |
|-----|---|-----------------------------------------------------------------------------------|
| 4.1 | Дата, с которой член саморегулируемой организации имеет право осуществлять подготовку проектной документации по договорам подряда, заключаемым с использованием конкурентных способов заключения договоров, в соответствии с которым указанным членом внесен взнос в компенсационный фонд обеспечения договорных обязательств      | 18.06.2021                                                                        |
| 4.2 | Уровень ответственности члена саморегулируемой организации по обязательствам по договорам подряда на подготовку проектной документации, заключаемым с использованием конкурентных способов заключения договоров, в соответствии с которым указанным членом внесен взнос в компенсационный фонд обеспечения договорных обязательств | Четвертый уровень ответственности<br>(составляет триста миллионов рублей и более) |
| 4.3 | Дата уплаты дополнительного взноса   | Нет                                                                               |
| 4.4 | Сведения о приостановлении / прекращении права осуществлять подготовку проектной документации по договорам подряда, заключаемым с использованием конкурентных способов заключения договоров   |                                                                                   |

### 5. Фактический совокупный размер обязательств

|     |   |                |
|-----|---|----------------|
| 5.1 | Фактический совокупный размер обязательств по договорам подряда на подготовку проектной документации, заключаемым с использованием конкурентных способов заключения договоров на дату выдачи выписки | 399883177 руб. |
|-----|---|----------------|



ДОКУМЕНТ ПОДПИСАН УСИЛЕННОЙ КВАЛИФИЦИРОВАННОЙ  
ЭЛЕКТРОННОЙ ПОДПИСЬЮ

Владелец: «НАЦИОНАЛЬНОЕ ОБЪЕДИНЕНИЕ ИЗЫСКАТЕЛЕЙ И  
ПРОЕКТИРОВЩИКОВ» «НОПРИЗ»

129090, г. Москва, пр-т Мира, 3, стр.3

СЕРТИФИКАТ 02 A9 64 C2 00 16 B3 DD A0 42 4E 1C 7B 48 A1 7E 77

ДЕЙСТВИТЕЛЕН: с 10.07.2025 по 10.10.2026



**9710075487-20260216-1016**

(регистрационный номер выписки)

**16.02.2026**

(дата формирования выписки)

## ВЫПИСКА

**из единого реестра сведений о членах саморегулируемых организаций в области инженерных изысканий и в области архитектурно-строительного проектирования и их обязательствах**

**Настоящая выписка содержит сведения о юридическом лице (индивидуальном предпринимателе), выполняющем инженерные изыскания:**

**Государственное автономное учреждение города Москвы Московский научно-исследовательский и проектный институт жилищного хозяйства "МосжилНИИпроект"**

(полное наименование юридического лица/ФИО индивидуального предпринимателя)

**1197746303204**

(основной государственный регистрационный номер)

### 1. Сведения о члене саморегулируемой организации:

|     |   |   |
|-----|---|---|
| 1.1 | Идентификационный номер налогоплательщика                                                                         | 9710075487   |
| 1.2 | Полное наименование юридического лица<br>(Фамилия Имя Отчество индивидуального предпринимателя)                   | Государственное автономное учреждение города Москвы Московский научно-исследовательский и проектный институт жилищного хозяйства "МосжилНИИпроект"            |
| 1.3 | Сокращенное наименование юридического лица                                                                        | ГАУ "МосжилНИИпроект"   |
| 1.4 | Адрес юридического лица<br>Место фактического осуществления деятельности<br>(для индивидуального предпринимателя) | 107078, Россия, Москва, вн.тер.г. муниципальный округ Красносельский, ул. Каланчевская, д. 4/2, стр. 1                                                        |
| 1.5 | Является членом саморегулируемой организации                                                                      | Ассоциация саморегулируемая организация «Центральное объединение организаций по инженерным изысканиям для строительства «Центризыскания» (СРО-И-003-14092009) |
| 1.6 | Регистрационный номер члена саморегулируемой организации                                                          | И-003-009710075487-0097   |
| 1.7 | Дата вступления в силу решения о приеме в члены саморегулируемой организации                                      | 14.10.2009   |
| 1.8 | Дата и номер решения об исключении из членов саморегулируемой организации, основания исключения                   |   |

### 2. Сведения о наличии у члена саморегулируемой организации права выполнять инженерные изыскания:

|   |   |                                                                                                |
|---|---|------------------------------------------------------------------------------------------------|
| 2.1 в отношении объектов капитального строительства (кроме особо опасных, технически сложных и уникальных объектов, объектов использования атомной энергии)<br>(дата возникновения/изменения права) | 2.2 в отношении особо опасных, технически сложных и уникальных объектов капитального строительства (кроме объектов использования атомной энергии)<br>(дата возникновения/изменения права) | 2.3 в отношении объектов использования атомной энергии<br>(дата возникновения/изменения права) |
| Да, 14.10.2009   | Да, 28.06.2023   | Нет                                                                                            |



### 3. Компенсационный фонд возмещения вреда

|     |   |                                                                          |
|-----|---|--------------------------------------------------------------------------|
| 3.1 | Уровень ответственности члена саморегулируемой организации по обязательствам по договору подряда на выполнение инженерных изысканий, в соответствии с которым указанным членом внесен взнос в компенсационный фонд возмещения вреда | Третий уровень ответственности<br>(не превышает триста миллионов рублей) |
| 3.2 | Сведения о приостановлении права выполнять инженерные изыскания объектов капитального строительства   |                                                                          |

### 4. Компенсационный фонд обеспечения договорных обязательств

|     |   |                                                                          |
|-----|---|--------------------------------------------------------------------------|
| 4.1 | Дата, с которой член саморегулируемой организации имеет право выполнять инженерные изыскания по договорам подряда, заключаемым с использованием конкурентных способов заключения договоров, в соответствии с которым указанным членом внесен взнос в компенсационный фонд обеспечения договорных обязательств                    | 01.07.2017                                                               |
| 4.2 | Уровень ответственности члена саморегулируемой организации по обязательствам по договорам подряда на выполнение инженерных изысканий, заключаемым с использованием конкурентных способов заключения договоров, в соответствии с которым указанным членом внесен взнос в компенсационный фонд обеспечения договорных обязательств | Третий уровень ответственности<br>(не превышает триста миллионов рублей) |
| 4.3 | Дата уплаты дополнительного взноса   | 07.03.2019                                                               |
| 4.4 | Сведения о приостановлении права выполнять инженерные изыскания по договорам подряда, заключаемым с использованием конкурентных способов заключения договоров   |                                                                          |

### 5. Фактический совокупный размер обязательств

|     |   |                 |
|-----|---|-----------------|
| 5.1 | Фактический совокупный размер обязательств по договорам подряда на выполнение инженерных изысканий, заключаемым с использованием конкурентных способов заключения договоров на дату выдачи выписки | 7736457.93 руб. |
|-----|---|-----------------|



ДОКУМЕНТ ПОДПИСАН УСИЛЕННОЙ КВАЛИФИЦИРОВАННОЙ  
ЭЛЕКТРОННОЙ ПОДПИСЬЮ

Владелец: «НАЦИОНАЛЬНОЕ ОБЪЕДИНЕНИЕ ИЗЫСКАТЕЛЕЙ И  
ПРОЕКТИРОВЩИКОВ» «НОПРИЗ»

129090, г. Москва, пр-т Мира, 3, стр.3

СЕРТИФИКАТ 02 A9 64 C2 00 16 B3 DD A0 42 4E 1C 7B 48 A1 7E 77

ДЕЙСТВИТЕЛЕН: с 10.07.2025 по 10.10.2026

