



Департамент капитального ремонта города Москвы Государственное автономное учреждение города Москвы Московский научно-исследовательский и проектный институт жилищного хозяйства «МосжилНИИпроект» (ГАУ «МосжилНИИпроект»)

mgnp@mgnp.mos.ru +7 495 624 40 65 107078, г. Москва, Каланчевская, д. 4/2, стр. 1

Арх.№

**Капитальный ремонт здания,
расположенного по адресу:
г. Москва, ул. Мясницкая д.44, стр.1**

ПРОЕКТНАЯ ДОКУМЕНТАЦИЯ

Раздел 5

**Сведения об инженерном оборудовании, о сетях и
системам инженерно- технического обеспечения.**

Подраздел 5 «Сети связи»

Часть 7. Система контроля и управления доступом

2025-00224-01-0-ИОС5.7

Том 5.5.7

I Этап

Москва 2026г.



Департамент капитального ремонта города Москвы Государственное автономное учреждение города Москвы Московский научно-исследовательский и проектный институт жилищного хозяйства «МосжилНИИпроект» (ГАУ «МосжилНИИпроект»)

mgnp@mgnp.mos.ru +7 495 624 40 65 107078, г. Москва, Каланчевская, д. 4/2, стр. 1

Капитальный ремонт здания,

**расположенного по адресу:
г. Москва, ул. Мясницкая д.44, стр.1**

ПРОЕКТНАЯ ДОКУМЕНТАЦИЯ

Раздел 5

**Сведения об инженерном оборудовании, о сетях и
системах инженерно- технического обеспечения.**

Подраздел 5 «Сети связи»

Часть 7. Система контроля и управления доступом.


2025-00224-01-0-ИОС5.7

Том 5.5.7

I Этап

Начальник ОПИС №1

ГИП

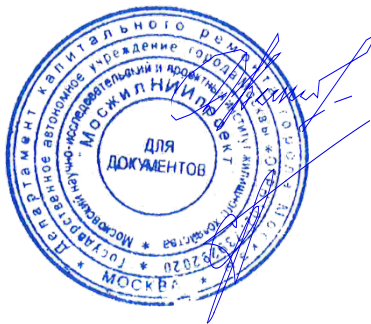

Д.П. Белоусова

08.04.2026

В.Ю. Гунченко

08.04.2026

Москва 2026г.

Содержание раздела

№п/п	Наименование проектных материалов	Марка листа	Стр.
1	Содержание раздела		2
2	Состав проектной документации		3
3	Текстовая часть		4-6
4	Принципиальная схема СКУД	ИОС5.7-1	7
5	Принципиальная схемы видеодомофона.	ИОС5.7-2	8
6	План 1-го этажа. СКУД	ИОС5.7-3	9
7	План 2-го этажа. СКУД	ИОС5.7-4	10
8	Спецификация оборудования и материалов	ИОС5.7.СО	11,12

Согласовано

Взам. Инв. №

Подп. И дата

Инв. № подл.

2025-00224-01-0-ИОС5.7

Изм.	Кол.уч	Лист	№ док.	Подп.	Дата
Разработал		Роянцева А.А			03.2026
Зав.сектора		Роянцева А.А			03.2026
Норм.контр		Роянцева А.А			03.2026
Нач.ОПИС №1		Белоусова Д.П.			03.2026

Капитальный ремонт
Здание и помещений по адресу:
г. Москва, ул. Мясницкая, д.44,
стр.1

Стадия	Лист	Листов
П	1	1



**МОСЖИЛ
НИИПРОЕКТ**

Текстовая часть.

1. Краткая характеристика объекта

Капитальный ремонт здания и помещений , расположенное по адресу: г. Москва, ул. Мясницкая, д. 44, стр.1.

Здание оборудовано центральным отоплением; холодным и горячим водоснабжением; канализацией; электроснабжением; городским телефонным вводом, который при капитальном ремонте сохраняется.

Для обеспечения устойчивого функционирования сетей связи, в том числе при чрезвычайных ситуациях, проектом выполнены мероприятия по обеспечению здания:

- городским радио-вводом;
- городским телефонным вводом;
- цифровым телевидением.

Для защиты информационных сетей применяются антивирусные программы.

2. Система контроля и управления доступом

Система контроля и управления доступом (СКУД) принадлежит к техническим средствам высокого уровня и предназначена для ограничения несанкционированного доступа в охраняемые помещения с помощью электронных идентификаторов.

Системой контроля и управления доступом оборудовать все входы в здание, в архив, в помещение ввода водопровода, в серверную, входы во все кабинеты.

Система СКУД интегрирована с системой охранно-пожарной сигнализации и имеет общую базу данных на основе системы "Рубеж" и собрана на сетевой контроллер STR20-IP который подключается на коммутатор, расположенный в телекоммуникационном шкафу. К сетевому контроллеру можно подключить до 8-ми модулей доступа "STR-1AP-M", но длина кабеля от контроллера до модуля не должна превышать 10,0м. Смотри схему на л.1 Гр.части. Каждый из модулей доступа устанавливаются на стене у контролируемой двери и подключаются к сетевому контроллеру кабелем КПСВВнг(A)HF -1х2х0.75.

Сетевые контроллеры включается в линию интерфейса и питания RS-485 кабель U/UTPнг(A) HF -4х2х0.52.

Питание контроллеров осуществляется от ИВЭПР-12 /3 3.5А.

Для каждой точки прохода предусмотрена кнопка аварийного выхода, разрывающая при нажатии цепь питания замка. Разблокировка при пожаре предусмотрена с помощью релейных модулей, подключенных к АПС (релейные модули предусмотрены в том 2025-00224-01-0-ИОС5.1). Данные модули при пожаре размыкают цепь питания замка.

Доводчики учитываются в разделе АР в комплекте с дверьми. В помещениях изнутри рядом с дверью монтируется считыватель STR-RM-A01.

Согласовано					
Взам. Инв. №					
Подп. И. дата					
Инв. № подл.					

						2025-00224-01-0-ИОС5.7		
Изм.	Кол.уч	Лист	№ док.	Подп.	Дата			
Разработал		Роянцева А.А			03.2026	Капитальный ремонт здания и помещений по адресу: . Москва, ул. Мясницкая д. 44, стр.1	Стадия	Лист
Зав.сектора		Роянцева А.А			03.2026		П	1
Норм.контр		Роянцева А.А			03.2026			Листов
Нач.ОПИС №1		Белоусова Д.П.			03.2026			З
						 МОСЖИЛ НИИПРОЕКТ		

Со стороны входа у двери монтируется считыватель электронных идентификаторов. Карточки выдаются сотрудникам учреждения. Тип алгоритма согласован с Заказчиком.

Система доступа объединена в локально вычислительную сеть с подключением к коммутаторам через патч-панели. Патч-панели, коммутаторы устанавливаются в телекоммуникационном шкафу ШТ2.1. Шкаф ШТ2.1 учтен в разделе СКС. Смотри схему на листе №1. Системы СОТС и СКУД объединяются на программном уровне на АРМ СОТС (учтен в томе 2025-00223-01-0-ИОС5.8)

По степени надежности электроснабжения сети связи относятся к 1-ой категории потребителей. Для оборудования предусмотрены источники бесперебойного питания.

Источник бесперебойного питания обеспечивает бесперебойную работу оборудования, в отсутствие электропитания 220В, от аккумуляторных батарей в течение не менее 10 минут. Переход с основного на резервное электропитание происходит автоматически при пропадании основного питания.

Защита электрических цепей должна быть выполнена в соответствии с ПУЭ.

Защитное заземление электрооборудования, металлических каркасов и конструкций следует выполнить в соответствии с ПУЭ и технической документацией на оборудование

3.Видеодомофон.

У дверей главного и запасного входа на стене здания устанавливаются вызывные панели DS06-AP IP видеодомофона SM-400W на 2 вызывные2 панели. Монитор видеодомофона устанавливается на посту охраны, пом. №101А. Видеодомофоны являются одним из вариантов решения для организации системы контроля и управления доступом, состоящей из видеомонитора с вызывной панелью. Проход осуществляется с помощью поднесения идентификатора, кнопки выхода и через монитор видеодомофона.

Видеомонитор предназначен для просмотра изображения от внешней видеокамеры (вызывной панели) и звукового вызова при входе посетителя и состоит из переговорной трубки с динамиком и монитора 4.3", индикатором питания, кнопками "монитор", вызова и открытия двери.

Антивандальная вызывная панель имеет встроенный микрофон и динамическую головку, кнопку вызова и монохромную видеокамеру 1/3" (400ТВЛ, 0Лк) с ИК -подсветкой (60см).

Монитор видеодомофона устанавливается на стене на посту охраны, вызывные панели монтируются снаружи у входной двери. Также рядом с вызывной панелью монтируется считыватель ключей. Ключи выдаются сотрудникам учреждения.

Питание видеомонитора осуществляется от сети (100 -240В, 50/60Гц), питание вызывной панели - от видеомонитора (12В). Сеть выполняется кабелем марки КПСВВнг(А)-HF -4х2х0, 75.

Питание замка и считывателя ключа осуществляется от блока питания 12В, установленного по месту на стене поста охраны. Для точки прохода предусмотрена кнопка аварийного выхода, разрывающая при нажатии цепь питания замка. Разблокировка при пожаре предусмотрена с помощью релейного модуля, подключенного к АПС (релейные модули предусмотрены в томе 2025-00223-01-0- ИОС5.1). Данный модуль при пожаре размыкает цепь питания замка.

В соответствии с требованиями п.5.2.4 СП 2.13130.2020, места пересечения кабелей, кабеленесущих конструкций со строительными конструкциями с нормируемыми пределами огнестойкости, обеспечиваются проходками не ниже пределов огнестойкости, установленных для пересекаемых конструкций посредством установки гильз из труб с заделкой гидроизоляционной огнеупорной мастикой в соответствии с ГОСТ 30247.1, ГОСТ Р 53306, ГОСТ Р 53310.


Взам. инв. №							Лист	
Подп. и дата							2025-00224-01-0-ИОС5.7	2
Инв. № подл.	Изм.	Кол.уч	Лист	№ док	Подп.	Дата		

4. Перечень нормативных документов

- **ГОСТ Р 21.101-2020** «Система проектной документации для строительства (СПДС). Основные требования к проектной и рабочей документации». Постановление №87 от 16.02.2008 «О составе разделов проектной документации и требования к их содержанию» (с изменениями на 23 июня 2020г. ст.282-ст)
 - **СП 118.13330.2022** «Общественные здания и сооружения».
 - **ГОСТ 21.406-88** актуализация 01.01.2021 «Проводные средства связи. Обозначения условные графические на схемах и планах»
 - **РМ-2798** «Инструкция по проектированию систем связи информатизации и диспетчеризации объектов жилищного строительства»
 - **ГОСТ 53246-2025** «Информационные технологии. Системы кабельные структурированные. Проектирование основных узлов системы. Общие требования».
- ГОСТ 29099-91** дата введения **01.01.93г** «Сети вычислительные локальные. Термины и определения»
- **ГОСТ Р 21.703-2000** актуализация 01.06.2025г «Правила выполнения рабочей документации проводных систем связи».
 - **СП 76.13130-2016** дата введения 17.06.2017г «Электротехнические устройства».
 - **ПУЭ** «Правила устройства электроустановок».
 - **ГОСТ 28601.2-90** дата введения **01.01.1991г** «Система несущих конструкций серии 482,6мм. Шкафы и стоечные конструкции. Основные рекомендации».
 - **СП 134.13330.2022** «Система электросвязи зданий и сооружений. Основные положения проектирования».

Инв. № подл.	Подп. и дата	Взам. инв. №							Лист	
Изм.	Кол.уч	Лист	№ док	Подп.	Дата	2025-00224-01-0-ИОС5.7				3

Принципиальная схема СКУД

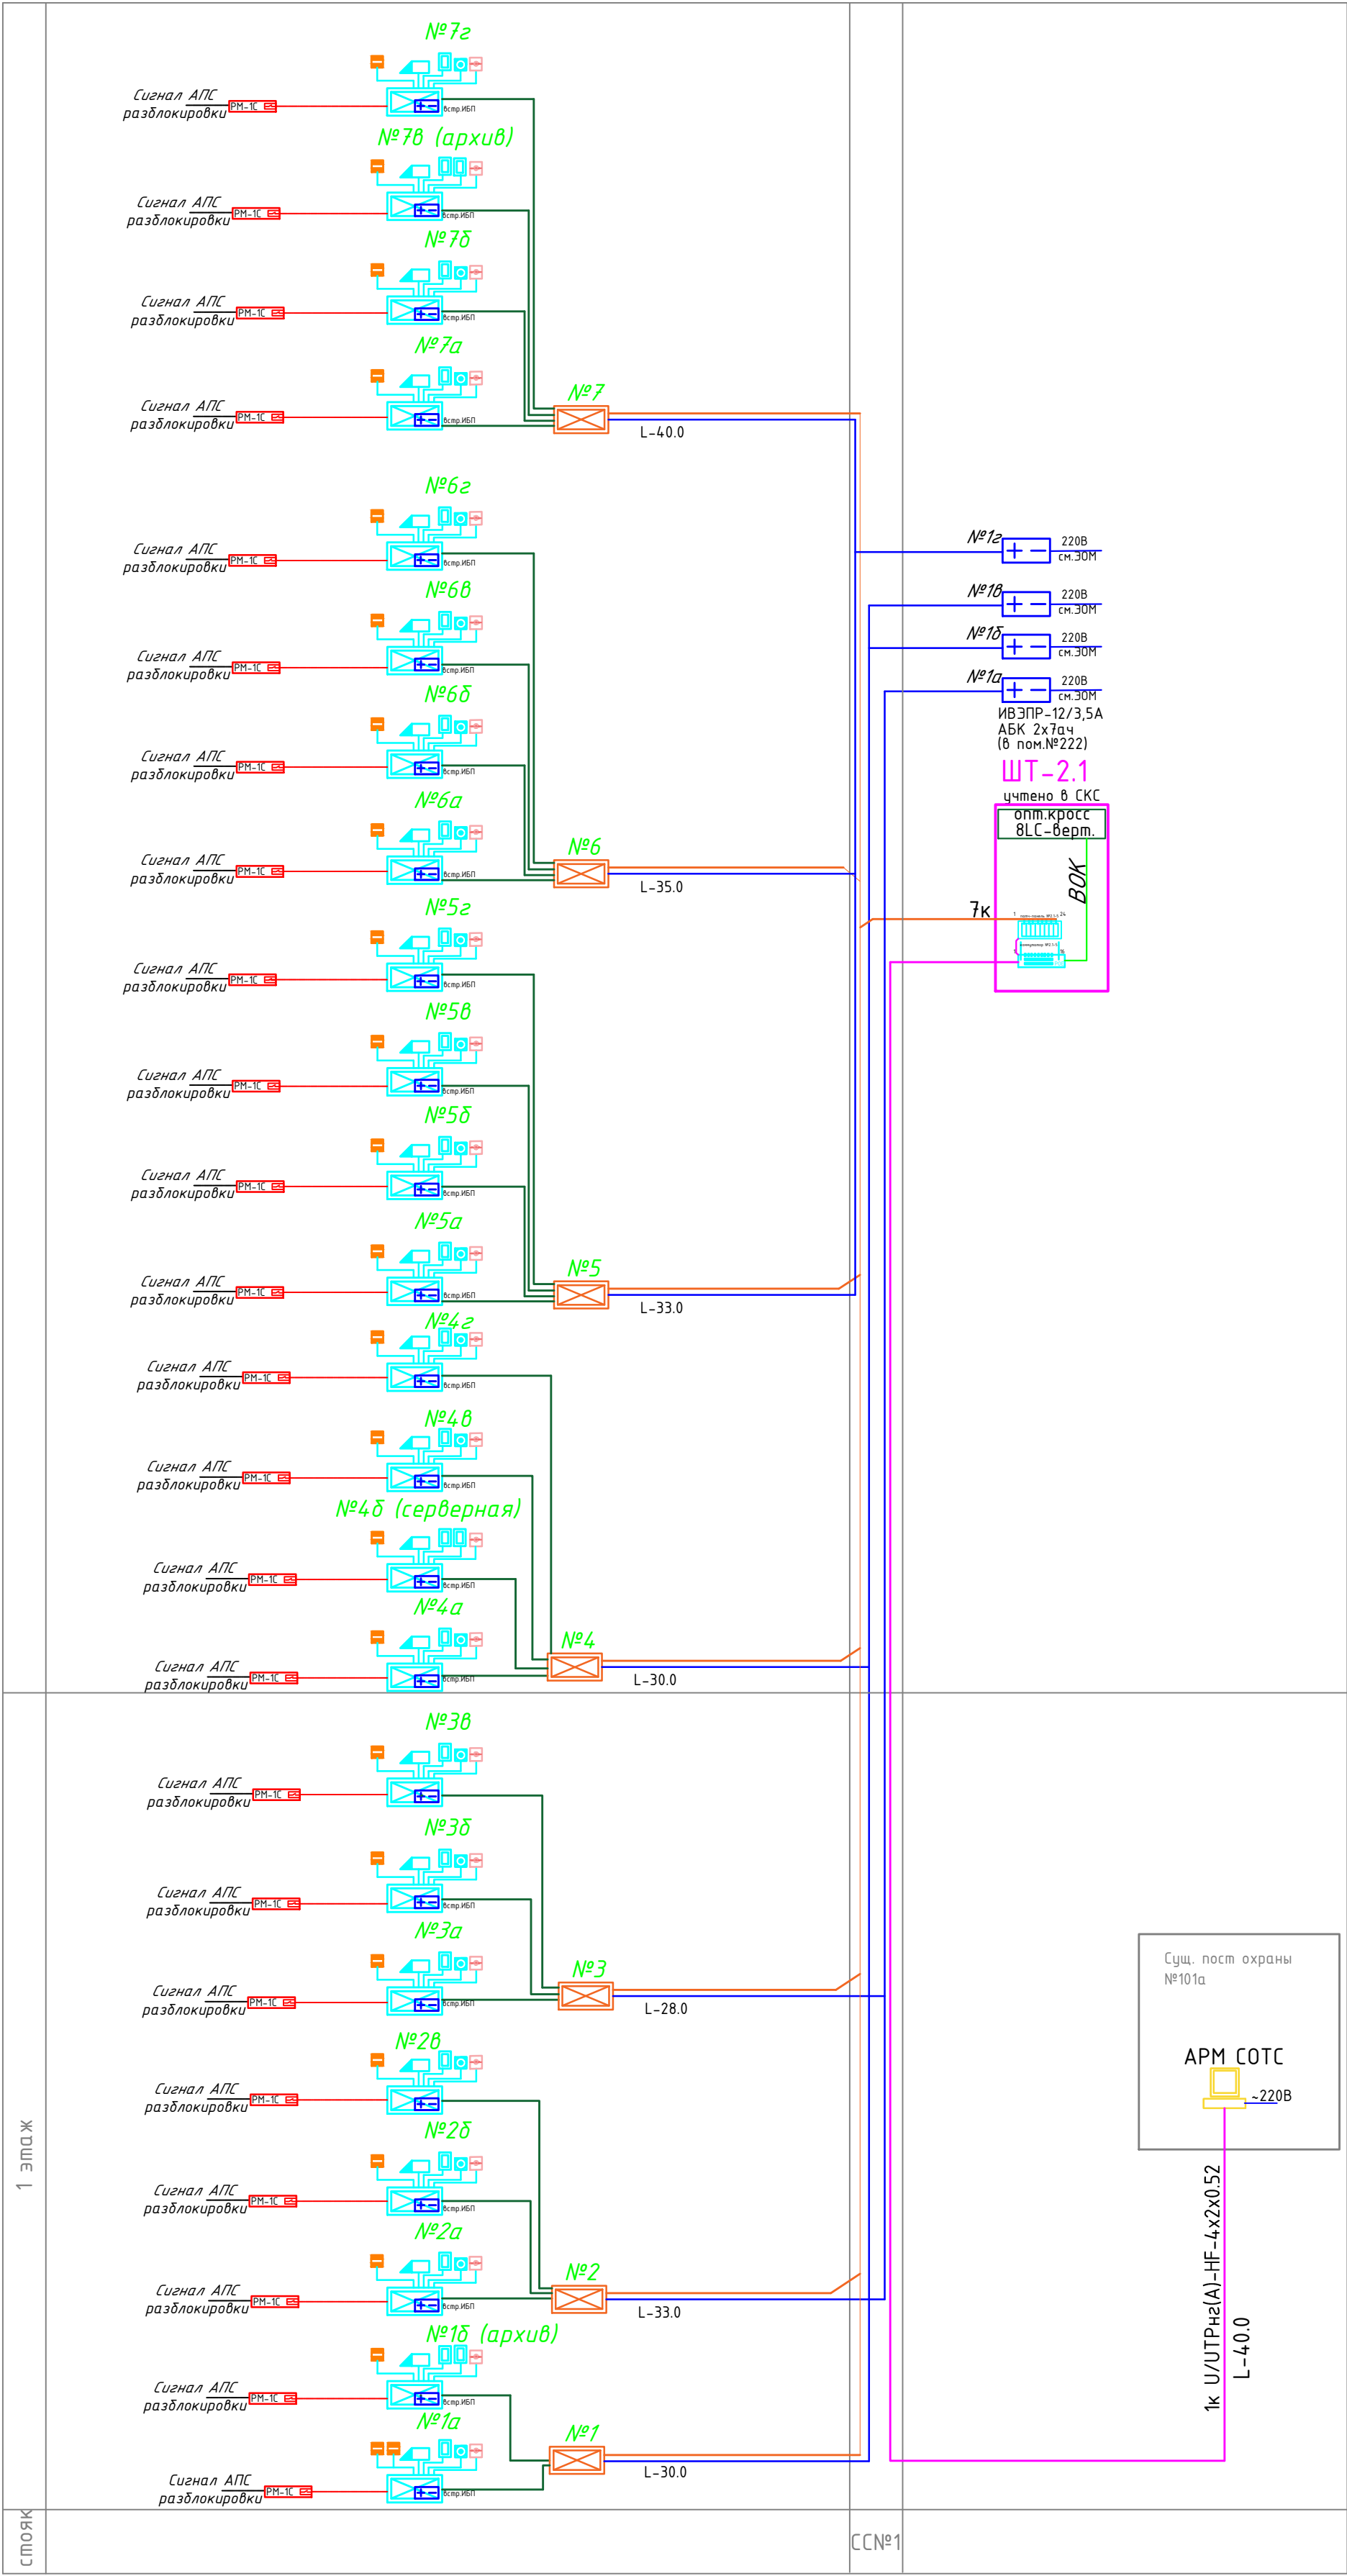


Условные обозначения

- ШТ-1.4
- П-п №8.1-1
- Шкаф телекоммуникационный 19" 42U напольный с указанием номера
- Патч - панель с указанием номера
- Коммутатор на 16 портов с PoE
- Источник электропитания 12В
- Контроллер доступа "STR20-IP"
- Модуль доступа "STR-1AP-M", встроенным ИБП
- Замок электромагнитный
- Извещатель охранной точечный магнитоконтактный
- Считыватель электронных идентификаторов
- Бесконтактная кнопка выхода
- Аварийная кнопка выхода
- Сигнал АПС разблокировки
- Релейный модуль
- Кабели:
- U/UTPнз(A)-HF-4x2x0.52
- КПСВВнз(A)-HF-1x2x0.75
- ВВГнз(A)-HF-1x2x1.5мм
- ЛОУТОКС 20нз(A)-FRHF -1x2x0.5

ПРИМЕЧАНИЯ:


1. Шкафы телекоммуникационные, оптические кроссовые панели, оптические кабели ВОК, металлические лотки учтены в части СКС-2025-00224-01-0-ИОС 5.5
2. Адресные релейные модули РМ-1С включаются в шлейф пожарной сигнализации и учтены в части АПС -2025-00224-01-0-ИОС 5.5.1.
3. Подключение к контроллерам и модулям выполняется кабелем ЛОУТОКС 20нз(A)-FRHF-1x2x0.5 и учитывается в данном томе

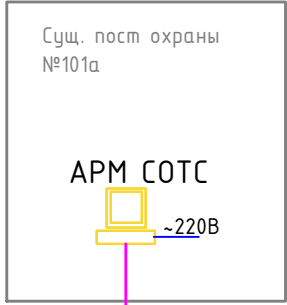

Согласовано					
Изм. №	Подпись	Дата	Взамен инв. №		
Изм. №	Подпись	Дата	Взамен инв. №		

						2025-00224-01-0-ИОС 5.7		
						Капитальный ремонт здания и помещений по адресу г. Москва, ул. Мясницкая, д.44, стр.1.		
Изм.	Кол.уч.	Лист	№ док.	Подпись	Дата	Капитальный ремонт	Стадия	Лист
Разработал	Белова Ф.И.	03.03.26					П	1
Зав.сектора	Роянцева А.А.	03.03.26						4
						Принципиальная схема СКУД		
Норм.Контр	Роянцева А.А.	03.03.26						
Нач.ОПИС	Белусова Д.П.	03.03.26						

Принципиальная схема видеодомофона

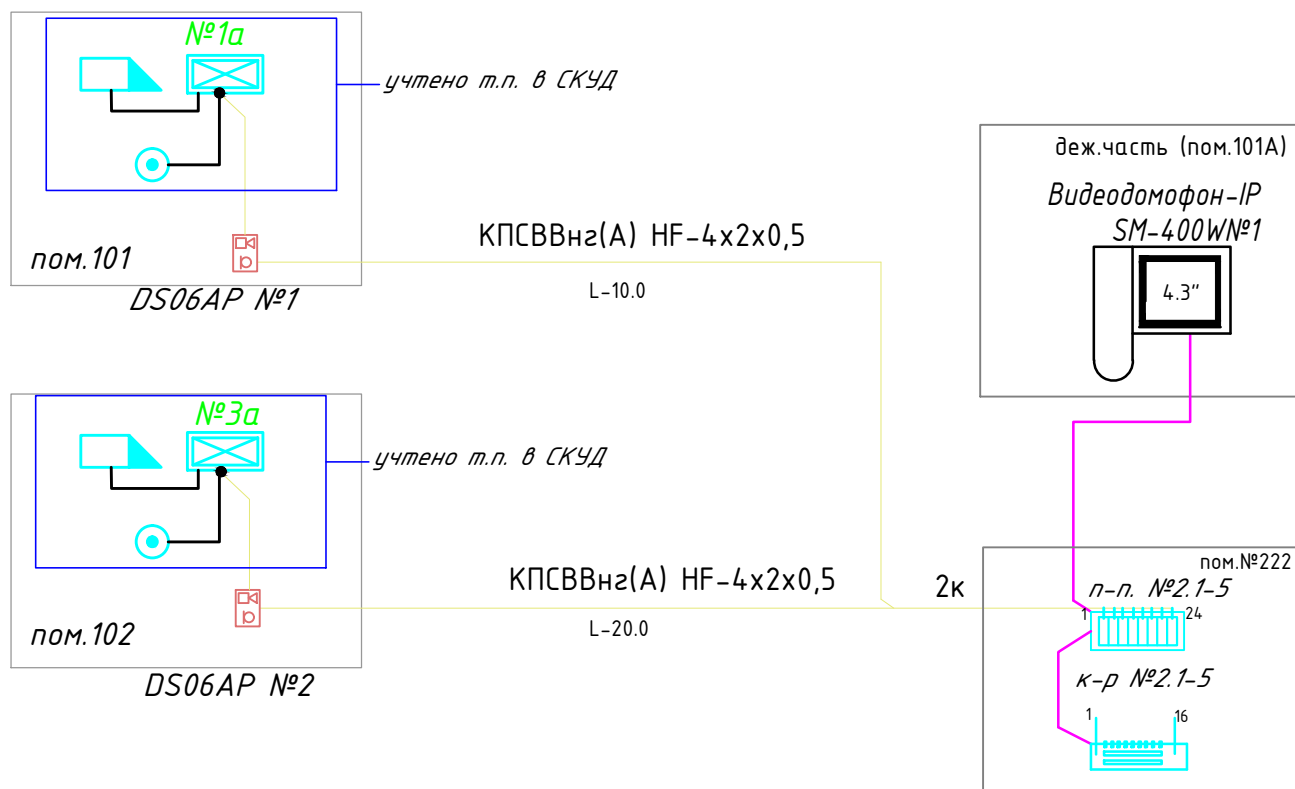


Условные обозначения



видеомонитор



вызывная панель

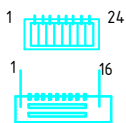

Патч-панель

Коммутатор доступа

ВВГн2(A)-HF-1x2x1.5мм

U/UTPн2(A)-HF-4x2x0.52

КПСВВн2(A)-HF-1x2x0.75

ПРИМЕЧАНИЯ:

1. Шкафы телекоммуникационные, оптические кроссовые панели, оптические кабели ВОК, металлические лотки учтены в части СКС-2025-00224-01-0-ИОС5.5

Взам. инв. №

Подпись и дата

Инв. № подл.

2025-00224-01-0-ИОС5.7

Капитальный ремонт здания и помещений по адресу г. Москва, ул Мясницкая, д.44, стр.1.

Изм.	Кол.уч.	Лист	№ док.	Подпись	Дата
Разработал	Белова Ф.И.				03.03.26
Зав.сектора	Роянцева А.А.				03.03.26
Норм.Контр	Роянцева А.А.				03.03.26
Нач.ОПИС	Белусова Д.П.				03.03.26

Капитальный ремонт


Принципиальная схема
видеодомофона

Стадия	Лист	Листов
П	2	4



МОСЖИЛ
НИИПРОЕКТ

План 1-го этажа на отм. 0.000
М 1:100

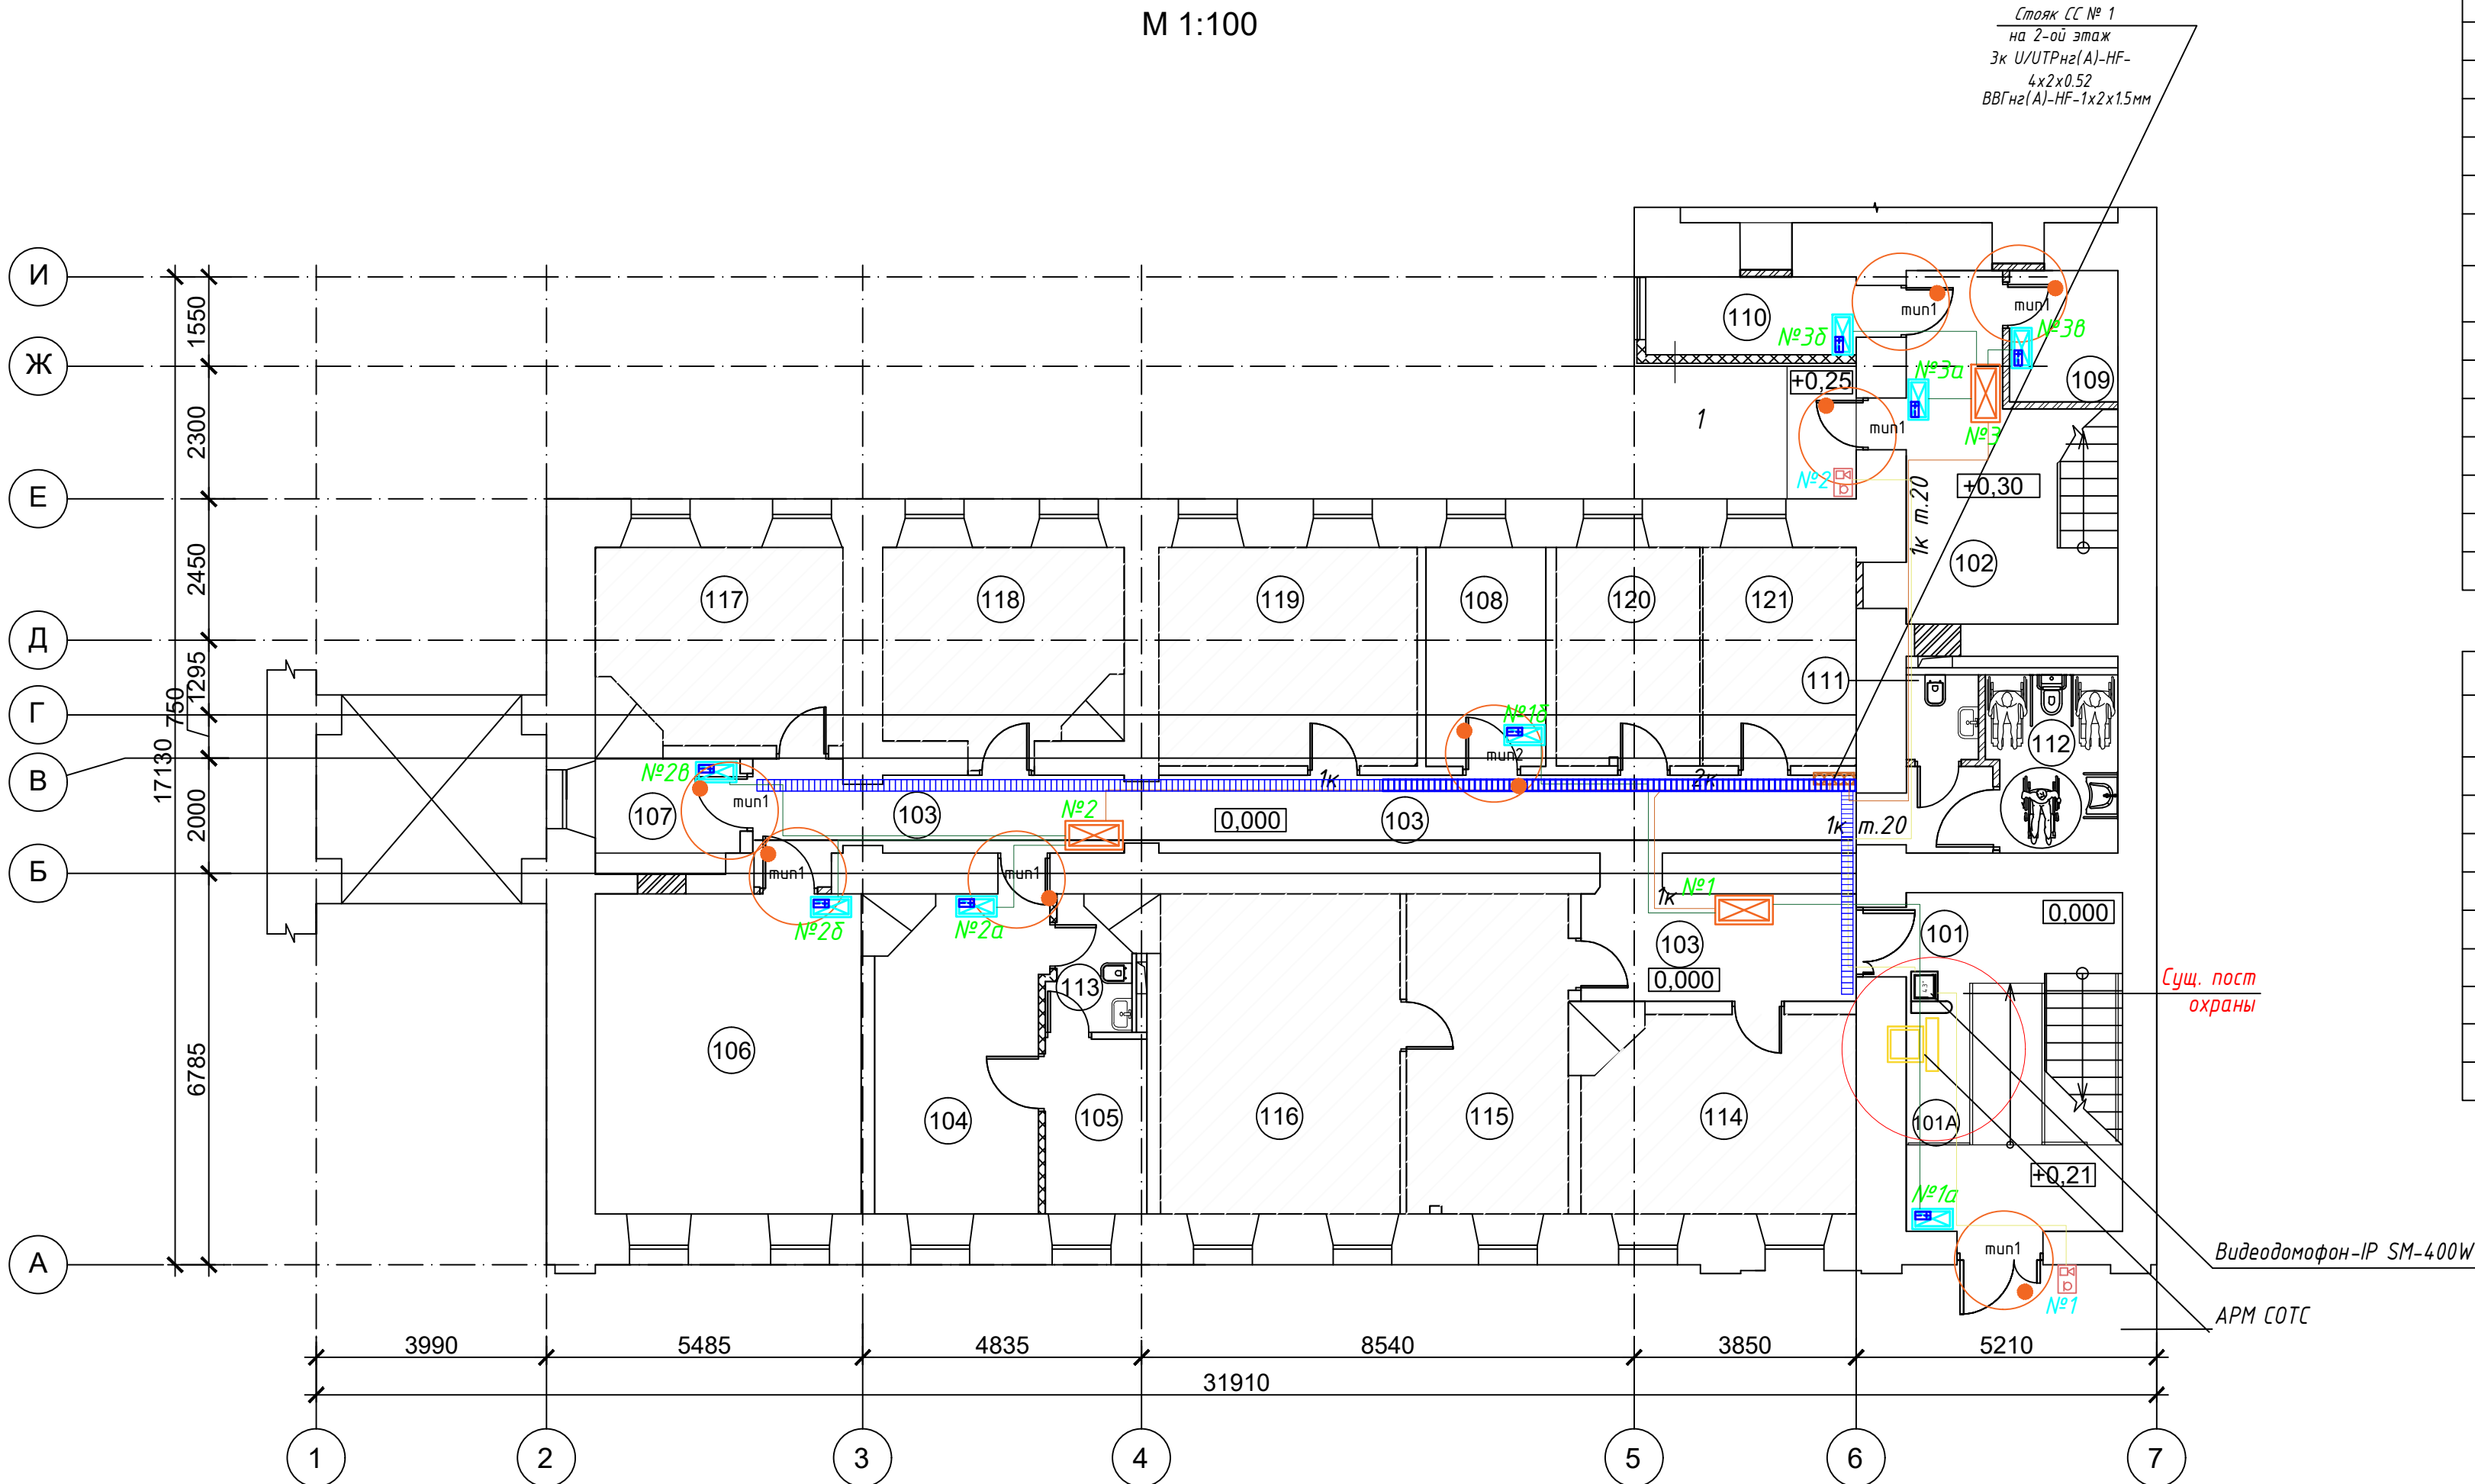

Экспликация помещений 1-го этажа				8
N п/п	Наименование помещений	Площадь м²	Кат. пом.	
101	Лестница №1 (ЛК ти 1)	22,9		
101A	Пост охраны			
102	Лестница №2 (ЛК тип 1)	17,7		
103	Коридор	39,4		
104	Кабинет заместителя прокурора	15,9		
105	Комната отдыха заместителя прокурора	5,3		
106	Кабинет помощника прокурора / прием граждан МГН	25,6		
107	Кабинет*	4,8		
108	Архив	7,9	В4	
109	Ввод водопровода	4,3		
110	Кабинет для приема граждан	4,9		
111	Санузел	1,8		
112	Санузел МГН	6,7		
113	Санузел заместителя прокурора	2,8		
ИТОГО:		160		

Помещения не входящие в зону ремонта			
N п/п	Наименование помещений	Площадь м²	Кат. пом.
114	Офисное помещение	15,7	
115	Офисное помещение	15,6	
116	Офисное помещение	23,0	
117	Офисное помещение	13,8	
118	Офисное помещение	13,8	
119	Офисное помещение	17,0	
120	Офисное помещение	9,4	
121	Офисное помещение	10,1	
ИТОГО:		118,4	

Схема расположения шкафа СС


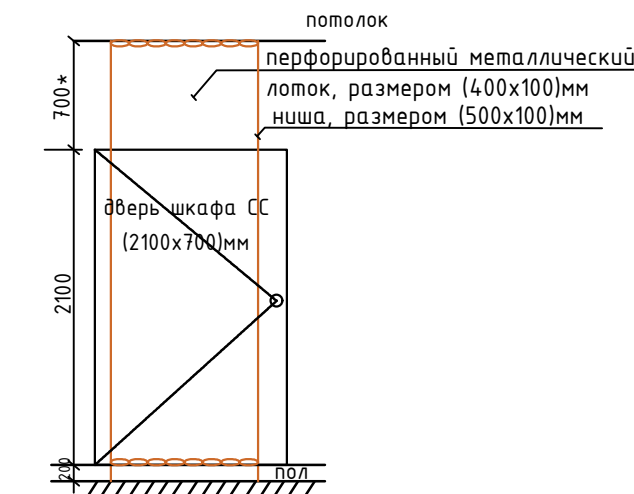


Схема расположения гильз d=50мм в перекрытиях

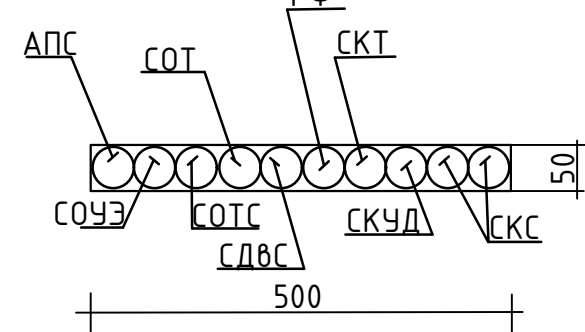

Условные обозначения

ШТ-1.4

Шкаф телекоммуникационный 19" 42U напольный с указанием номера

Патч - панель с указанием номера

Источник электропитания 12В

Контроллер доступа "STR20-IP"

Модуль доступа "STR-1AP-M", встроенным ИБП

Замок электромагнитный

Извещатель охранный точечный магнитоконтактный

Считыватель электронных идентификаторов

Бесконтактная кнопка выхода

Аварийная кнопка выхода

Релейный модуль

mun1 - односторонняя точка прохода считыватель - кнопка "Выход"

mun2 - двухсторонняя точка прохода считыватель - считыватель

Кабели:

U/UTPn2(A)-HF-4x2x0.52


U/UTPn2(A)-HF-4x2x0.52

KPCBВn2(A)-HF-1x2x0.75

ЛОУТОКС 20n2(A)-FRHF -1x2x0.5


ВВГn2(A)-HF-1x2x1.5мм

проволочный металлический лоток

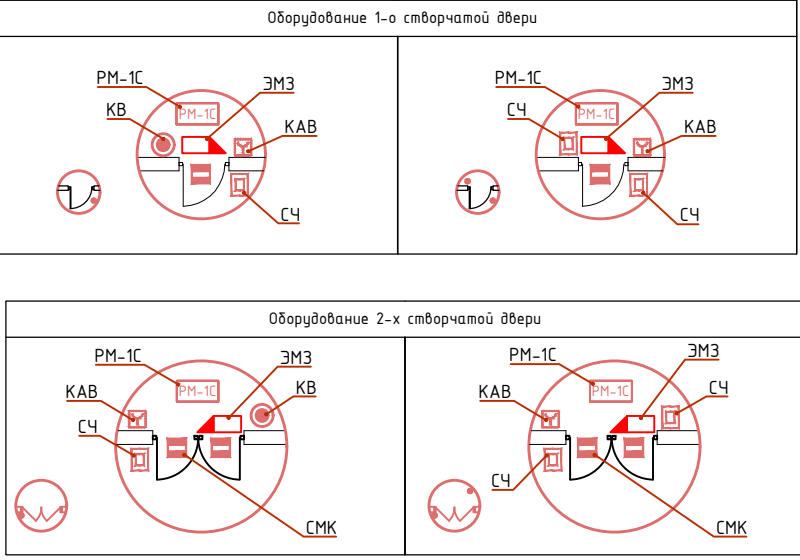

						2025-00224-01-0- ИОС.7		
						Капитальный ремонт здания и помещений по адресу г. Москва, ул. Мясницкая, д.44, стр.1.		
						Структурированные кабельные сети		
						П	3	4
						План 1-го этажа. М 1:100. Расположение оборудования и кабельных трасс СКУД.		

План 2-го этажа на отм. +3.800
М 1:100

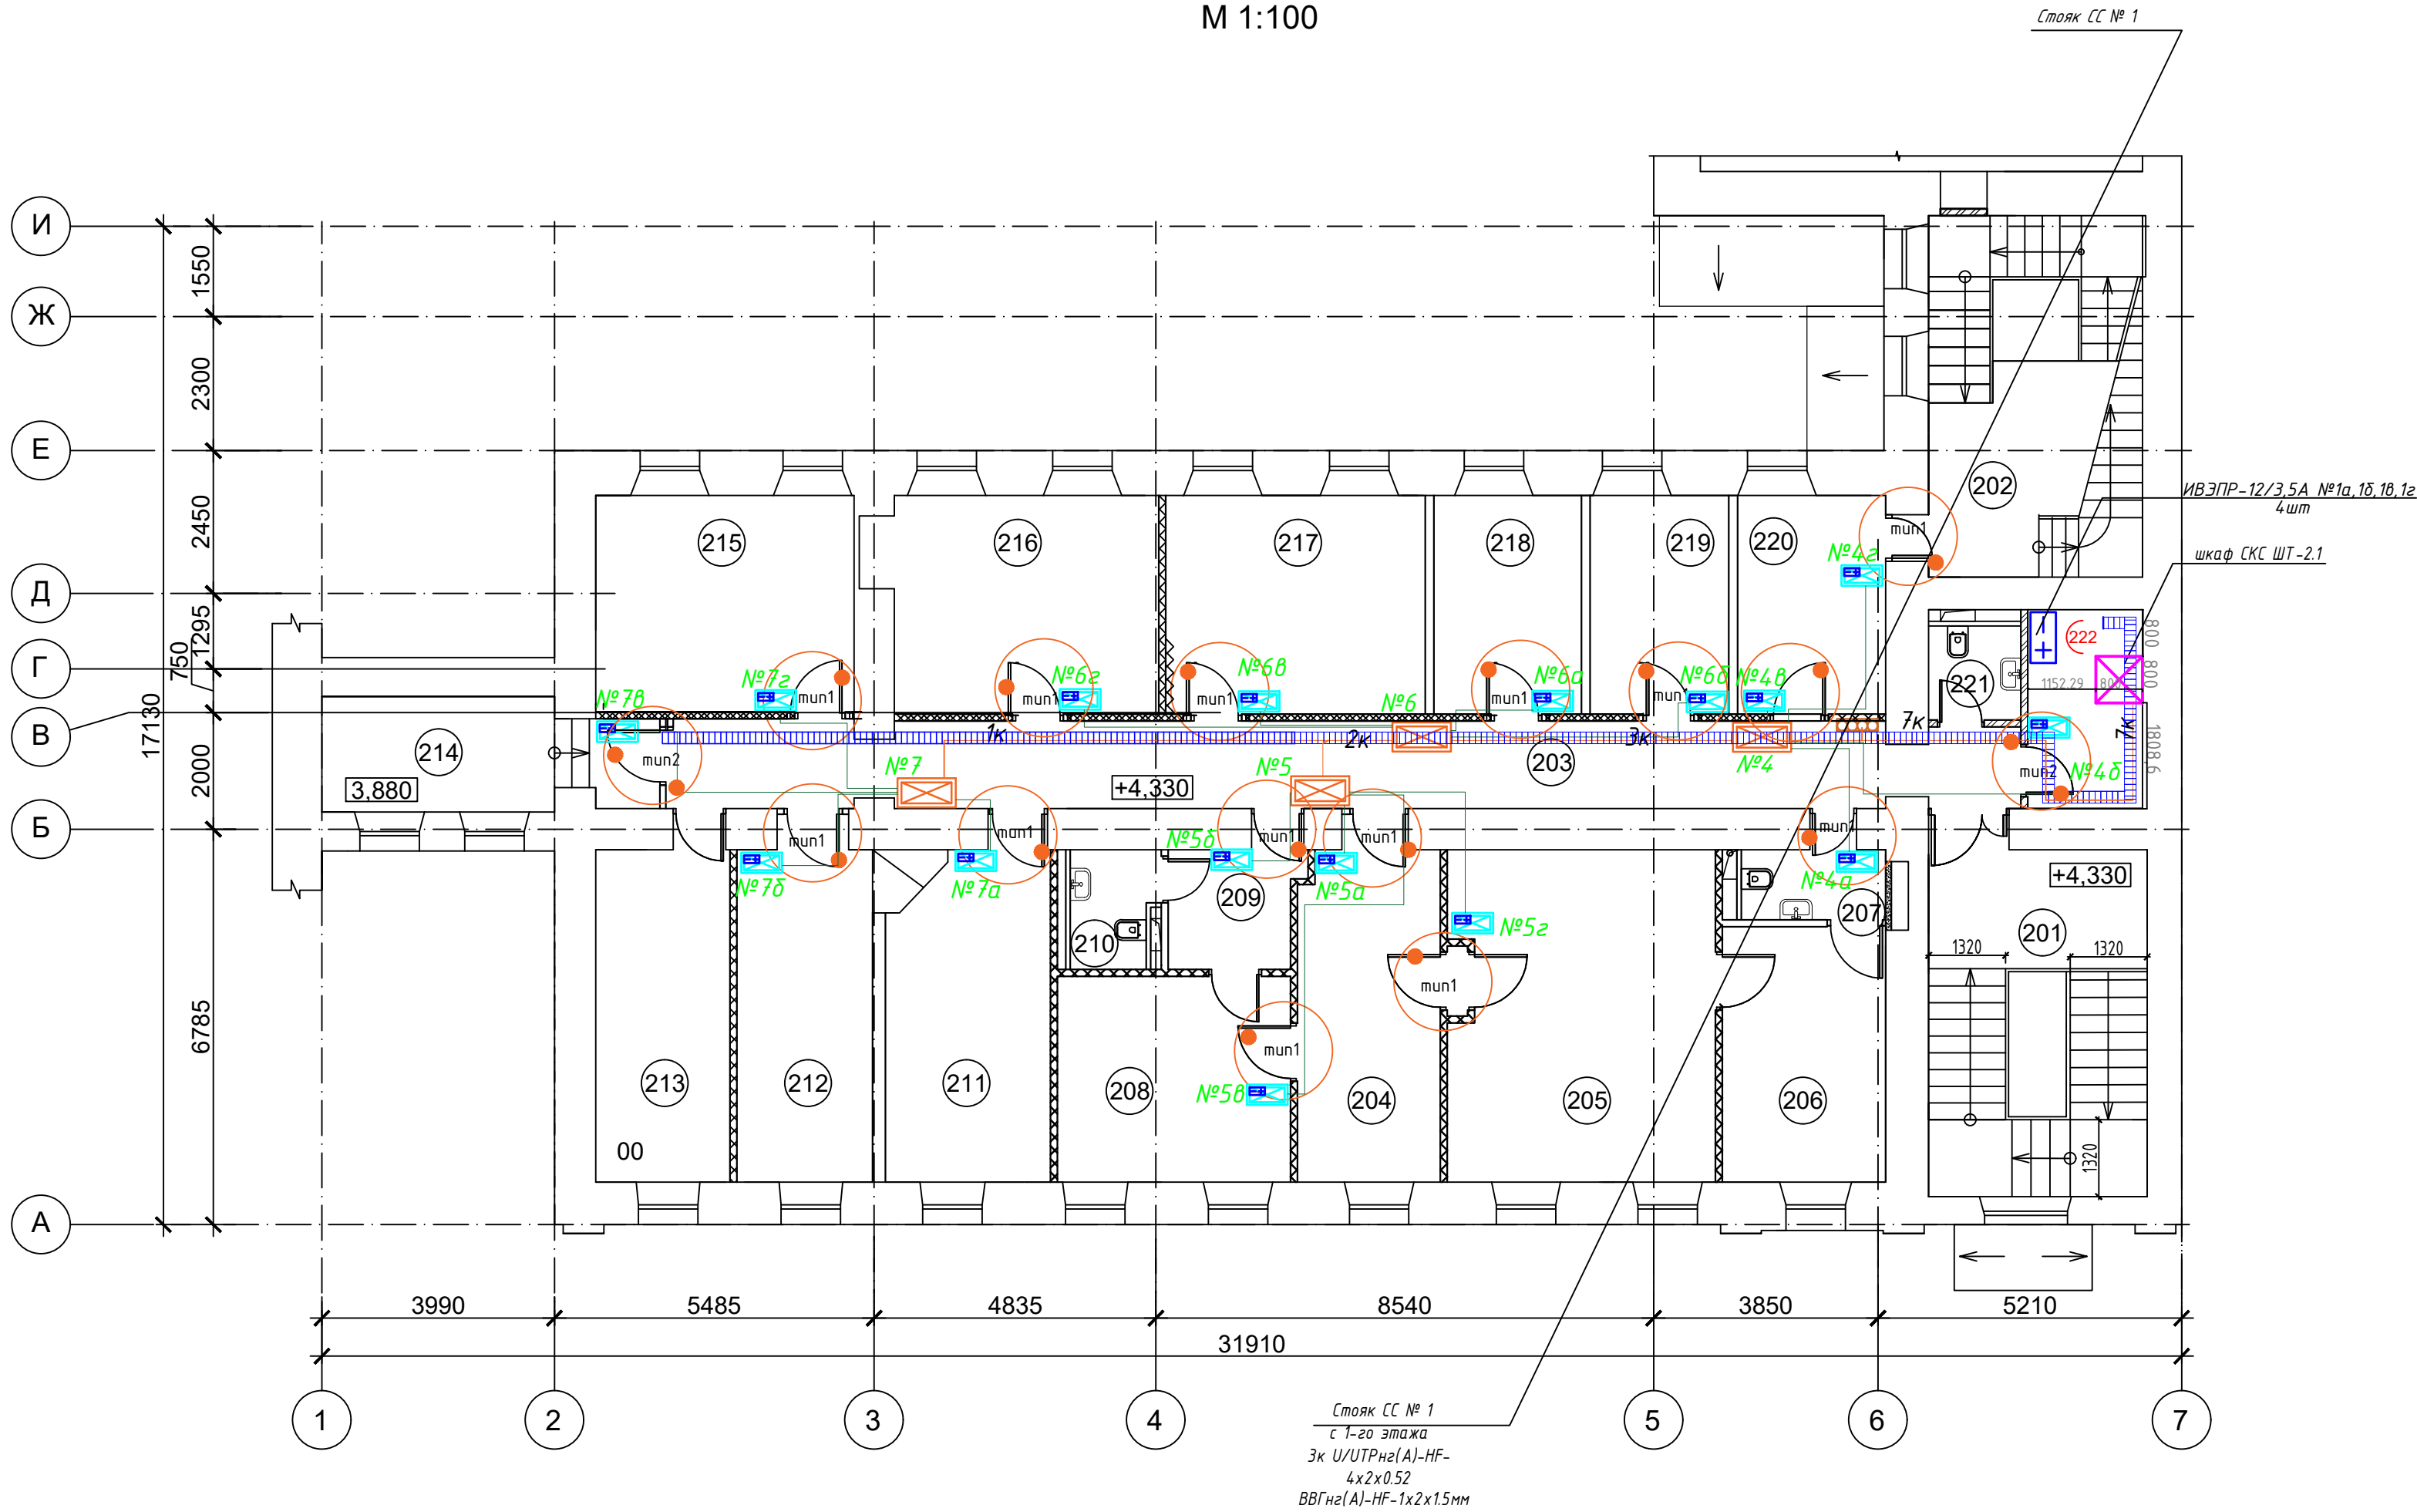

Экспликация помещений 2-го этажа			9
N п/п	Наименование помещений	Площадь м²	Кат. пом.
201	Лестница № 1 (ЛК тип 1)	23,1	
202	Лестница № 2 (ЛК тип 1)	22,8	
203	Коридор	34,2	
204	Приемная прокурора	14,5	
205	Кабинет прокурора / видеонаблюдение	25,9	
206	Комната отдыха прокурора	12,3	
207	Сан. узел прокурора	3,5	
208	Кабинет 1-го заместителя прокурора	14,1	
209	Комната отдыха 1-го заместителя прокурора	5,0	
210	Сан. узел 1-го заместителя прокурора	2,6	
211	Кабинет помощника прокурора	15,9	
212	Кабинет помощника прокурора	14,0	
213	Кабинет помощника прокурора	13,7	
214	Архив	10,3	ВЗ
215	Кабинет помощника прокурора	16,4	
216	Кабинет помощника прокурора	17,0	
217	Зал совещаний	16,7	
218	Кабинет помощника прокурора	9,5	
219	Кабинет помощника прокурора	8,9	
220	Комната прирема пищи	9,5	
221	Санузел	2,5	
222	Серверная	7,6	ВЗ
Итого:		300	

Схема расположения шкафа СС


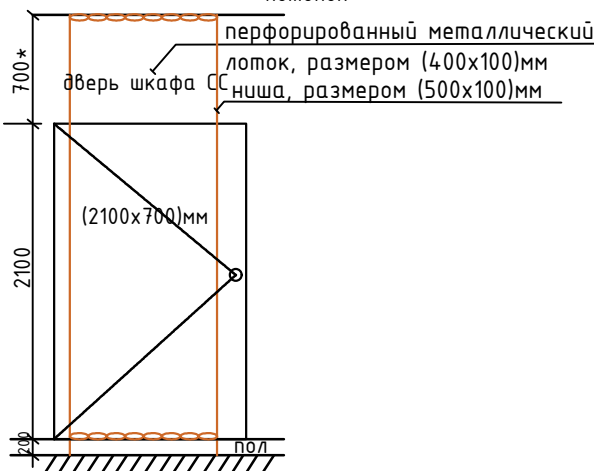



Схема расположения гильз d=50мм в перекрытиях

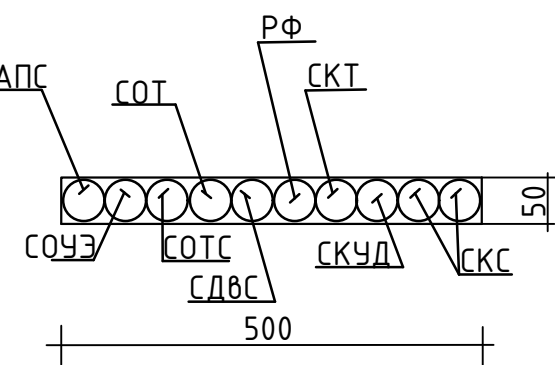

Условные обозначения

- ШТ-1.4

Телекоммуникационный шкаф 19" 42U напольный с указанием номера
- Патч -панель с указанием номера
- Коммутатор на 24 порта с PoE
- Источник электропитания 12В
- Контроллер доступа "STR20-IP"
- Модуль доступа "STR-1AP-M", встроенным ИБП
- Замок электромагнитный
- Извещатель охранный точечный магнитоконтактный
- Считыватель электронных идентификаторов
- Бесконтактная кнопка выхода
- Аварийная кнопка выхода
- Релейный модуль
- mun1 - односторонняя точка прохода
- mun2 - двухсторонняя точка прохода
- Кабели:
U/UTPn2(A)-HF-4x2x0.52
U/UTPn2(A)-HF-4x2x0.52
КПСВВn2(A)-HF-1x2x0.75
ЛОУТОКС 20n2(A)-FRHF -1x2x0.5
ВВГn2(A)-HF-1x2x1.5мм
- проволочный металлический лоток

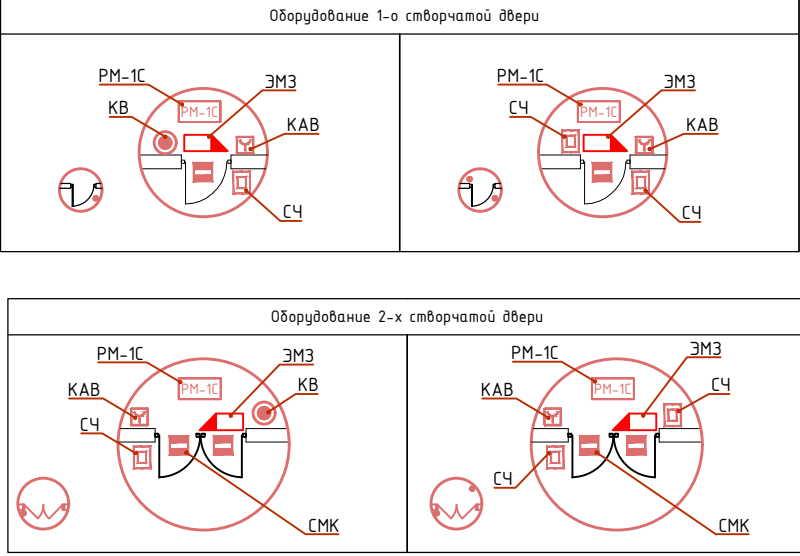

2025-00224-01-0- ИОС.7				
Капитальный ремонт здания и помещений по адресу г. Москва, ул. Мясницкая, д.44, стр.1.				
Изм.	Кол.уч.	Лист	№ док.	Подпись
Разработал	Белова Ф.И.	03.03.24		
Зав.сектор	Роянцева А.А.	03.03.24		
Структурированные кабельные сети				
План 2-го этажа. М 1:100. Расположение оборудования и кабельных трасс СКУД.				
Н. Контроль	Роянцева А.А.	03.03.24		
Нач.ОПИС	№1 Белоусова Д.П.	03.03.24		
Стадия			Лист	Листов
П			4	4
МОСЖИЛ НИИПРОЕКТ				

Согласована:				Позиция	Наименование и техническая характеристика	Тип, марка, обозначение документа, опросного листа	Код оборудования, изделия, материала	Завод-изготовитель	Единица измерения	Количество	Масса единицы кг	Примечания	11	
				1	2	3	4	5	6	7	8	9	
				15	Источник бесперебойного питания	Rapap-USB 3000		ЗАО "Бастуон"	шт.	1	
				16	Сетевой коммутатор RVI-1NSM16G-4H 16 портов	RVI-1NSM 16G-4H	арм.2310007	RVI	комп.	1	
				17	Карта Mifare стандартная	ST-PC010MF		Smartec	шт.	50	
					Кабельные изделия и материалы	
				1	Кабель	КПСВВнг(А)-HF -1х2х0.75мм		"Спецкабель"г.Подольск	м	80.0	
				2	Кабель	КПСВВнг(А)-HF -1х2х1.0мм		"Спецкабель"г.Подольск	м	70.0	
				3	Кабель	ЛОУТОКС 20нг(А)-FRHF-1х2х0.5		"Спецкабель"г.Подольск	м	50.0	
				4	Кабель	У\УТРнг(А)-HF-4х2х0,52 cat.5e		ПТД "Паритет"	м	270.0	
				5	Кабель	ВВГнг(А)-HF-1х2х1.5мм		"Спецкабель"г.Подольск	м	270.0	
				6	Труба гофрированная гибкая ПВХ-20мм			ДКС	м	540,0	
				7	Труба гофрированная гибкая ПВХ-16мм			ДКС	м	200,0	
				8	Гидроизоляционная огнеупорная мастика	AM-05		Россия	кг	1,0	
					ВИДЕОДОМОФОН	
					Оборудование	
				1	Монитор IP-видеодомофона 4.3" SIP протокол ,PoE, ОС Linux с поддержкой подключения IP-вызывных панелей и IP-камер.	SM-400W		ПП Бевард	шт	1	
				2	Вызывная Full HD IP-панель для видеодомофонов с углом обзора 146° врезной установки.	DS06AP		ПП Бевард	шт	2	
					Кабельные изделия и материалы	
				3	Кабель "витая пара" негорючий с низким выделением газа,дыма.	КПСВВнг(А)-LSLTx -4х2х0.5мм		"Спецкабель"г.Подольск	м	30.0	
				4	Кабель электрический негорючий с низким выделением газа,дыма.	ВВГнг(А)-LSLTx -1х2х1.5мм		"Спецкабель"г.Подольск	м	30.0	
5	Труба гофрированная самозатухающая «ТГ ПВХ» 20 мм		РТК-2-5-02	РТК	м	60,0	
6	Патч-корд RJ45, cat.5e, 1.0м					2	
Инв. N подл.	

АССОЦИАЦИЯ САМОРЕГУЛИРУЕМЫХ ОРГАНИЗАЦИЙ ОБЩЕРОССИЙСКАЯ НЕГОСУДАРСТВЕННАЯ НЕКОММЕРЧЕСКАЯ ОРГАНИЗАЦИЯ – ОБЩЕРОССИЙСКОЕ МЕЖОТРАСЛЕВОЕ ОБЪЕДИНЕНИЕ РАБОТОДАТЕЛЕЙ «НАЦИОНАЛЬНОЕ ОБЪЕДИНЕНИЕ САМОРЕГУЛИРУЕМЫХ ОРГАНИЗАЦИЙ, ОСНОВАННЫХ НА ЧЛЕНСТВЕ ЛИЦ, ВЫПОЛНЯЮЩИХ ИНЖЕНЕРНЫЕ ИЗЫСКАНИЯ, И САМОРЕГУЛИРУЕМЫХ ОРГАНИЗАЦИЙ, ОСНОВАННЫХ НА ЧЛЕНСТВЕ ЛИЦ, ОСУЩЕСТВЛЯЮЩИХ ПОДГОТОВКУ ПРОЕКТНОЙ ДОКУМЕНТАЦИИ»

9710075487-20260216-1017

(регистрационный номер выписки)

16.02.2026

(дата формирования выписки)

ВЫПИСКА

из единого реестра сведений о членах саморегулируемых организаций в области инженерных изысканий и в области архитектурно-строительного проектирования и их обязательствах

Настоящая выписка содержит сведения о юридическом лице (индивидуальном предпринимателе), осуществляющем подготовку проектной документации:

Государственное автономное учреждение города Москвы Московский научно-исследовательский и проектный институт жилищного хозяйства «МосжилНИИпроект»

(полное наименование юридического лица/ФИО индивидуального предпринимателя)

1197746303204

(основной государственный регистрационный номер)

1. Сведения о члене саморегулируемой организации:

1.1	Идентификационный номер налогоплательщика	9710075487
1.2	Полное наименование юридического лица (Фамилия Имя Отчество индивидуального предпринимателя)	Государственное автономное учреждение города Москвы Московский научно-исследовательский и проектный институт жилищного хозяйства «МосжилНИИпроект»
1.3	Сокращенное наименование юридического лица	ГАУ «МосжилНИИпроект»
1.4	Адрес юридического лица Место фактического осуществления деятельности (для индивидуального предпринимателя)	107078, Россия, Москва, г. Москва, Каланчевская, 4/2, 1, -
1.5	Является членом саморегулируемой организации	Ассоциация проектировщиков инженерной инфраструктуры «Инфрадизайн» (СРО-П-218-15012021)
1.6	Регистрационный номер члена саморегулируемой организации	П-218-009710075487-0095
1.7	Дата вступления в силу решения о приеме в члены саморегулируемой организации	18.06.2021
1.8	Дата и номер решения об исключении из членов саморегулируемой организации, основания исключения	

2. Сведения о наличии у члена саморегулируемой организации права осуществлять подготовку проектной документации:

2.1 в отношении объектов капитального строительства (кроме особо опасных, технически сложных и уникальных объектов, объектов использования атомной энергии) (дата возникновения/изменения права)	2.2 в отношении особо опасных, технически сложных и уникальных объектов капитального строительства (кроме объектов использования атомной энергии) (дата возникновения/изменения права)	2.3 в отношении объектов использования атомной энергии (дата возникновения/изменения права)
Да, 18.06.2021	Нет	Нет



3. Компенсационный фонд возмещения вреда

13

3.1	Уровень ответственности члена саморегулируемой организации по обязательствам по договору подряда на подготовку проектной документации, в соответствии с которым указанным членом внесен взнос в компенсационный фонд возмещения вреда	Третий уровень ответственности (не превышает триста миллионов рублей)
3.2	Сведения о приостановлении / прекращении права осуществлять подготовку проектной документации объектов капитального строительства	

4. Компенсационный фонд обеспечения договорных обязательств

4.1	Дата, с которой член саморегулируемой организации имеет право осуществлять подготовку проектной документации по договорам подряда, заключаемым с использованием конкурентных способов заключения договоров, в соответствии с которым указанным членом внесен взнос в компенсационный фонд обеспечения договорных обязательств	18.06.2021
4.2	Уровень ответственности члена саморегулируемой организации по обязательствам по договорам подряда на подготовку проектной документации, заключаемым с использованием конкурентных способов заключения договоров, в соответствии с которым указанным членом внесен взнос в компенсационный фонд обеспечения договорных обязательств	Четвертый уровень ответственности (составляет триста миллионов рублей и более)
4.3	Дата уплаты дополнительного взноса	Нет
4.4	Сведения о приостановлении / прекращении права осуществлять подготовку проектной документации по договорам подряда, заключаемым с использованием конкурентных способов заключения договоров	

5. Фактический совокупный размер обязательств

5.1	Фактический совокупный размер обязательств по договорам подряда на подготовку проектной документации, заключаемым с использованием конкурентных способов заключения договоров на дату выдачи выписки	399883177 руб.
-----	--	-----------------------



ДОКУМЕНТ ПОДПИСАН УСИЛЕННОЙ КВАЛИФИЦИРОВАННОЙ
ЭЛЕКТРОННОЙ ПОДПИСЬЮ

Владелец: «НАЦИОНАЛЬНОЕ ОБЪЕДИНЕНИЕ ИЗЫСКАТЕЛЕЙ И
ПРОЕКТИРОВЩИКОВ» «НОПРИЗ»

129090, г. Москва, пр-т Мира, 3, стр.3

СЕРТИФИКАТ 02 A9 64 C2 00 16 B3 DD A0 42 4E 1C 7B 48 A1 7E 77

ДЕЙСТВИТЕЛЕН: с 10.07.2025 по 10.10.2026



АССОЦИАЦИЯ САМОРЕГУЛИРУЕМЫХ ОРГАНИЗАЦИЙ ОБЩЕРОССИЙСКАЯ НЕГОСУДАРСТВЕННАЯ НЕКОММЕРЧЕСКАЯ ОРГАНИЗАЦИЯ – ОБЩЕРОССИЙСКОЕ МЕЖОТРАСЛЕВОЕ ОБЪЕДИНЕНИЕ РАБОТОДАТЕЛЕЙ «НАЦИОНАЛЬНОЕ ОБЪЕДИНЕНИЕ САМОРЕГУЛИРУЕМЫХ ОРГАНИЗАЦИЙ, ОСНОВАННЫХ НА ЧЛЕНСТВЕ ЛИЦ, ВЫПОЛНЯЮЩИХ ИНЖЕНЕРНЫЕ ИЗЫСКАНИЯ, И САМОРЕГУЛИРУЕМЫХ ОРГАНИЗАЦИЙ, ОСНОВАННЫХ НА ЧЛЕНСТВЕ ЛИЦ, ОСУЩЕСТВЛЯЮЩИХ ПОДГОТОВКУ ПРОЕКТНОЙ ДОКУМЕНТАЦИИ»

9710075487-20260216-1016

(регистрационный номер выписки)

16.02.2026

(дата формирования выписки)

ВЫПИСКА

из единого реестра сведений о членах саморегулируемых организаций в области инженерных изысканий и в области архитектурно-строительного проектирования и их обязательствах

Настоящая выписка содержит сведения о юридическом лице (индивидуальном предпринимателе), выполняющем инженерные изыскания:

Государственное автономное учреждение города Москвы Московский научно-исследовательский и проектный институт жилищного хозяйства "МосжилНИИпроект"

(полное наименование юридического лица/ФИО индивидуального предпринимателя)

1197746303204

(основной государственный регистрационный номер)

1. Сведения о члене саморегулируемой организации:

1.1	Идентификационный номер налогоплательщика	9710075487
1.2	Полное наименование юридического лица (Фамилия Имя Отчество индивидуального предпринимателя)	Государственное автономное учреждение города Москвы Московский научно-исследовательский и проектный институт жилищного хозяйства "МосжилНИИпроект"
1.3	Сокращенное наименование юридического лица	ГАУ "МосжилНИИпроект"
1.4	Адрес юридического лица Место фактического осуществления деятельности (для индивидуального предпринимателя)	107078, Россия, Москва, вн.тер.г. муниципальный округ Красносельский, ул. Каланчевская, д. 4/2, стр. 1
1.5	Является членом саморегулируемой организации	Ассоциация саморегулируемая организация «Центральное объединение организаций по инженерным изысканиям для строительства «Центризыскания» (СРО-И-003-14092009)
1.6	Регистрационный номер члена саморегулируемой организации	И-003-009710075487-0097
1.7	Дата вступления в силу решения о приеме в члены саморегулируемой организации	14.10.2009
1.8	Дата и номер решения об исключении из членов саморегулируемой организации, основания исключения	

2. Сведения о наличии у члена саморегулируемой организации права выполнять инженерные изыскания:

2.1 в отношении объектов капитального строительства (кроме особо опасных, технически сложных и уникальных объектов, объектов использования атомной энергии) (дата возникновения/изменения права)	2.2 в отношении особо опасных, технически сложных и уникальных объектов капитального строительства (кроме объектов использования атомной энергии) (дата возникновения/изменения права)	2.3 в отношении объектов использования атомной энергии (дата возникновения/изменения права)
Да, 14.10.2009	Да, 28.06.2023	Нет



3. Компенсационный фонд возмещения вреда

15/15

3.1	Уровень ответственности члена саморегулируемой организации по обязательствам по договору подряда на выполнение инженерных изысканий, в соответствии с которым указанным членом внесен взнос в компенсационный фонд возмещения вреда	Третий уровень ответственности (не превышает триста миллионов рублей)
3.2	Сведения о приостановлении права выполнять инженерные изыскания объектов капитального строительства	

4. Компенсационный фонд обеспечения договорных обязательств

4.1	Дата, с которой член саморегулируемой организации имеет право выполнять инженерные изыскания по договорам подряда, заключаемым с использованием конкурентных способов заключения договоров, в соответствии с которым указанным членом внесен взнос в компенсационный фонд обеспечения договорных обязательств	01.07.2017
4.2	Уровень ответственности члена саморегулируемой организации по обязательствам по договорам подряда на выполнение инженерных изысканий, заключаемым с использованием конкурентных способов заключения договоров, в соответствии с которым указанным членом внесен взнос в компенсационный фонд обеспечения договорных обязательств	Третий уровень ответственности (не превышает триста миллионов рублей)
4.3	Дата уплаты дополнительного взноса	07.03.2019
4.4	Сведения о приостановлении права выполнять инженерные изыскания по договорам подряда, заключаемым с использованием конкурентных способов заключения договоров	

5. Фактический совокупный размер обязательств

5.1	Фактический совокупный размер обязательств по договорам подряда на выполнение инженерных изысканий, заключаемым с использованием конкурентных способов заключения договоров на дату выдачи выписки	7736457.93 руб.
-----	--	-----------------



ДОКУМЕНТ ПОДПИСАН УСИЛЕННОЙ КВАЛИФИЦИРОВАННОЙ
ЭЛЕКТРОННОЙ ПОДПИСЬЮ

Владелец: «НАЦИОНАЛЬНОЕ ОБЪЕДИНЕНИЕ ИЗЫСКАТЕЛЕЙ И
ПРОЕКТИРОВЩИКОВ» «НОПРИЗ»

129090, г. Москва, пр-т Мира, 3, стр.3

СЕРТИФИКАТ 02 A9 64 C2 00 16 B3 DD A0 42 4E 1C 7B 48 A1 7E 77

ДЕЙСТВИТЕЛЕН: с 10.07.2025 по 10.10.2026

