



Департамент капитального ремонта города Москвы Государственное автономное учреждение города Москвы Московский научно-исследовательский и проектный институт жилищного хозяйства «МосжилНИИпроект» (ГАУ «МосжилНИИпроект»)

mgnp@mgnp.mos.ru +7 495 624 40 65 107078, г. Москва, ул. Каланчевская, д. 4/2, стр. 1

Арх. №

**Капитальный ремонт здания,  
расположенного по адресу:  
г. Москва, ул. Мясницкая, дом 44, стр.1**

**Раздел 5. Сведения об инженерном оборудовании,  
о сетях и системах инженерно-технического обеспечения.**

**Подраздел 5. Сети связи**

**Часть 8. Система охранно-тревожной сигнализации.**

**Том 5.5.8**

**2025-00224-01-0-ИОС5.8**

**Капитальный ремонт здания,  
расположенного по адресу:  
г. Москва, ул. Мясницкая, дом 44, стр.1**

**Раздел 5. Сведения об инженерном оборудовании,  
о сетях и системах инженерно-технического обеспечения.**

**Подраздел 5. Сети связи**

**Часть 8. Система охранно-тревожной сигнализации.**

**Том 5.5.8**

**2025-00224-01-0-ИОС5.8**

Начальник ОПИС №1

ГИП



Д.П. Белоусова

07.04.2026

В.Ю. Гунченко

07.04.2026

Содержание раздела

| №п/п | Наименование проектных материалов      | Марка листа | Стр.  |
|------|----------------------------------------|-------------|-------|
| 1    | Содержание раздела                     |             | 2     |
| 2    | Состав проектной документации          |             | 3     |
| 3    | Текстовая часть                        |             | 4-7   |
| 4    | Условные обозначения                   | ИОС5.8-1    | 8     |
| 5    | Принципиальная схема СОТС              | ИОС5.8-2    | 9     |
| 6    | План 1-го этажа. СОТС                  | ИОС5.8-3    | 10    |
| 7    | План 2-го этажа. СОТС                  | ИОС5.8-4    | 11    |
| 8    | План чердака. СОТС                     | ИОС5.8-5    | 12    |
| 9    | Спецификация оборудования и материалов | ИОС5.8-С1   | 13    |
| 10   | Спецификация оборудования и материалов | ИОС5.8-С2   | 14    |
| 11   | Выписка из реестра                     |             | 15-18 |
|      |                                        |             |       |
|      |                                        |             |       |
Согласовано

Взам. Инв. №

Подп. И дата

Инв. № подл.

2025-00224-01-0-ИОС5.8

|             |               |      |       |                                                                                     |          |
|-------------|---------------|------|-------|-------------------------------------------------------------------------------------|----------|
|             |               |      |       |                                                                                     |          |
| Изм.        | Кол.уч        | Лист | №док. | Подп.                                                                               | Дата     |
| Разработал  | Роянцева А.А. |      |       |  | 19.12.25 |
| Зав. сектор | Роянцева А.А. |      |       |  | 19.12.25 |
| Н.контроль  | Роянцева А.А. |      |       |                                                                                     | 19.12.25 |
| Нач.ОПИС№1  | Белюсова Д.П. |      |       |  | 19.12.25 |

Здания и помещения  
по адресу: г. Москва,  
ул. Мясницкая, д.44, стр.1

|        |      |        |
|--------|------|--------|
| Стадия | Лист | Листов |
| П      | 1    | 1      |



## Состав проектной документации

Смотри том 1.1, 2025-00224-01-1-СП, Часть1. Раздел1. Состав проектной документации.

[illegible]

## Текстовая часть.

### 1. Краткая характеристика объекта

Капитальный ремонт помещений по адресу: г Москва, ул. Мясницкая, д.44, стр.1

Данным проектом выполняются расстановка оконечного оборудования системы охранно-тревожной сигнализации.

Проектная документация разработана на основании нормативных документов, Рекомендаций Генеральной прокуратуры Российской Федерации и архитектурных чертежей стадии проектная документация.

### 2. Система охранно-тревожной сигнализации

Система охранно-тревожной сигнализации выполняет следующие функции:

- обнаруживает действия нарушителя и выдает извещение о несанкционированном проникновении в здание и отдельные помещения;
- выдает извещение о неисправности при отказе технических средств охранной сигнализации;
- сохраняет исправное состояние при воздействии факторов окружающей среды;
- сохраняет устойчивость к установленным в стандартах на системы конкретного вида повреждениям какой-либо своей части и не вызывает других повреждений в системе или не приводит к косвенной опасности вне ее;
- сохраняет работоспособное состояние при отключении основного источника электропитания в течение времени прерывания электропитания;
- оповещение службы охраны о срабатывании технических средств системы охранной сигнализации и контроля и управления доступом;
- автоматическое ведение отчета и сохранение его в базе о посетителях и обслуживающем персонале находящихся на территории комплекса.

Системой охранно-тревожной сигнализации оборудуются все помещения с постоянным или временным хранением материальных ценностей, а также все уязвимые места здания (окна, двери, люки), через которые возможно несанкционированное проникновение в помещения объекта.

### 3. Обоснование выбора и описание оборудования СОТС

Помещения здания, подлежащие защите, оборудуются охранной сигнализацией по периметру цокольного и первого этажа.

**Двухрубежной системой охранной сигнализации оборудуются: кабинет прокурора, комната отдыха прокурора, приемная прокурора, кабинет 1-го заместителя прокурора, кабинет заместителя прокурора, кабинеты помощников прокурора и архив.**

2025-00224-01-0-ИОС5.8

|             |        |                |        |                                                                                     |          |                                                                           |   |      |        |
|-------------|--------|----------------|--------|-------------------------------------------------------------------------------------|----------|---------------------------------------------------------------------------|---|------|--------|
|             |        |                |        |                                                                                     |          | 2025-00224-01-0-ИОС5.8                                                    |   |      |        |
|             |        |                |        |                                                                                     |          |                                                                           |   |      |        |
| Изм.        | Кол.уч | Лист           | № док. | Подп.                                                                               | Дата     |                                                                           |   |      |        |
| Разработал  |        | Роянцева А.А.  |        |  | 19.12.25 | Здания и помещения<br>по адресу: г. Москва,<br>ул. Мясницкая, д.44, стр.1 | Стадия   | Лист | Листов |
| Зав. сектор |        | Роянцева А.А.  |        |  | 19.12.25 |                                                                           | П   | 1    | 5      |
|             |        |                |        |                                                                                     |          |                                                                           |   |      |        |
| Н.контроль  |        | Роянцева А.А.  |        |  | 19.12.25 |                                                                           |  <b>МОСЖИЛ<br/>НИИПРОЕКТ</b> |      |        |
| Нач.ОПИС№1  |        | Белуосова Д.П. |        |  | 19.12.25 |                                                                           |   |      |        |

В двухрубежную систему охранной сигнализации входит:

- защита оконных проемов на «разбитие»;
- защита объема помещения от «проникновения»;

Защита объема помещений от «проникновения» производится с помощью охранных объемных оптико-электронных извещателей.

Защита оконных проемов на «разбитие» производится с помощью охранных поверхностных звуковых извещателей.

Защита деревянных и пластиковых окон на «открывание» производится с помощью охранных магнитоконтактных извещателей.

Для оперативной передачи сигнала "Тревога" на пост охраны о противоправных действиях в отношении сотрудников (например, разбойных нападениях, хулиганских действиях, угрозах), предусмотрены кнопки тревожной сигнализации (ТС) КТ-R3, установленные в зоне стола. Кнопки установлены в кабинете прокурора, в приемной прокурора, в кабинете 1-го заместителя прокурора, в кабинете заместителя прокурора, в кабинетах помощников прокурора.

#### 4. Характеристика состава и структуры

Выбор типа и состава оборудования обусловлен требованиями архитектурной компоновкой объекта, а также требованием по аппаратно-программной совместимости с другими системами здания.

Указанные в проектной документации типы и марки оборудования указаны в качестве базовых аналогов, как соответствующее техническому уровню оснащения объекта. Окончательно тип оборудования будет уточняться перед началом монтажных работ и закупки оборудования. Применяемое оборудование должно соответствовать, по своим характеристикам, проектному аналогу, но не превышать его стоимость.

Проектом предусмотрено применение следующих типов оборудования для организации системы СОТС:

- АРМ в составе: системный блок, комплект ПО, монитор, клавиатура, мышь, ИБП;
- Прибор приемноконтрольный и управления Рубеж R3-Рубеж-2ОП СЕРИЯ "З";
- Модуль сопряжения R3-MC;
- Блок индикации и управления Рубеж R3-Рубеж-БИУ СЕРИЯ "З";
- Устройство оконечное объектовое «Приток-А-КОП-02»;
- Блок питания, 12В, 2А ИВЭПР 12/2 RS-R3;
- Аккумулятор 12В 7 Ач DTM 1207;
- Адресный релейный модуль РМ-1-R3;
- Интерфейсный модуль "ИМ-1 прот. R3"
- Изолятор шлейфа ИЗ-1 прот. R3;
- Извещатель объемный оптико-электронный адресный ИО 40920-2;
- Извещатель поверхностный звуковой адресный ИО 32920-2;
- Извещатель магнитоуправляемый адресный ИО 10220-2;
- Извещатель ручной точечный электроконтактный КТ-R3;
- Оповещатель световой "Маяк-12".

|              |              |              |      |        |      |       |       |      |      |                        |
|--------------|--------------|--------------|------|--------|------|-------|-------|------|------|------------------------|
| Взам. инв. № | Подп. и дата | Инв. № подл. |      |        |      |       |       |      | Лист |                        |
|              |              |              |      |        |      |       |       |      |      | 2025-00224-01-0-ИОС5.8 |
|              |              |              | Изм. | Кол.уч | Лист | № док | Подп. | Дата |      |                        |

Тревожная сигнализация

Согласно техническим условиям (ТУ) от 16.07.2025 г. исх. 20105/8-3479 для передачи сигнала «Тревога» на ПЦН, предусматривается установка тревожной кнопки ИО101-7/1 "Астра-321 исп.Т" на существующем посту охраны (пом.101а) на первом этаже. Передача осуществляется с помощью сети Ethernet и GPRS канала на пульт ФГКУ УВО ВНГ России по городу Москве. Устройством передачи выступает прибор УОО «Приток-А- КОП-05».

5. Перечень мероприятий по устойчивому функционированию сетей связи, в том числе чрезвычайных ситуациях

Оборудование систем функционирует в непрерывном круглосуточном режиме и требует бесперебойного электропитания, не допускающего перерыва в подаче электроэнергии в любых режимах работы электроустановок.

Резервное электропитание осуществляется аккумуляторными батареями и источниками бесперебойного питания, обеспечивающими резервное электропитание, при отключении основного, на протяжении 24-х часов в дежурном режиме и не менее 1 ч работы в тревожном режиме.

При монтаже электропроводки выполнить цветовую маркировку жил кабелей в соответствии с требованиями гл.2.1. ПУЭ.

Защитное заземление (зануление) электрооборудования и устройств СОС выполнить в соответствии с ПУЭ, требованиями ГОСТ 12.1.030-81 и технической документацией заводов-изготовителей на проектируемое оборудование.

6. Характеристика и обоснование принятых технических решений

Первым рубежом объекта защищается периметр помещения (окна) – ИО 10220-2, вторым рубежом объекта защищается объем помещения – ИО 40920-2. Все применяемые датчики адресные. Двери, оборудованные СКУД, охранной сигнализацией не оборудуются.

АРМ располагается на первом этаже на существующем посту. АРМ используется для нескольких систем: охранная сигнализация, система контроля и управления доступом.

Сигналы при срабатывании охранных извещателей поступают на ППКиУ Рубеж R3-Рубеж-2ОП СЕРИЯ "З", который в свою очередь выдает информацию на блок индикации и управления Рубеж R3-Рубеж-БИУ СЕРИЯ "З" и АРМ.

7. Характеристика линий связи

Используемая кабельная продукция соответствует ГОСТ и другим нормативным документам, действующих на территории РФ.

Для подключения охранных извещателей используется кабель КСВВнг(А)-HF 1х2х0,8. Кабель питания 12В КСВВнг(А)-HF 1х2х0,97. Линия интерфейса RS-485 – кабель Лоутокс 20нг(А)-HF 1х2х0,5. Подключение магнитоконтактных датчиков производится кабелем UTP Cat5e PVCLS 4х2х0,52 нг(А)-HF.

|              |  |
|--------------|--|
| Взам. инв. № |  |
| Подп. и дата |  |
| Инв. № подл. |  |

|      |        |      |      |       |      |                        |      |
|------|--------|------|------|-------|------|------------------------|------|
|      |        |      |      |       |      | 2025-00224-01-0-ИОС5.8 | Лист |
|      |        |      |      |       |      |                        |      |
| Изм. | Кол.уч | Лист | №док | Подп. | Дата |                        | 3    |

## 8. Электроснабжение

В соответствии с требованиями РД 78.36.003-2002 и ПУЭ, оборудование в части обеспечения электроснабжения относится к потребителям электроэнергии 1-ой категории надежности электроснабжения.

Защита электрических цепей должна быть выполнена в соответствии с ПУЭ. Защитное заземление электрооборудования, металлических каркасов и конструкций следует выполнить в соответствии с ПУЭ и технической документацией на оборудование.

Оборудование систем функционирует в непрерывном круглосуточном режиме и требует бесперебойного электропитания, не допускающего перерыва в подаче электроэнергии в любых режимах работы электроустановок.

Система имеет автономное вторичное электропитание от внутренних аккумуляторных батарей способное обеспечить нормальное функционирование в условиях отсутствия внешнего напряжения питания 220 В, в течении не менее 1-го часа. При пропадании основного электропитания происходит автоматическое переключение на автономное вторичное электропитание от аккумуляторных батарей.

В соответствии с требованиями п.5.2.4 СП 2.13130.2020, места пересечения кабелей, кабеленесущих конструкций со строительными конструкциями с нормируемыми пределами огнестойкости, обеспечиваются проходками не ниже пределов огнестойкости, установленных для пересекаемых конструкций посредством установки гильз из труб с заделкой гидроизоляционной огнеупорной мастикой в соответствии с ГОСТ 30247.1, ГОСТ Р 53306, ГОСТ Р 53310.

|              |              |              |        |       |      |  |  |  |                        |  |  |
|--------------|--------------|--------------|--------|-------|------|--|--|--|------------------------|--|--|
| Инв. № подл. | Подп. и дата | Взам. инв. № |        |       |      |  |  |  | Лист                   |  |  |
|              |              |              |        |       |      |  |  |  | 2025-00224-01-0-ИОС5.8 |  |  |
|              |              |              |        |       |      |  |  |  | 4                      |  |  |
| Изм.         | Кол.уч       | Лист         | №докум | Подп. | Дата |  |  |  |                        |  |  |



9. **Перечень нормативных документов, использованных при разработке проектной документации**

- **ГОСТ Р 21.101-2020** «Система проектной документации для строительства (СПДС). Основные требования к проектной и рабочей документации». Постановление №87 от 16.02.2008 «О составе разделов проектной документации и требования к их содержанию» (утв. Приказом Росстандарта от 23.06.2020 N 282-СТ)
- **СП 118.13330.2022** «Общественные здания и сооружения»;
- **СП 1.13130.2020** «Системы противопожарной защиты. Эвакуационные пути и выходы»;
- ПУЭ издание 7 «Правила устройства электроустановок»;
- **Р 083-2019** «Нормы и правила проектирования систем безопасности на объектах, охраняемых (принимаемых под охрану) подразделениями вневедомственной охраны»;
- **Р 093-2024** «Обследование и прием под централизованную охрану подразделениями вневедомственной охраны войск национальной гвардии Российской Федерации объектов, мест проживания и хранение имущества граждан»;
- **Р 069-2017** «Рекомендации по выбору и применению средств обнаружения проникновения в зависимости от степени важности и опасности охраняемых объектов»;
- **Р 102-2024** «Инженерно-техническая укрепленность и оснащение техническими средствами охраны объектов и мест проживания и хранения имущества граждан, принимаемых под централизованную охрану подразделениями вневедомственной охраны войск национальной гвардии Российской Федерации»; принимаемых под централизованную охрану подразделениями вневедомственной охраны войск национальной гвардии Российской Федерации»;
- **Р 071-2017** «Технические средства систем безопасности объектов. Обозначения условные, графические элементов технических средств охраны, систем контроля и управления доступом, систем охранного телевидения»;
- **Р 035-2019** «Системы и комплексы охранной, пожарной и охранно-пожарной сигнализации. Правила производства и приемки работ».

|              |              |              |       |       |      |  |  |  |                        |  |  |
|--------------|--------------|--------------|-------|-------|------|--|--|--|------------------------|--|--|
| Инв. № подл. | Подп. и дата | Взам. инв. № |       |       |      |  |  |  | Лист                   |  |  |
|              |              |              |       |       |      |  |  |  | 2025-00224-01-0-ИОС5.8 |  |  |
|              |              |              |       |       |      |  |  |  | 5                      |  |  |
| Изм.         | Кол.уч       | Лист         | № док | Подп. | Дата |  |  |  |                        |  |  |

# Условные обозначения

| Обозначение                                                                           | Название                                                                               |
|---------------------------------------------------------------------------------------|----------------------------------------------------------------------------------------|
| АРК  | Приемно-контрольный прибор                                                             |
| БИУ  | блок индикации и управления                                                            |
| ИБП  | источник бесперебойного питания                                                        |
|      | модуль сопряжения "МС-Е".                                                              |
| BGC  | извещатель охранный объемный, типа Фотон-9М                                            |
| BGS  | Извещатель охранный поверхностный звуковой, типа СтеклоЗ                               |
| BGB  | извещатель охранный магнитоконтактный                                                  |
| BGL  | извещатель охранный объемный, типа Фотон-10БМ                                          |
| BGA  | извещатель охранный вибрационный поверхностный, типа Шорох-2                           |
| BGR  | извещатель охранный объемный радиоволновой, типа Аргус-2                               |
| BGM  | извещатель охранный точечный                                                           |
|      | изолятор шлейфа "ИЗ-1 прот.РЗ" (ИЗ);                                                   |
|      | линия интерфейса RS-485 КСВВнз(А)-LS 2x0,5;                                            |
|      | кабель КСВВнз(А)-LS 1x2x0,8;                                                           |
|      | кабель UTP Cat5e PVCLS 4x2x0,52 нз(А)-LS;                                              |
|    | Оповещатель «Световой»                                                                 |
|    | Извещатель охранный «Точечный электроконтактный (ручной)»                              |
|    | Извещатель охранный «Точечный электроконтактный (ручной)»<br>«носимый радиобрелок КТС» |
|    | Устройство СПИ «Приемник (системы передачи извещений по радиоканалу»                   |
|    | Прибор приемно-контрольный охранный "Приток-А-КОП-05"                                  |
|    | Источник бесперебойного электропитания                                                 |

Согласовано

Взам. инв.№

подпись и дата

Инв. № подл.

2025-00224-01-1-ИОС 5.8

Здания и помещения по адресу: г. Москва  
ул. Мясницкая, д.44, стр.1

| Изм.        | Кол.уч.       | Лист | № док. | Подпись                                                                             | Дата     |
|-------------|---------------|------|--------|-------------------------------------------------------------------------------------|----------|
| Разработал  | Роянцева А.А. |      |        |  | 19.12.25 |
| Зав.сектора | Роянцева А.А. |      |        |  | 19.12.25 |
| Норм.Контр. | Роянцева А.А. |      |        |  | 19.12.25 |
| Нач.ОПИС№1  | Белюсова Д.П. |      |        |  | 19.12.25 |

Капитальный ремонт


Условные обозначения

| Стадия | Лист | Листов |
|--------|------|--------|
| П      | 1    |        |



Принципиальная схема системы охранно-тревожной сигнализации

Схема передачи сигнала на пульт ПЦН

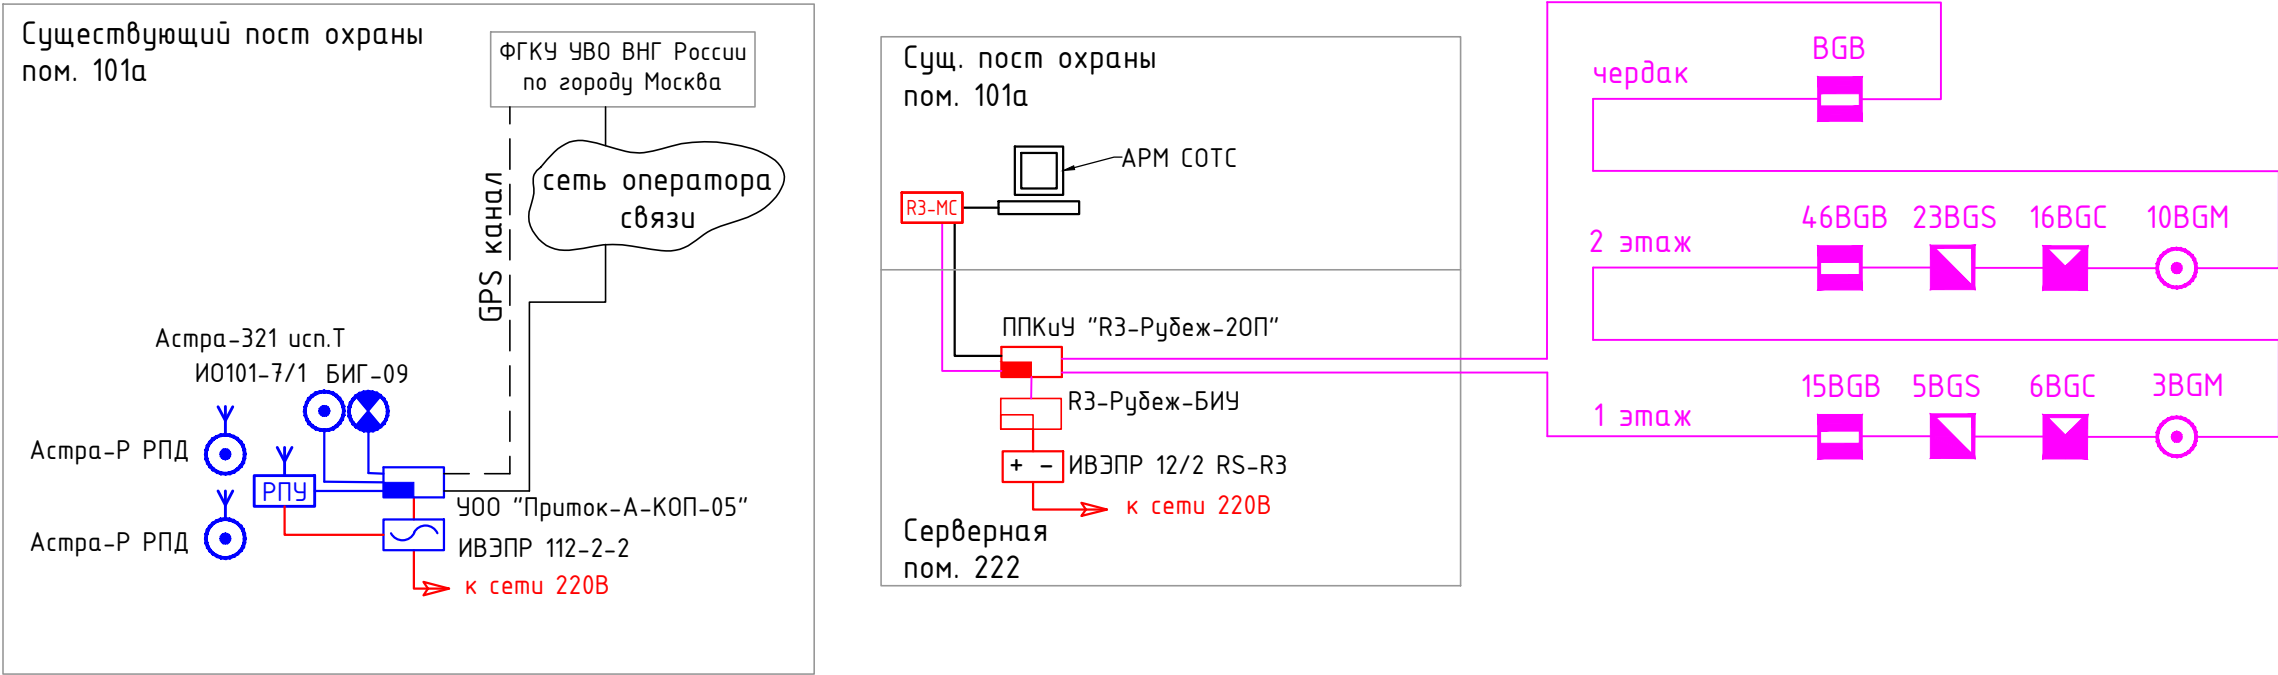

Согласована:

|              |                |              |
|--------------|----------------|--------------|
| Инв. N подл. | Подпись и дата | Взам. инв. N |
|              |                |              |
|              |                |              |
|              |                |              |

|             |               |      |        |                                                                                       |          |                                                                       |   |      |        |
|-------------|---------------|------|--------|---------------------------------------------------------------------------------------|----------|-----------------------------------------------------------------------|---|------|--------|
|             |               |      |        |                                                                                       |          | 2025-00224-01-1-ИОС 5.8                                               |   |      |        |
|             |               |      |        |                                                                                       |          | Здания и помещения по адресу: г. Москва<br>ул. Мясницкая, д.44, стр.1 |   |      |        |
| Изм.        | Кол.уч.       | Лист | № док. | Подпись                                                                               | Дата     | Капитальный ремонт                                                    | Стадия   | Лист | Листов |
| Разработал  | Роянцева А.А. |      |        |  | 19.12.25 |                                                                       | П   | 2    |        |
| Зав.сектора | Роянцева А.А. |      |        |  | 19.12.25 |                                                                       |   |      |        |
|             |               |      |        |                                                                                       |          | Принципиальная схема<br>СОТС                                          |  <b>МОСЖИЛ<br/>НИИПРОЕКТ</b> |      |        |
| Норм.Контр. | Роянцева А.А. |      |        |  | 19.12.25 |                                                                       |   |      |        |
| Нач.ОПИС №1 | Белюсова Д.П. |      |        |  | 19.12.25 |                                                                       |   |      |        |

Architectural floor plan of a building with a grid system. The plan shows various rooms numbered 101 through 121. Rooms 106, 116, 115, 114, 113, 110, 109, 102, 101, and 101A are shaded. Rooms 107, 108, 103, 104, 105, 117, 118, 119, 120, and 121 are unshaded. The plan includes a staircase, a toilet, and a storage area labeled 'стояк СС'. Dimensions are provided for the grid lines: horizontal (3990, 5485, 4835, 31910, 8540, 3850, 5210) and vertical (17130, 750, 1295, 2000, 6785, 1550, 2300, 2450). The scale is 1:100.


| Экспликация помещений 1-го этажа |                                                 |                           |              |
|----------------------------------|-------------------------------------------------|---------------------------|--------------|
| № п/п                            | Наименование помещений                          | Площадь<br>м <sup>2</sup> | Кат.<br>пом. |
| 101                              | Лестница №1 (ЛК ти 1)                           | 22,9                      |              |
| 101А                             | Пост охраны                                     |                           |              |
| 102                              | Лестница № 2 (ЛК тип 1)                         | 17,7                      |              |
| 103                              | Коридор                                         | 39,4                      |              |
| 104                              | Кабинет заместителя прокурора                   | 15,9                      |              |
| 105                              | Комната отдыха заместителя прокурора            | 5,3                       |              |
| 106                              | Кабинет помощника прокурора / прием граждан МГН | 25,6                      |              |
| 107                              | Кабинет помощника прокурора                     | 4,8                       |              |
| 108                              | Архив                                           | 7,9                       | В4           |
| 109                              | Ввод водопровода                                | 4,3                       |              |
| 110                              | Кабинет для приема граждан                      | 4,9                       |              |
| 111                              | Санузел                                         | 1,8                       |              |
| 112                              | Санузел МГН                                     | 6,7                       |              |
| 113                              | Санузел заместителя прокурора                   | 2,8                       |              |
|                                  | ИТОГО:                                          | 160                       |              |

| Помещения не входящие в зону ремонта |                        |                           |              |
|--------------------------------------|------------------------|---------------------------|--------------|
| № п/п                                | Наименование помещений | Площадь<br>м <sup>2</sup> | Кат.<br>пом. |
| 114                                  | Офисное помещение      | 15,7                      |              |
| 115                                  | Офисное помещение      | 15,6                      |              |
| 116                                  | Офисное помещение      | 23,0                      |              |
| 117                                  | Офисное помещение      | 13,8                      |              |
| 118                                  | Офисное помещение      | 13,8                      |              |
| 119                                  | Офисное помещение      | 17,0                      |              |
| 120                                  | Офисное помещение      | 9,4                       |              |
| 121                                  | Офисное помещение      | 10,1                      |              |
|                                      | ИТОГО:                 | 118,4                     |              |

\* - кабинет для работы с секретными документами

1. В здании предусматривается капитальный ремонт, размеры проемов в капитальных стенах увеличению не подлежат.

Узел прохода кабельной линии через стену, перекрытие

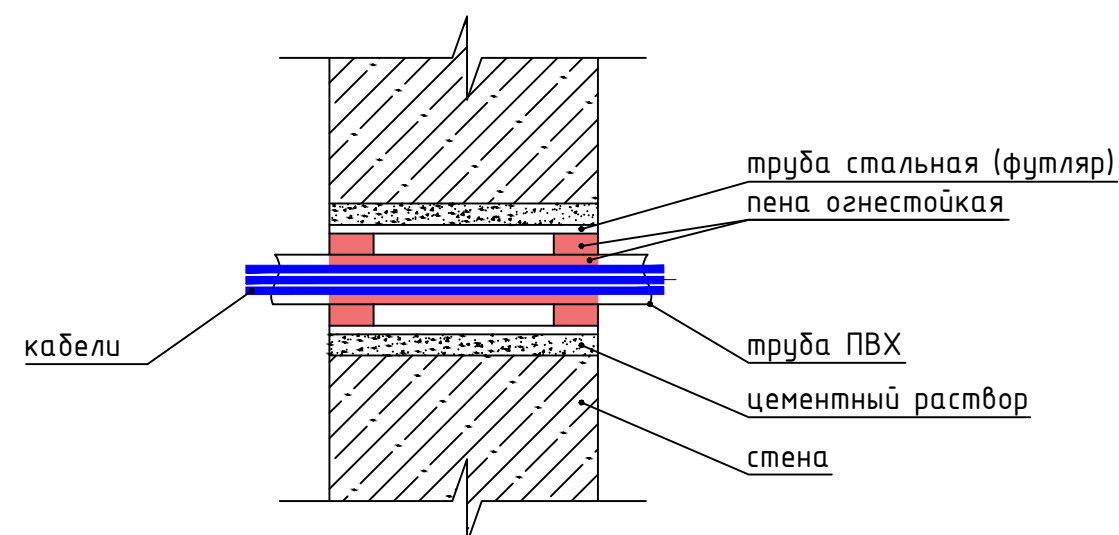

|             |         |                |        |                       |          |                                                                       |                                                                                       |                     |        |
|-------------|---------|----------------|--------|-----------------------|----------|-----------------------------------------------------------------------|---------------------------------------------------------------------------------------|---------------------|--------|
|             |         |                |        |                       |          | 2025-00224-01-1-ИОС.5.8                                               |                                                                                       |                     |        |
|             |         |                |        |                       |          | Здания и помещения по адресу: г. Москва<br>ул. Мясницкая, д.44, стр.1 |                                                                                       |                     |        |
| Изм.        | Кол.уч. | Лист           | № док. | Подпись               | Дата     | Капитальный ремонт                                                    | Стадия                                                                                | Лист                | Листов |
| Разработал  |         | Роянцева А.А.  |        | <i>А.А. Роянцева</i>  | 19.12.25 |                                                                       | П                                                                                     | 3                   |        |
| Зав.сектора |         | Роянцева А.А.  |        | <i>А.А. Роянцева</i>  | 19.12.25 |                                                                       |                                                                                       |                     |        |
|             |         |                |        |                       |          |                                                                       |                                                                                       |                     |        |
| Норм.Контр. |         | Роянцева А.А.  |        | <i>А.А. Роянцева</i>  | 19.12.25 | План 1-го этажа.                                                      |  | МОСЖИЛ<br>НИИПРОЕКТ |        |
| Нач.ОПИС№1  |         | Белосцова Д.П. |        | <i>Д.П. Белосцова</i> | 19.12.25 |                                                                       |                                                                                       |                     |        |


Согласовано

|               |              |               |
|---------------|--------------|---------------|
| Инв. N° подл. | Подп. и дата | Взам. инв. N° |
|---------------|--------------|---------------|

Согласовано


Взам. инв. №  
Подп. и дата  
Инв. № подл.

План 2-го этажа на отм. +3.800  
М 1:100

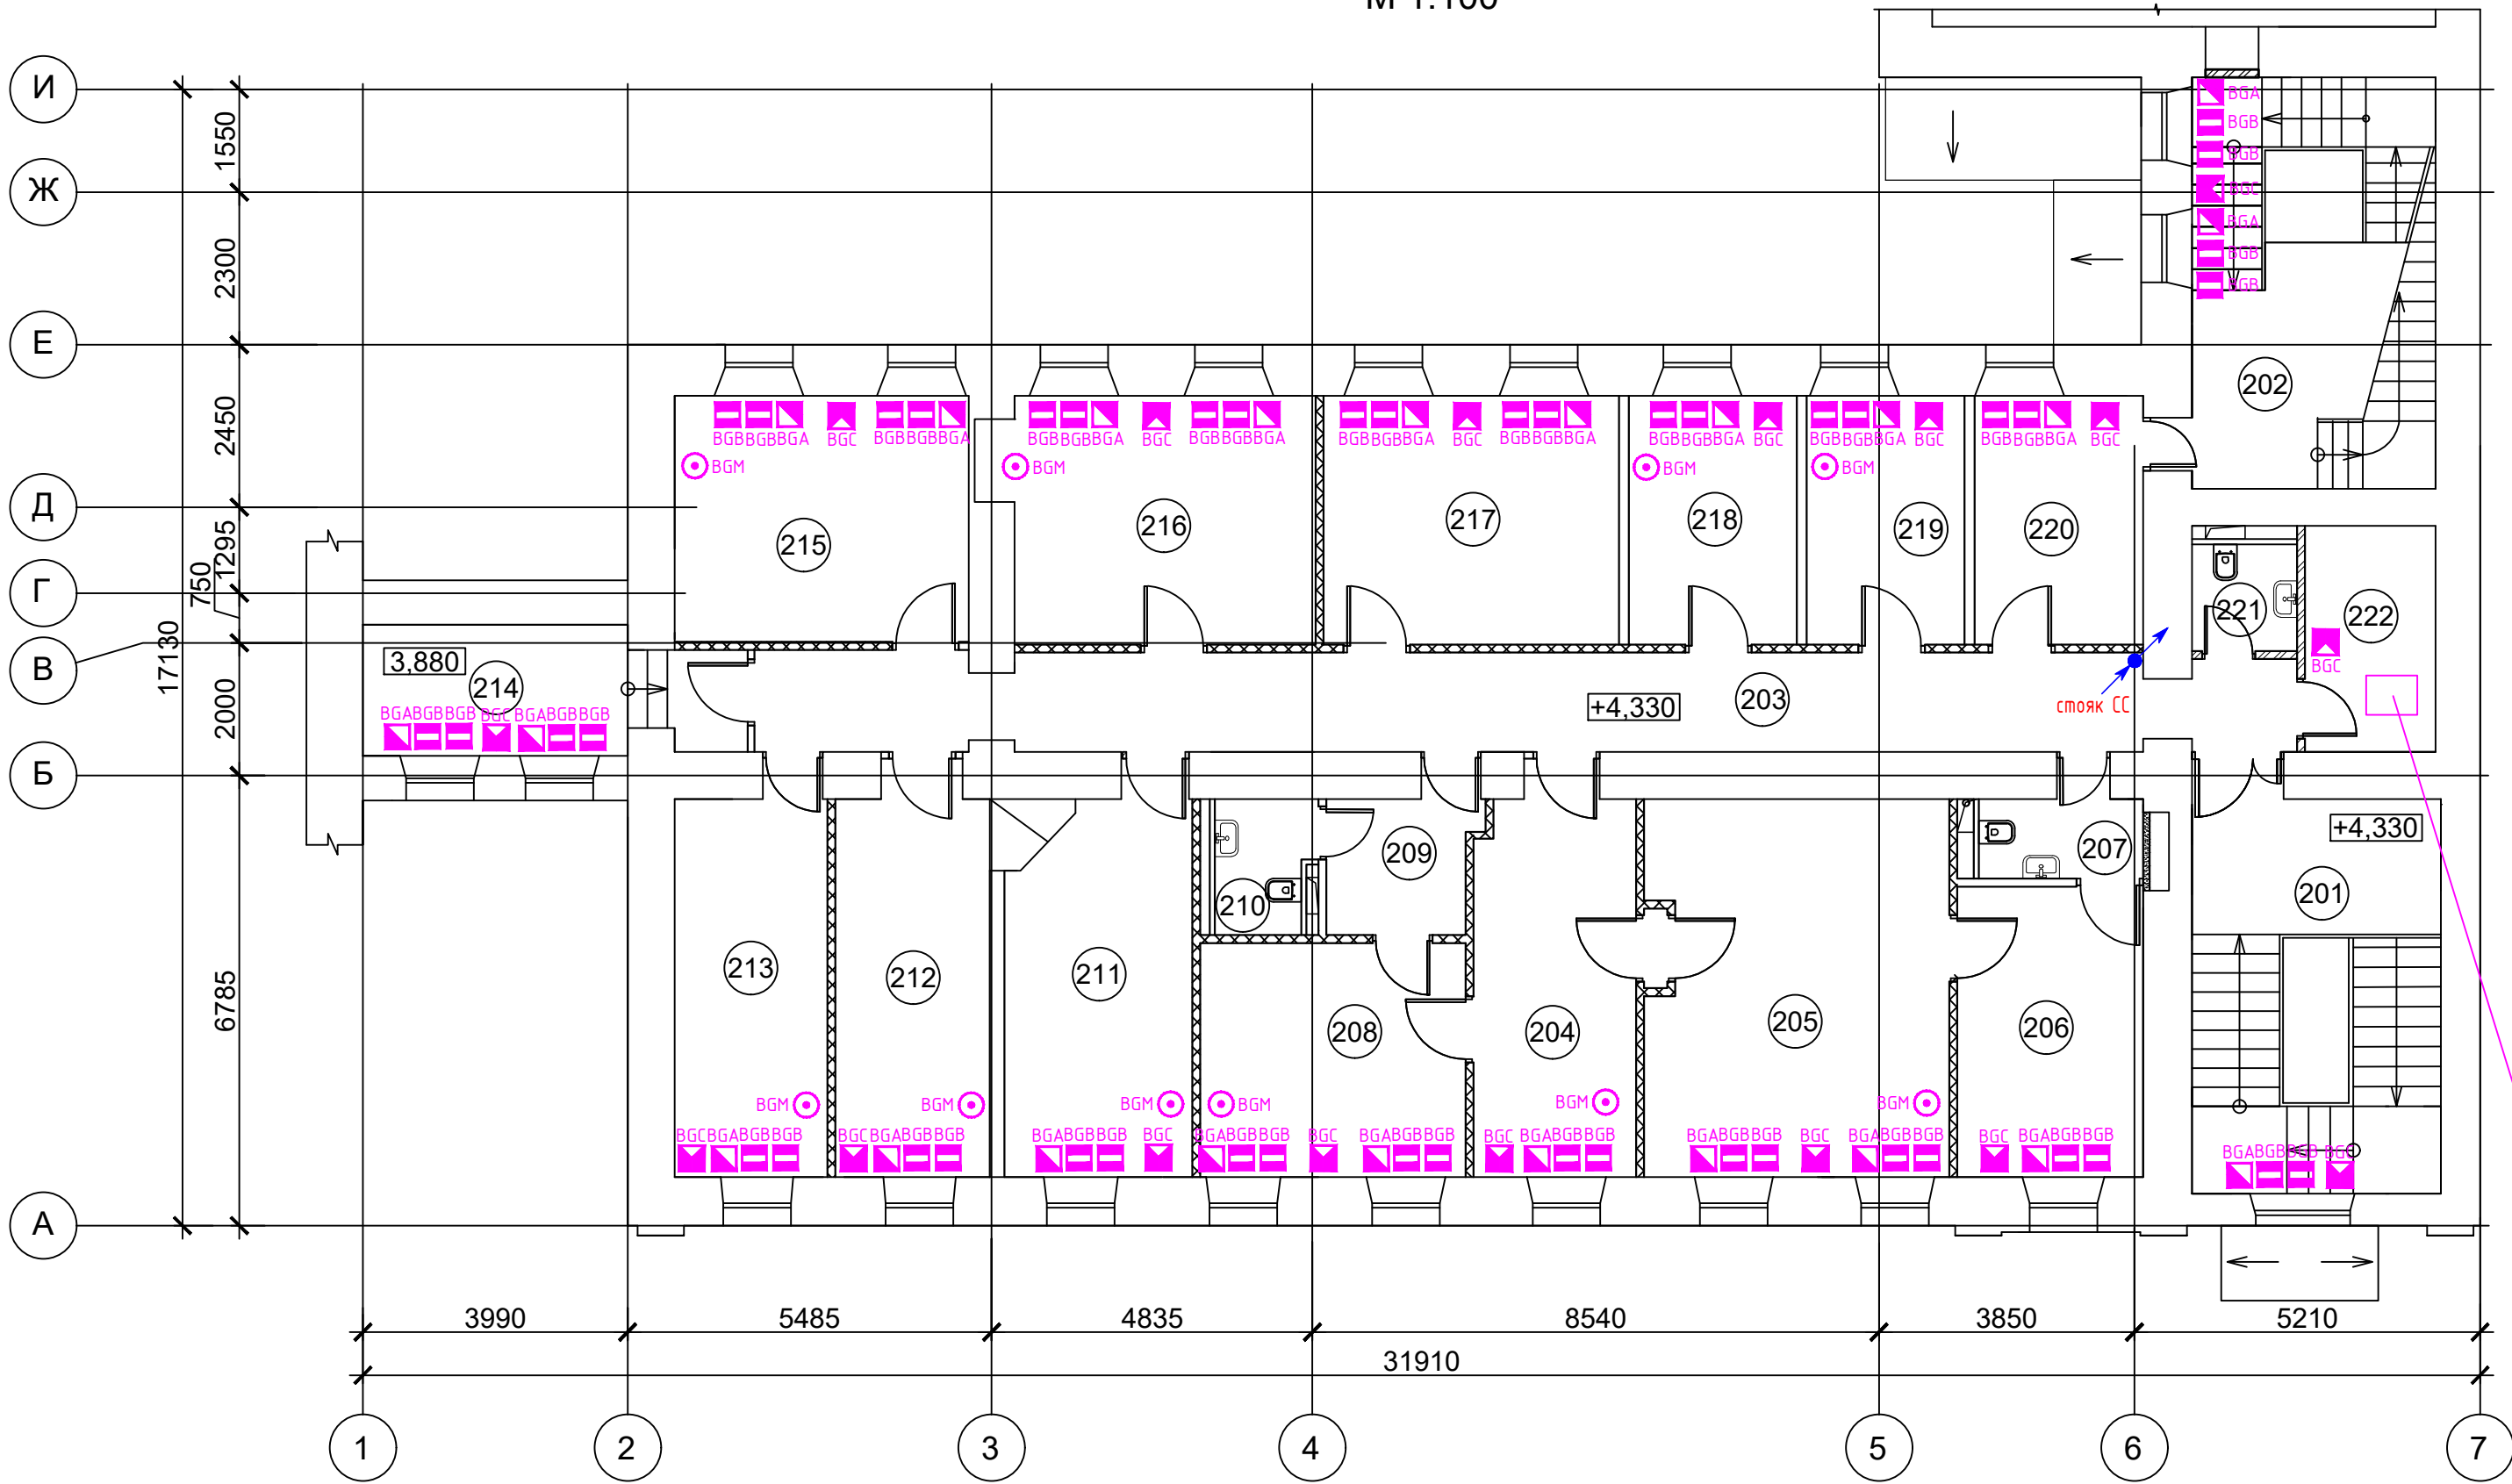

| Экспликация помещений 2-го этажа |                                           |            |           |
|----------------------------------|-------------------------------------------|------------|-----------|
| N п/п                            | Наименование помещений                    | Площадь м² | Кат. пом. |
| 201                              | Лестница № 1 (ЛК тип 1)                   | 23,1       |           |
| 202                              | Лестница № 2 (ЛК тип 1)                   | 22,8       |           |
| 203                              | Коридор                                   | 34,2       |           |
| 204                              | Приемная прокурора                        | 14,5       |           |
| 205                              | Кабинет прокурора / видеонаблюдение       | 25,9       |           |
| 206                              | Комната отдыха прокурора                  | 12,3       |           |
| 207                              | Сан. узел прокурора                       | 3,5        |           |
| 208                              | Кабинет 1-го заместителя прокурора        | 14,1       |           |
| 209                              | Комната отдыха 1-го заместителя прокурора | 5,0        |           |
| 210                              | Сан. узел 1-го заместителя прокурора      | 2,6        |           |
| 211                              | Кабинет помощника прокурора               | 15,9       |           |
| 212                              | Кабинет помощника прокурора               | 14,0       |           |
| 213                              | Кабинет помощника прокурора               | 13,7       |           |
| 214                              | Архив                                     | 10,3       | ВЗ        |
| 215                              | Кабинет помощника прокурора               | 16,4       |           |
| 216                              | Кабинет помощника прокурора               | 17,0       |           |
| 217                              | Зал совещаний                             | 16,7       |           |
| 218                              | Кабинет помощника прокурора               | 9,5        |           |
| 219                              | Кабинет помощника прокурора               | 8,9        |           |
| 220                              | Комната прирема пищи                      | 9,5        |           |
| 221                              | Санузел                                   | 2,5        |           |
| 222                              | Серверная                                 | 7,6        | ВЗ        |
| Итого:                           |                                           | 300        |           |

Узел прохода кабельной линии через стену, перекрытие

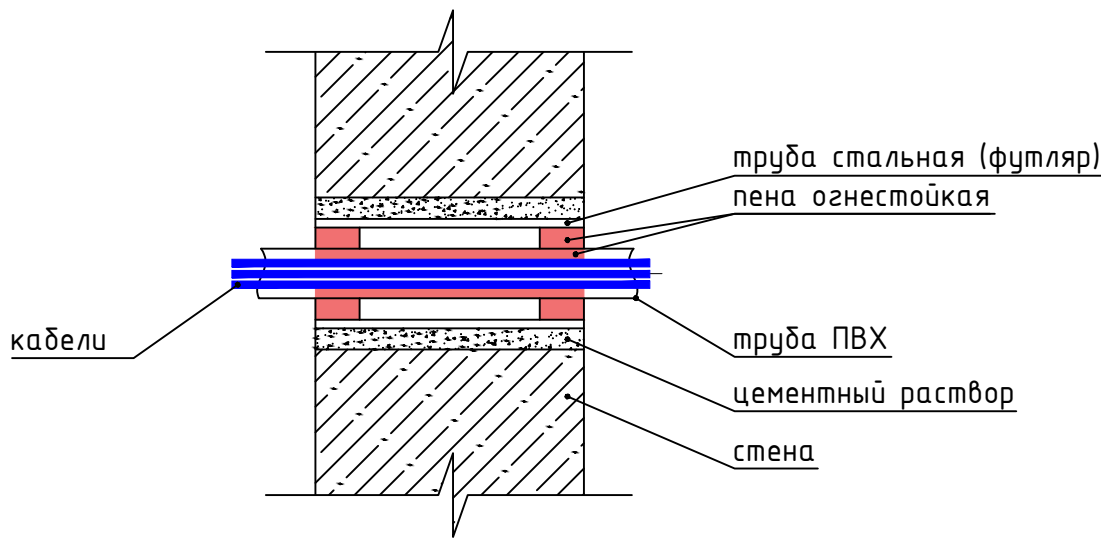


1. В здании предусматривается капитальный ремонт, размеры проемов в капитальных стенах увеличению не подлежат.


|                                                                       |               |          |        |         |      |
|-----------------------------------------------------------------------|---------------|----------|--------|---------|------|
| 2025-00224-01-1-ИОС 5.8                                               |               |          |        |         |      |
| Здания и помещения по адресу: г. Москва<br>ул. Мясницкая, д.44, стр.1 |               |          |        |         |      |
| Изм.                                                                  | Колуч.        | Лист     | № док. | Подпись | Дата |
| Разработал                                                            | Роянцева А.А. | 19.12.25 |        |         |      |
| Зав. сектора                                                          | Роянцева А.А. | 19.12.25 |        |         |      |
| Капитальный ремонт                                                    |               |          |        |         |      |
|                                                                       |               |          |        | Стадия  | Лист |
|                                                                       |               |          |        | П       | 4    |
| План 2-го этажа.                                                      |               |          |        |         |      |
| Норм.Контр.                                                           | Роянцева А.А. | 19.12.25 |        |         |      |
| Нач.ОПИС №1                                                           | Белюсова Д.П. | 19.12.25 |        |         |      |
| МОСЖИЛ<br>НИИПРОЕКТ                                                   |               |          |        |         |      |
| Формат ФОРМАТ                                                         |               |          |        |         |      |



План чердака М 1:100

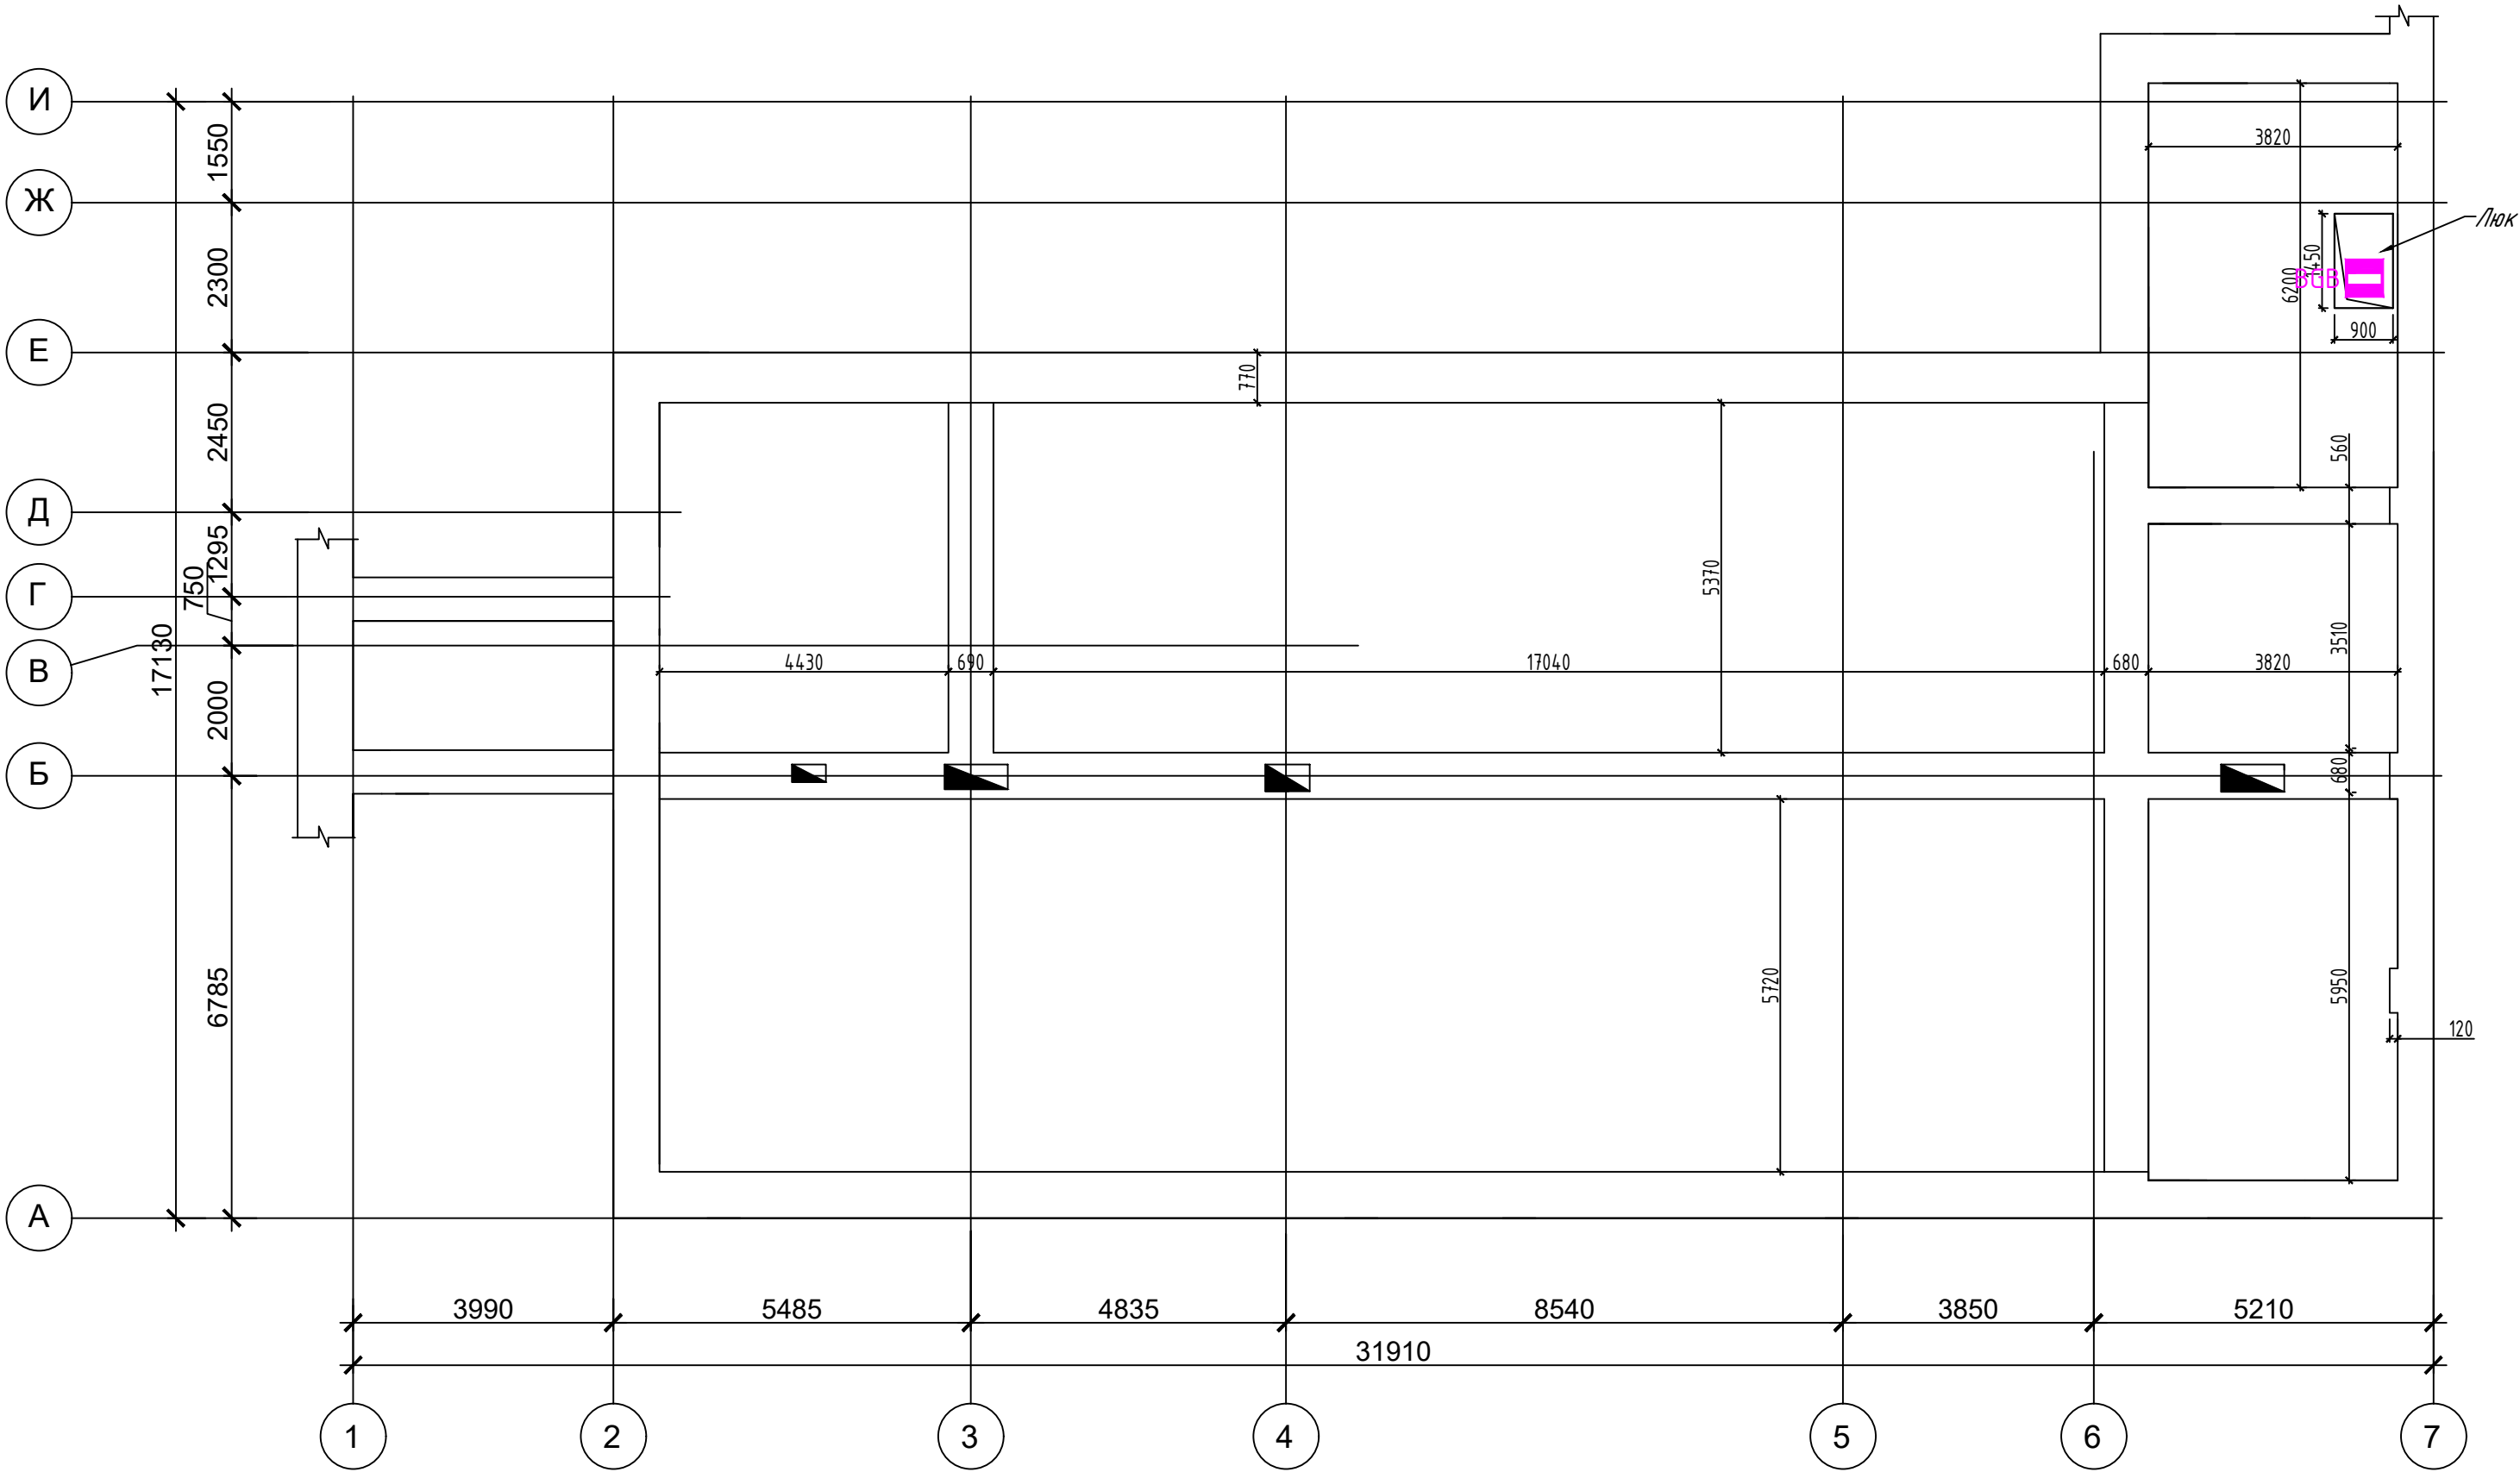

Узел прохода кабельной линии через стену, перекрытие

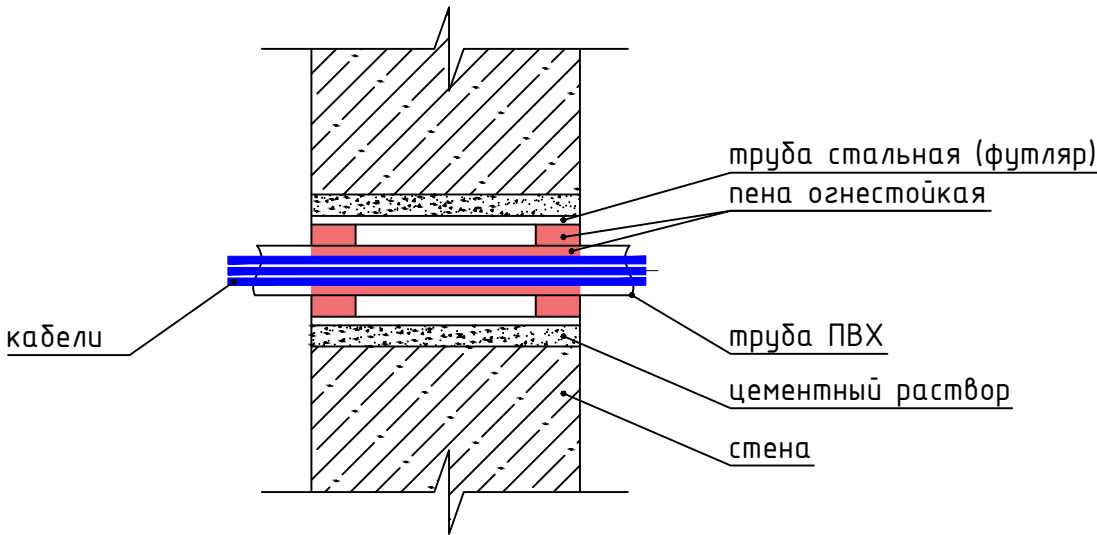

|             |               |      |        |         |          |                    |                                                                                       |      |        |  |
|-------------|---------------|------|--------|---------|----------|--------------------|---------------------------------------------------------------------------------------|------|--------|--|
|             |               |      |        |         |          |                    | 2025-00224-01-1-ИОС 5.8                                                               |      |        |  |
|             |               |      |        |         |          |                    | Здания и помещения по адресу: г. Москва<br>ул. Мясницкая, д.44, стр.1                 |      |        |  |
| Изм.        | Колуч.        | Лист | № док. | Подпись | Дата     | Капитальный ремонт | Стадия                                                                                | Лист | Листов |  |
| Разработал  | Роянцева А.А. |      |        |         | 19.12.25 |                    | П                                                                                     | 5    |        |  |
| Зав.сектора | Роянцева А.А. |      |        |         | 19.12.25 |                    |                                                                                       |      |        |  |
| Норм.Контр. | Роянцева А.А. |      |        |         | 19.12.25 | План чердака.      |  |      |        |  |
| Нач.ОПИС №1 | Белюсова Д.П. |      |        |         | 19.12.25 |                    |                                                                                       |      |        |  |



Согласована:

Взам. инв. №  
Подпись и дата  
Инв. № подл.

| Позиция | Наименование и техническая характеристика             | Тип, марка, обозначение документа, опросного листа | Код оборудования, изделия, материала | Завод-изготовитель | Единица измерения | Количество | Масса единицы кг | Примечания |
|---------|-------------------------------------------------------|----------------------------------------------------|--------------------------------------|--------------------|-------------------|------------|------------------|------------|
| 1       | 2                                                     | 3                                                  | 4                                    | 5                  | 6                 | 7          | 8                | 9          |
|         | СИСТЕМА ОХРАННО-ТРЕВОЖНОЙ СИГНАЛИЗАЦИИ                |                                                    |                                      |                    |                   |            |                  |            |
| 1       | АРМ СОТС, в составе:                                  |                                                    |                                      |                    | шт                | 1          |                  |            |
| 1.1     | АРМ ДЕРО ПЕРЕСВЕТ 110D11                              | 110D11                                             |                                      |                    | шт                | 1          |                  |            |
| 1.2     | Операционная система REDOS-DSP-STD-BAS-VDI            |                                                    |                                      |                    | шт                | 1          |                  |            |
| 1.3     | Монитор LCD 21 дюймов                                 |                                                    |                                      |                    | шт                | 1          |                  |            |
| 1.4     | Клавиатура, мышь                                      |                                                    |                                      |                    | шт                | 1          |                  |            |
| 1.5     | Источник бесперебойного питания, 600Вт                | Back Basic 1050S Euro                              |                                      |                    | шт                | 1          |                  |            |
|         |                                                       |                                                    |                                      |                    |                   |            |                  |            |
| 2       | Прибор приемно-контрольный и управления               | ППКУ "R3-Рудеж-20П"                                |                                      | Рудеж              | шт                | 1          |                  |            |
| 3       | Световой оповещатель                                  | "Маяк-12-С"                                        |                                      | КСС                | шт.               | 1          |                  |            |
| 4       | Модуль сопряжения                                     | R3-МС                                              |                                      | Рудеж              | шт                | 1          |                  |            |
| 5       | Блок индикации и управления                           | R3-Рудеж-БИУ                                       |                                      | Рудеж              | шт                | 1          |                  |            |
| 6       | Блок питания, 12В, 2А                                 | ИБЭПР 12/2 RS-R3                                   |                                      | Рудеж              | шт                | 1          |                  |            |
| 7       | Аккумулятор 12В 7 Ач                                  | DTM 1207                                           |                                      | Delta              | шт                | 2          |                  |            |
| 8       | Адресный релейный модуль                              | PM-1-R3                                            |                                      | Рудеж              | шт                | 1          |                  |            |
| 9       | Изолятор шлейфа                                       | ИЗ-1 прот.R3                                       |                                      | Рудеж              | шт                | 22         |                  |            |
| 10      | Извещатель охранный магнитоуправляемый адресный       | ИО 10220-2                                         |                                      | Рудеж              | шт                | 93         |                  |            |
| 11      | Извещатель охранный звуковой адресный, типа Стекло-3  | ИО 32920-2                                         |                                      | Рудеж              | шт                | 46         |                  |            |
| 12      | Извещатель охранный объемный, типа Фотон-9М           | ИО 40920-2                                         |                                      | Рудеж              | шт                | 22         |                  |            |
| 13      | Извещатель охранный ручной точечный электроконтактный | КТ-R3                                              |                                      | Рудеж              | шт.               | 15         |                  |            |
| 14      | Устройство оконечное объектовое                       | Приток-А-КОП-05                                    |                                      | Сократ             | шт.               | 1          |                  |            |
| 14.1    | Блок питания, 12В, 2А                                 | ИБЭПР 122-2-2                                      |                                      | Рудеж              | шт                | 1          |                  |            |
| 14.2    | Извещатель охранный ручной точечный электроконтактный | ИО 101-7/1 "Астра-321 исп.Т                        |                                      | Теко               | шт                | 2          |                  |            |
| 14.3    | Радиоприемное устройство                              | Астра-Р РПУ                                        |                                      | Теко               | шт                | 2          |                  |            |
| 14.4    | Брелок радиоканальный                                 | Астра-Р РПД                                        |                                      | Теко               | шт                | 4          |                  |            |
| 14.5    | Индикатор прибытия наряда                             | БИГ-09                                             |                                      |                    | шт.               | 2          |                  |            |

|                                                                    |               |      |        |         |          |                        |      |        |
|--------------------------------------------------------------------|---------------|------|--------|---------|----------|------------------------|------|--------|
|                                                                    |               |      |        |         |          | 2025-00224-01-1-ИОС5.8 |      |        |
| Изм.                                                               | Кол.уч.       | Лист | № док. | Подпись | Дата     |                        |      |        |
| Разработал                                                         | Роянцева А.А. |      |        |         | 19.12.25 |                        |      |        |
| Зав.сектора                                                        | Роянцева А.А. |      |        |         | 19.12.25 |                        |      |        |
| Норм.Контр                                                         | Роянцева А.А. |      |        |         | 19.12.25 |                        |      |        |
| Нач.ОПИС №                                                         | Белюсова Д.П. |      |        |         | 19.12.25 |                        |      |        |
| Здания и помещения по адресу: г. Москва ул. Мясницкая, д.44, стр.1 |               |      |        |         |          | Стадия                 | Лист | Листов |
|                                                                    |               |      |        |         |          | П                      | 1    | 2      |
|                                                                    |               |      |        |         |          | МОСЖИЛ НИИПРОЕКТ       |      |        |

[illegible][illegible]

|      |         |      |      |         |      |                         |      |
|------|---------|------|------|---------|------|-------------------------|------|
|      |         |      |      |         |      | 2025-00224-01-1-ИОС 5.8 | лист |
| Изм. | Кол.уч. | Лист | Ндк. | Подпись | Дата |                         | 2    |



**9710075487-20260216-1017**

(регистрационный номер выписки)

**16.02.2026**

(дата формирования выписки)

## ВЫПИСКА

**из единого реестра сведений о членах саморегулируемых организаций в области инженерных изысканий и в области архитектурно-строительного проектирования и их обязательствах**

**Настоящая выписка содержит сведения о юридическом лице (индивидуальном предпринимателе), осуществляющем подготовку проектной документации:**

**Государственное автономное учреждение города Москвы Московский научно-исследовательский и проектный институт жилищного хозяйства «МосжилНИИпроект»**

(полное наименование юридического лица/ФИО индивидуального предпринимателя)

**1197746303204**

(основной государственный регистрационный номер)

### 1. Сведения о члене саморегулируемой организации:

|     |   |   |
|-----|---|---|
| 1.1 | Идентификационный номер налогоплательщика                                                                         | 9710075487   |
| 1.2 | Полное наименование юридического лица<br>(Фамилия Имя Отчество индивидуального предпринимателя)                   | Государственное автономное учреждение города Москвы Московский научно-исследовательский и проектный институт жилищного хозяйства «МосжилНИИпроект» |
| 1.3 | Сокращенное наименование юридического лица                                                                        | ГАУ «МосжилНИИпроект»   |
| 1.4 | Адрес юридического лица<br>Место фактического осуществления деятельности<br>(для индивидуального предпринимателя) | 107078, Россия, Москва, г. Москва, Каланчевская, 4/2, 1, -                                                                                         |
| 1.5 | Является членом саморегулируемой организации                                                                      | Ассоциация проектировщиков инженерной инфраструктуры «Инфрадизайн» (СРО-П-218-15012021)                                                            |
| 1.6 | Регистрационный номер члена саморегулируемой организации                                                          | П-218-009710075487-0095   |
| 1.7 | Дата вступления в силу решения о приеме в члены саморегулируемой организации                                      | 18.06.2021   |
| 1.8 | Дата и номер решения об исключении из членов саморегулируемой организации, основания исключения                   |   |

### 2. Сведения о наличии у члена саморегулируемой организации права осуществлять подготовку проектной документации:

|   |   |                                                                                                |
|---|---|------------------------------------------------------------------------------------------------|
| 2.1 в отношении объектов капитального строительства (кроме особо опасных, технически сложных и уникальных объектов, объектов использования атомной энергии)<br>(дата возникновения/изменения права) | 2.2 в отношении особо опасных, технически сложных и уникальных объектов капитального строительства (кроме объектов использования атомной энергии)<br>(дата возникновения/изменения права) | 2.3 в отношении объектов использования атомной энергии<br>(дата возникновения/изменения права) |
| Да, 18.06.2021   | Нет   | Нет                                                                                            |



### 3. Компенсационный фонд возмещения вреда

|     |   |                                                                          |
|-----|---|--------------------------------------------------------------------------|
| 3.1 | Уровень ответственности члена саморегулируемой организации по обязательствам по договору подряда на подготовку проектной документации, в соответствии с которым указанным членом внесен взнос в компенсационный фонд возмещения вреда | Третий уровень ответственности<br>(не превышает триста миллионов рублей) |
| 3.2 | Сведения о приостановлении / прекращении права осуществлять подготовку проектной документации объектов капитального строительства   |                                                                          |

### 4. Компенсационный фонд обеспечения договорных обязательств

|     |   |                                                                                   |
|-----|---|-----------------------------------------------------------------------------------|
| 4.1 | Дата, с которой член саморегулируемой организации имеет право осуществлять подготовку проектной документации по договорам подряда, заключаемым с использованием конкурентных способов заключения договоров, в соответствии с которым указанным членом внесен взнос в компенсационный фонд обеспечения договорных обязательств      | 18.06.2021                                                                        |
| 4.2 | Уровень ответственности члена саморегулируемой организации по обязательствам по договорам подряда на подготовку проектной документации, заключаемым с использованием конкурентных способов заключения договоров, в соответствии с которым указанным членом внесен взнос в компенсационный фонд обеспечения договорных обязательств | Четвертый уровень ответственности<br>(составляет триста миллионов рублей и более) |
| 4.3 | Дата уплаты дополнительного взноса   | Нет                                                                               |
| 4.4 | Сведения о приостановлении / прекращении права осуществлять подготовку проектной документации по договорам подряда, заключаемым с использованием конкурентных способов заключения договоров   |                                                                                   |

### 5. Фактический совокупный размер обязательств

|     |   |                |
|-----|---|----------------|
| 5.1 | Фактический совокупный размер обязательств по договорам подряда на подготовку проектной документации, заключаемым с использованием конкурентных способов заключения договоров на дату выдачи выписки | 399883177 руб. |
|-----|---|----------------|



ДОКУМЕНТ ПОДПИСАН УСИЛЕННОЙ КВАЛИФИЦИРОВАННОЙ  
ЭЛЕКТРОННОЙ ПОДПИСЬЮ

Владелец: «НАЦИОНАЛЬНОЕ ОБЪЕДИНЕНИЕ ИЗЫСКАТЕЛЕЙ И  
ПРОЕКТИРОВЩИКОВ» «НОПРИЗ»

129090, г. Москва, пр-т Мира, 3, стр.3

СЕРТИФИКАТ 02 A9 64 C2 00 16 B3 DD A0 42 4E 1C 7B 48 A1 7E 77

ДЕЙСТВИТЕЛЕН: с 10.07.2025 по 10.10.2026



**9710075487-20260216-1016**

(регистрационный номер выписки)

**16.02.2026**

(дата формирования выписки)

## ВЫПИСКА

**из единого реестра сведений о членах саморегулируемых организаций в области инженерных изысканий и в области архитектурно-строительного проектирования и их обязательствах**

**Настоящая выписка содержит сведения о юридическом лице (индивидуальном предпринимателе), выполняющем инженерные изыскания:**

**Государственное автономное учреждение города Москвы Московский научно-исследовательский и проектный институт жилищного хозяйства "МосжилНИИпроект"**

(полное наименование юридического лица/ФИО индивидуального предпринимателя)

**1197746303204**

(основной государственный регистрационный номер)

### 1. Сведения о члене саморегулируемой организации:

|     |   |   |
|-----|---|---|
| 1.1 | Идентификационный номер налогоплательщика                                                                         | 9710075487   |
| 1.2 | Полное наименование юридического лица<br>(Фамилия Имя Отчество индивидуального предпринимателя)                   | Государственное автономное учреждение города Москвы Московский научно-исследовательский и проектный институт жилищного хозяйства "МосжилНИИпроект"            |
| 1.3 | Сокращенное наименование юридического лица                                                                        | ГАУ "МосжилНИИпроект"   |
| 1.4 | Адрес юридического лица<br>Место фактического осуществления деятельности<br>(для индивидуального предпринимателя) | 107078, Россия, Москва, вн.тер.г. муниципальный округ Красносельский, ул. Каланчевская, д. 4/2, стр. 1                                                        |
| 1.5 | Является членом саморегулируемой организации                                                                      | Ассоциация саморегулируемая организация «Центральное объединение организаций по инженерным изысканиям для строительства «Центризыскания» (СРО-И-003-14092009) |
| 1.6 | Регистрационный номер члена саморегулируемой организации                                                          | И-003-009710075487-0097   |
| 1.7 | Дата вступления в силу решения о приеме в члены саморегулируемой организации                                      | 14.10.2009   |
| 1.8 | Дата и номер решения об исключении из членов саморегулируемой организации, основания исключения                   |   |

### 2. Сведения о наличии у члена саморегулируемой организации права выполнять инженерные изыскания:

|   |   |                                                                                                |
|---|---|------------------------------------------------------------------------------------------------|
| 2.1 в отношении объектов капитального строительства (кроме особо опасных, технически сложных и уникальных объектов, объектов использования атомной энергии)<br>(дата возникновения/изменения права) | 2.2 в отношении особо опасных, технически сложных и уникальных объектов капитального строительства (кроме объектов использования атомной энергии)<br>(дата возникновения/изменения права) | 2.3 в отношении объектов использования атомной энергии<br>(дата возникновения/изменения права) |
| Да, 14.10.2009   | Да, 28.06.2023   | Нет                                                                                            |



### 3. Компенсационный фонд возмещения вреда

|     |   |                                                                          |
|-----|---|--------------------------------------------------------------------------|
| 3.1 | Уровень ответственности члена саморегулируемой организации по обязательствам по договору подряда на выполнение инженерных изысканий, в соответствии с которым указанным членом внесен взнос в компенсационный фонд возмещения вреда | Третий уровень ответственности<br>(не превышает триста миллионов рублей) |
| 3.2 | Сведения о приостановлении права выполнять инженерные изыскания объектов капитального строительства   |                                                                          |

### 4. Компенсационный фонд обеспечения договорных обязательств

|     |   |                                                                          |
|-----|---|--------------------------------------------------------------------------|
| 4.1 | Дата, с которой член саморегулируемой организации имеет право выполнять инженерные изыскания по договорам подряда, заключаемым с использованием конкурентных способов заключения договоров, в соответствии с которым указанным членом внесен взнос в компенсационный фонд обеспечения договорных обязательств                    | 01.07.2017                                                               |
| 4.2 | Уровень ответственности члена саморегулируемой организации по обязательствам по договорам подряда на выполнение инженерных изысканий, заключаемым с использованием конкурентных способов заключения договоров, в соответствии с которым указанным членом внесен взнос в компенсационный фонд обеспечения договорных обязательств | Третий уровень ответственности<br>(не превышает триста миллионов рублей) |
| 4.3 | Дата уплаты дополнительного взноса   | 07.03.2019                                                               |
| 4.4 | Сведения о приостановлении права выполнять инженерные изыскания по договорам подряда, заключаемым с использованием конкурентных способов заключения договоров   |                                                                          |

### 5. Фактический совокупный размер обязательств

|     |   |                 |
|-----|---|-----------------|
| 5.1 | Фактический совокупный размер обязательств по договорам подряда на выполнение инженерных изысканий, заключаемым с использованием конкурентных способов заключения договоров на дату выдачи выписки | 7736457.93 руб. |
|-----|---|-----------------|



ДОКУМЕНТ ПОДПИСАН УСИЛЕННОЙ КВАЛИФИЦИРОВАННОЙ  
ЭЛЕКТРОННОЙ ПОДПИСЬЮ

Владелец: «НАЦИОНАЛЬНОЕ ОБЪЕДИНЕНИЕ ИЗЫСКАТЕЛЕЙ И  
ПРОЕКТИРОВЩИКОВ» «НОПРИЗ»

129090, г. Москва, пр-т Мира, 3, стр.3

СЕРТИФИКАТ 02 A9 64 C2 00 16 B3 DD A0 42 4E 1C 7B 48 A1 7E 77

ДЕЙСТВИТЕЛЕН: с 10.07.2025 по 10.10.2026

