



Департамент капитального ремонта города Москвы Государственное автономное учреждение города Москвы Московский научно-исследовательский и проектный институт жилищного хозяйства «МосжилНИИпроект» (ГАУ «МосжилНИИпроект»)

mgnp@mgnp.mos.ru +7 495 624 40 65 107078, г. Москва, ул. Каланчевская, д. 4/2, стр. 1

Арх. №

**Капитальный ремонт здания,
расположенного по адресу:
г. Москва, ул. Мясницкая, дом 44, стр.1**

**Раздел 5. Сведения об инженерном оборудовании,
о сетях и системах инженерно-технического обеспечения.**

Подраздел 5. Сети связи

Часть 6. Система охранного теленаблюдения.

Том 5.5.6

2025-00224-01-0-ИОС5.6

**Капитальный ремонт здания,
расположенного по адресу:
г. Москва, ул. Мясницкая, дом 44, стр.1**

**Раздел 5. Сведения об инженерном оборудовании,
о сетях и системах инженерно-технического обеспечения.**

Подраздел 5. Сети связи

Часть 6. Система охранного теленаблюдения.

Том 5.5.6

2025-00224-01-0-ИОС5.6

Начальник ОПИС №1

ГИП




Д.П. Белоусова

07.04.2026

В.Ю. Гунченко

07.04.2026

Содержание раздела

[illegible]

Согласовано

Взам. Инв. №

Подп. И дата

Инв. № подл.

						2025-00224-01-0-ИОС5.6			
Изм.	Кол.уч	Лист	№ док.	Подп.	Дата	Здания и помещения по адресу: г. Москва, ул. Мясницкая, д.44, стр.1	Стадия	Лист	Листов
Разработал		Роянцева А.А.			01.2026		П	1	1
Зав. сектор		Роянцева А.А.			01.2026				
Н.контроль		Роянцева А.А.			01.2026				
Нач.ОПИС№1		Белуосова Д.П.			01.2026				
							МОСЖИЛ НИИПРОЕКТ		

Состав проектной документации

Смотри том 1.1, 2025-00224-01-0-СП, Часть1. Раздел1. Состав проектной документации.

[illegible]

- совместную работу с системами контроля и управления доступом, охранной сигнализации;
- автоматический вывод изображений с телекамер по сигналу средств телевизионного обнаружения или иных технических средств охраны;
- разграничение полномочий доступа к управлению и видеоинформации с целью предотвращения несанкционированных действий;
- воспроизведение ранее записанной информации;
- оперативный доступ к видеозаписи и видеоархиву путем задания времени, даты и идентификатора телекамеры.
- круглосуточное наблюдение и возможность постоянной автоматической записи видеоинформации от установленных камер видеонаблюдения (глубина архива не менее 31 суток);

В состав системы входят:

- автоматизированное рабочее место, моноблок AQone T927, Aquarius – 1 шт.;
- видеорегистратор до 32 IP-видеокамер, RVi-2NR32481 – 1 шт.;
- коммутатор сетевой RVi-NS2404M – 1 шт.;
- патч-панель, 5е cat., 24 порта – 1 шт.;
- устройство защиты Ethernet в комплекте 19" - 1 компл.;
- источник электропитания бесперебойный, SKAT-UPS 1500-RACK-ON-3X9-E P3 – 1 шт.;
- шкаф Cabeus монтажный телекоммуникационный 19" напольный для распределительного и серверного оборудования 32U 600x600x1610mm (ШxГxВ) SH-05C-32U60/60 – 1 комп.;
- IP-Видеокамера цилиндрическая RVi-1NCT4053 (2.8-12) – 7 шт.;
- IP-Видеокамера купольная RVi-1NCD4054 (2.8) white – 10 шт.;

IP-Видеокамеры цилиндрические предназначены для наблюдения за периметром и близлежащей территорией здания. IP-Видеокамеры цилиндрические устанавливаются на фасаде здания на высоте не менее 3 м, на фасаде рядом со входами в здание на высоте не менее 2,2 м

IP-Видеокамеры купольные предназначены для наблюдения за помещениями охраняемого здания.

IP-Видеокамеры купольные устанавливаются на потолке, на стене на высоте не менее 2,2 м, учитывая местные условия помещения.

Для сбора видеопотока от видеокамер устанавливается сетевой коммутатор с поддержкой PoE.

Глубина видеоархива составляет не менее 31 суток записи в режиме детектора движения.

Серверное и активное сетевое оборудование, совместно с источником бесперебойного питания и блоком распределения питания устанавливаются в монтажный телекоммуникационный шкаф Cabeus 19" напольный 32U 600x600x1610mm (ШxГxВ) передняя стеклянная и задняя сплошная металлическая двери, ручка с замком, цвет серый (RAL 7035).

СОТ обеспечивает круглосуточное наблюдение в режиме реального времени с установленных видеокамер при разрешении не менее 1920x1080 пикселей в режиме не менее 25 к/с, с учетом места установки (внутренняя/внешняя) с инфракрасной подсветкой, подогревом в зимний период, а также защиту от внешних атмосферных воздействий (пыль, вода) в соответствии со стандартом IP66 и выше и эксплуатацией в условиях температур от минус 40°С до 50°С. Питание камеры по кабелю Ethernet (PoE).

Взам. инв. №							Лист
Подп. и дата							2025-00224-01-0-ИОС5.6
Инв. № подл.							2
	Изм.	Кол.уч	Лист	№ док	Подп.	Дата	

Источник бесперебойного питания обеспечивает бесперебойную работу оборудования, в отсутствие электропитания 220В, от аккумуляторных батарей в течение не менее 10 минут. Переход с основного на резервное электропитание происходит автоматически при пропадании основного питания.

Кабели прокладывают по лоткам, в гофре и коробах. Открытая прокладка кабелей запрещена.

Заземление оборудования СОР осуществить путем присоединения металлических токоведущих частей оборудования к нулевому (защитному) проводу сети электропитания согласно ПУЭ разд. 1.7 и 7.1.

Оборудование и материалы, применяемые в проекте, соответствуют требованиям государственных стандартов и технических условий и имеют сертификаты соответствия и пожарной безопасности.

В соответствии с требованиями п.5.2.4 СП 2.13130.2020, места пересечения кабелей, кабеленесущих конструкций со строительными конструкциями с нормируемыми пределами огнестойкости, обеспечиваются проходками не ниже пределов огнестойкости, установленных для пересекаемых конструкций посредством установки гильз из труб с заделкой гидроизоляционной огнеупорной мастикой в соответствии с ГОСТ 30247.1, ГОСТ Р 53306, ГОСТ Р 53310.

3. Электроснабжение

По степени надежности электроснабжения системы СОР относятся к 1-ой категории потребителей.

Защита электрических цепей должна быть выполнена в соответствии с ПУЭ. Защитное заземление электрооборудования, металлических каркасов и конструкций следует выполнить в соответствии с ПУЭ и технической документацией на оборудование.

Инв. № подл.	Подп. и дата	Взам. инв. №							Лист
			2025-00224-01-0-ИОС5.6						
			3						
Изм.	Кол.уч	Лист	№ док	Подп.	Дата				

3. **Перечень нормативных документов, использованных при разработке проектной документации**

- **ПП № 87 от 16.02.2008 г. (с изменениями на 21 октября 2025 года)** «Составе разделов проектной документации и требования к их содержанию»;
- **ГОСТ 21.101-2020 «СПДС. Основные требования к проектной и рабочей документации»;**
- **ГОСТ 2.105-2019 «Единая система конструкторской документации. Общие требования к текстовым документам»;**
- **ГОСТ Р 51558-2014 «Средства и системы охранные телевизионные. Классификация. Общие технические требования. Методы испытаний»**
- **СП 1.13330.2022 «Системы электросвязи зданий и сооружений. Основные положения проектирования»;**
- **СП 118.13330.2022 «Общественные здания и сооружения»;**
- **ГОСТ 31565-2012 Кабельные изделия. Требования пожарной безопасности**
- **ПУЭ, издание 7 «Правила устройств электроустановок»;**
- **СП 118.13330.2022 «Общественные здания и сооружения»;**

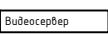
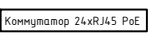
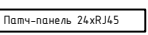
Дополнительные требования в части касающейся обеспечения мероприятий антитеррористической защищенности, требований по созданию структурированных кабельных систем, требований к помещениям для размещения серверной, режимных помещений, а также рекомендации Генеральной прокуратуры Российской Федерации:

1. Требования по созданию структурированных кабельных систем;
2. Типовые требования по созданию структурированных кабельных систем в органах и организациях прокуратуры Российской Федерации;
3. Требования при проведении ремонтных работ в серверном помещении;
4. Концепция безопасности органов и организаций прокуратуры Российской Федерации;
5. Рекомендации Генеральной прокуратуры Российской Федерации - система охранного видеонаблюдения, система контроля и управления доступом, система охранной сигнализации, система пожарной сигнализации;
6. Рекомендации Генеральной прокуратуры по инженерным телекоммуникационным системам;
7. Требования к помещениям приема граждан;
8. Требования к режимным помещениям;
9. Свод правил. Здания прокуратур. Правила проектирования;
10. Требования на предмет обеспечения антитеррористической защищенности;
11. Требования проведения работ по монтажу зарядных станций для электромобилей.

Данный список требований минимальный, обязательный, но не исчерпывающий.

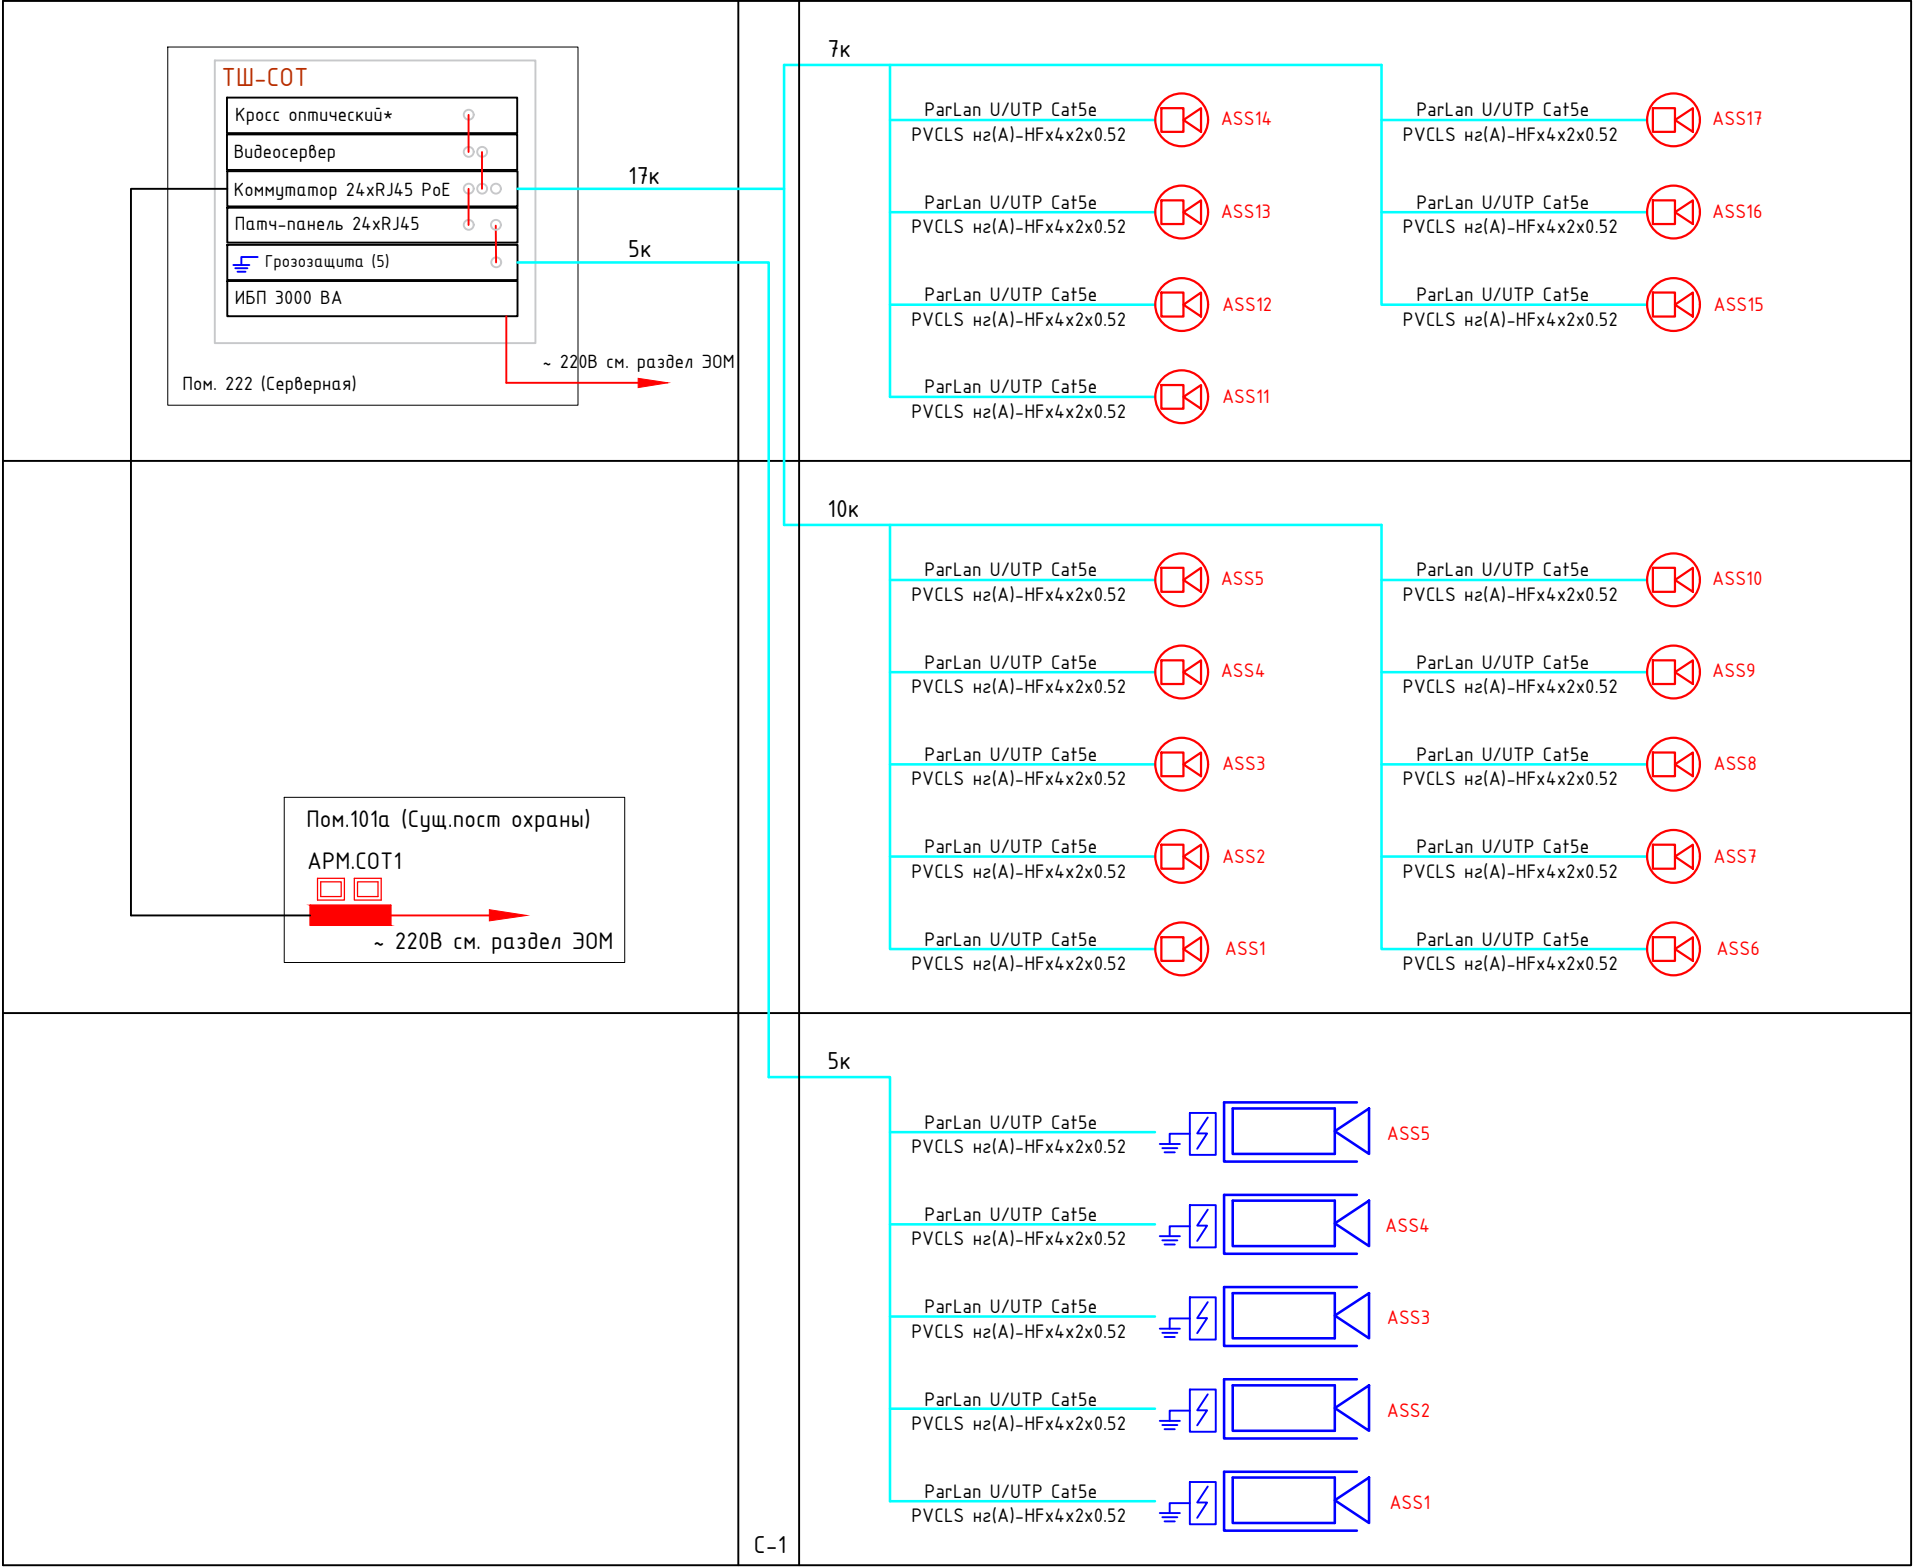
Взам. инв. №	Подп. и дата	Инв. № подл.							2025-00224-01-0-ИОС5.6	Лист
										4
			Изм.	Кол.уч	Лист	№ док	Подп.	Дата		

Условные обозначения

Обозначение	Название	примечание
 ТШ-СОТ	Телекоммуникационный шкаф	
	ПК сотрудника охраны	
 Видеосервер	Видеосервер	
 Коммутатор 24xRJ45 PoE	Коммутатор доступа, с указанием кол. портов (48)	
 Патч-панель 24xRJ45	Патч-панель, с указанием кол. возможных и реальных подключений – 48(20)	
	Видеокамера по фасаду	
	Купольная IP-видеокамера	
	Грозозащита	
	Кабель UTP кат. 5е	

						2025-00224-01-0-ИОС 5.6			
						Здания и помещения по адресу: г. Москва ул. Мясницкая, д.44, стр.1			
Изм.	Кол.уч.	Лист	№ док.	Подпись	Дата				
Разработал	Роянцева А.А.				11.03.26	Капитальный ремонт	Стадия	Лист	Листов
Зав.сектора	Роянцева А.А.				11.03.26		П	1	5
						Условные обозначения		МОСЖИЛ НИИПРОЕКТ	
Норм.Контр.	Роянцева А.А.				11.03.26				
Нач.ОПИС №1	Белоусова Д.П.				11.03.26				

Принципиальная схема охранного теленаблюдения



IP-видеокамера цилиндрическая ASS
RVi-1NCT4053 (2.8-12) с монтажной
коробкой RVi-1BMB-10 white



IP-видеокамера купольная ASS
RVi-1NCD4054 (2.8) white

						2025-00224-01-0-ИОС 5.6		
						Здания и помещения по адресу: г. Москва ул. Мясницкая, д.44, стр.1		
Изм.	Кол.уч.	Лист	№ док.	Подпись	Дата	Капитальный ремонт	Стадия	Лист
Разработал	Роянцева А.А.				11.03.26			Листов
Зав.сектора	Роянцева А.А.				11.03.26		П	2
								5
Норм.Контр.	Роянцева А.А.				11.03.26	Принципиальная схема СОТ		
Нач.ОПИС №1	Белуцова Д.П.				11.03.26			

M 1:100

ASS1

ASS2

ASS3

ASS4

101

101A

102

103

103

103

104

105

106

107

108

109

110

111

112

113

114

115

116

117

118

119

120

121

+0.00

+0.00

+0.00

+0.21

+0.25

+0.30

3990

6485

4835

3100

6540

6850

5210

8785

2000

2300

1550

Экспликация помещений 1-го этажа			
№ п/п	Наименование помещений	Площадь м ²	Кат. пом.
101	Лестница №1 (ЛК ти 1)	22,9	
101А	Пост охраны		
102	Лестница № 2 (ЛК тип 1)	17,7	
103	Коридор	39,4	
104	Кабинет заместителя прокурора	15,9	
105	Комната отдыха заместителя прокурора	5,3	
106	Кабинет помощника прокурора / прием граждан МГН	25,6	
107	Кабинет*	4,8	
108	Архив	7,9	В4
109	Ввод водопровода	4,3	
110	Кабинет для приема граждан	4,9	
111	Санузел	1,8	
112	Санузел МГН	6,7	
113	Санузел заместителя прокурора	2,8	
	ИТОГО:	160	

Помещения не входящие в зону ремонта			
N п/п	Наименование помещений	Площадь м ²	Кат. пом.
114	Офисное помещение	15,7	
115	Офисное помещение	15,6	
116	Офисное помещение	23,0	
117	Офисное помещение	13,8	
118	Офисное помещение	13,8	
119	Офисное помещение	17,0	
120	Офисное помещение	9,4	
121	Офисное помещение	10,1	
	ИТОГО:	118.4	

1. В здании предусматривается капитальный ремонт, размеры проемов в капитальных стенах увеличению не подлежат.

						2025-00224-01-0-ИОС 5.6			
						Здания и помещения по адресу: г. Москва ул. Мясницкая, д.44, стр.1			
Изм.	Колуч.	Лист	№ док.	Подпись	Дата	Капитальный ремонт	Стадия	Лист	Листов
Разработал	Роянцева А.А.				11.03.26		П	3	
Зав.сектора	Роянцева А.А.				11.03.26				
						План 1-го этажа. Камеры по фасаду		МОСЖИЛ НИИПРОЕКТ	
Норм.Контр.	Роянцева А.А.				11.03.26				
Нач. ОПИС №1	Белюсова Д.П.				11.03.26				



**МОСЖИЛ
НИИПРОЕКТ**

Формат ФОРМАТ

Помещения не входящие в зону ремонта			
№ п/п	Наименование помещений	Площадь м ²	Кат. пом.
114	Офисное помещение	15,7	
115	Офисное помещение	15,6	
116	Офисное помещение	23,0	
117	Офисное помещение	13,8	
118	Офисное помещение	13,8	
119	Офисное помещение	17,0	
120	Офисное помещение	9,4	
121	Офисное помещение	10,1	
	ИТОГО:	118,4	

*

1. В здании предусматривается капитальный ремонт, размеры проемов в капитальных стенах увеличению не подлежат.

ASS 



**МОСЖИЛ
НИИПРОЕКТ**

[illegible]

Экспликация помещений 2-го этажа			
№ п/п	Наименование помещений	Площадь м ²	Кат. пом.
201	Лестница № 1 (ЛК тип 1)	23,1	
202	Лестница № 2 (ЛК тип 1)	22,8	
203	Коридор	34,2	
204	Приемная прокурора	14,5	
205	Кабинет прокурора / видеонаблюдение	25,9	
206	Комната отдыха прокурора	12,3	
207	Сан. узел прокурора	3,5	
208	Кабинет 1-го заместителя прокурора	14,1	
209	Комната отдыха 1-го заместителя прокурора	5,0	
210	Сан. узел 1-го заместителя прокурора	2,6	
211	Кабинет помощника прокурора	15,9	
212	Кабинет помощника прокурора	14,0	
213	Кабинет помощника прокурора	13,7	
214	Архив	10,3	ВЗ
215	Кабинет помощника прокурора	16,4	
216	Кабинет помощника прокурора	17,0	
217	Зал совещаний	16,7	
218	Кабинет помощника прокурора	9,5	
219	Кабинет помощника прокурора	8,9	
220	Комната приrema пищи	9,5	
221	Санузел	2,5	
222	Серверная	7,6	ВЗ
	Итого:	300	

1. В здании предусматривается капитальный ремонт, размеры проемов в капитальных стенах увеличению не подлежат.

ASS1  IP-видеокамера купольная ASS RVi-1NCD4054
(2.8) white

						2025-00224-01-0-ИОС.6			
						Здания и помещения по адресу: г. Москва ул. Мясницкая, д.44, стр.1			
Изм.	Кол.уч.	Лист	№ док.	Подпись	Дата	Капитальный ремонт	Стадия	Лист	Листов
Разработал	Роянцева А.А			<i>Р.А. Роянцева</i>	11.03.26		П	5	5
Зав.сектора	Роянцева А.А			<i>Р.А. Роянцева</i>	11.03.26				
Норм.Контр.	Роянцева А.А.			<i>Р.А. Роянцева</i>	11.03.26	План 2-го этажа. СОТ			
Нач.ОПИС №1	Белогосова Д.П.			<i>Д.П. Белогосова</i>	11.03.26				

																		16	
Позиция		Наименование и техническая характеристика		Тип, марка, обозначение документа, опросного листа		Код оборудования, изделия, материала		Завод-изготовитель		Единица измерения		Количество		Масса, единицы, кг		Примечание			
1		2		3		4		5		6		7		8		9			
		Оборудование:																	
1		Цилиндрическая IP-видеокамера с фиксированным объективом IP 4 Мп; размер матрицы 1/2.9"; встроенный микрофон; Дальность ИК подсветки 80м; режим "день/ночь"; PoE 7 Вт; -40 ~ +60°C,		RVi-1NCT4053 (2.8-12)				RVi, Россия		компл.		5							
2		Устройство грозозащиты		NST NS-LP-1GP/D						шт		5							
3		IP-видеокамера купольная 4Мп с фиксированным объективом 2,8мм		RVi-1NCD4054 (2.8) white				RVi, Россия		шт		17							
4		Видеорегистратор до 32 IP-видеокамер		RVi-2NR32481				RVi, Россия		шт		1							
5		Коммутатор сетевой		RVi-NS2404M				RVi, Россия		шт		1							
6		Устройство защиты Ethernet в комплекте:																	
		- модуль защиты		PG4-12LSA				Информационные системы		шт		1							
		- универсальный корпус 19"						Информационные системы		шт		1							
7		Автоматизированное рабочее место, моноблок		AQone T927				Aquarius		компл.		1							
8		Комплект проводных клавиатуры и мыши								компл.		1							
9		ИБП 1500 Вт, On-Line, синус, встр. АКБ 36В (3x9Ач), 8xС13		SKAT-UPS 1500-RACK-ON-3X9-E P3				Бастуон		шт		1							
		Материалы и кабельные изделия																	
1		1U патч-панель кат.5E UTP 24 порта (Dual IDC) высокой плотности		PP24-1UC5EU-D05-1				ИТК		шт		1							
		Кабельные изделия																	
2		Кабель витая пара U/UTP в общем экране, cat 5e, 4x2x0.52, оболочка из ПВХ пластика повышенной пожарной опасности с низким дымо- и газовыделением, цвет оболочки зеленый		ParLan U/UTP Cat5e PVCLS нз(А)-HFx4x2x0.52				ООО "НПП Спецкабель"		м.		1300							
3		Коммутационный шнур (патч-корд) кат.5E UTP LSZH 1м синий		PC03-C5EUL-1M				ИТК		шт		27							
4		Гофротруба d-20мм						ООО "НПП Спецкабель"		м.		1000							
5		Короб электротехнический 10x12 ПВХ 2м								м.		300							
6		Металлорукав герметичный в ПВХ изоляции		P3-ЦПнг-20 с протяжкой						м.		10							
7		Изолирующий колпачек для разъемов RG45								шт		30							
8		Монтажная коробка для цилиндрических камер на стену		RVi-1BMB-10 white				RVi, Россия		шт		5							
</																			

9710075487-20260216-1017

(регистрационный номер выписки)

16.02.2026

(дата формирования выписки)

ВЫПИСКА

из единого реестра сведений о членах саморегулируемых организаций в области инженерных изысканий и в области архитектурно-строительного проектирования и их обязательствах

Настоящая выписка содержит сведения о юридическом лице (индивидуальном предпринимателе), осуществляющем подготовку проектной документации:

Государственное автономное учреждение города Москвы Московский научно-исследовательский и проектный институт жилищного хозяйства «МосжилНИИпроект»

(полное наименование юридического лица/ФИО индивидуального предпринимателя)

1197746303204

(основной государственный регистрационный номер)

1. Сведения о члене саморегулируемой организации:

1.1	Идентификационный номер налогоплательщика	9710075487
1.2	Полное наименование юридического лица (Фамилия Имя Отчество индивидуального предпринимателя)	Государственное автономное учреждение города Москвы Московский научно-исследовательский и проектный институт жилищного хозяйства «МосжилНИИпроект»
1.3	Сокращенное наименование юридического лица	ГАУ «МосжилНИИпроект»
1.4	Адрес юридического лица Место фактического осуществления деятельности (для индивидуального предпринимателя)	107078, Россия, Москва, г. Москва, Каланчевская, 4/2, 1, -
1.5	Является членом саморегулируемой организации	Ассоциация проектировщиков инженерной инфраструктуры «Инфрадизайн» (СРО-П-218-15012021)
1.6	Регистрационный номер члена саморегулируемой организации	П-218-009710075487-0095
1.7	Дата вступления в силу решения о приеме в члены саморегулируемой организации	18.06.2021
1.8	Дата и номер решения об исключении из членов саморегулируемой организации, основания исключения	

2. Сведения о наличии у члена саморегулируемой организации права осуществлять подготовку проектной документации:

2.1 в отношении объектов капитального строительства (кроме особо опасных, технически сложных и уникальных объектов, объектов использования атомной энергии) (дата возникновения/изменения права)	2.2 в отношении особо опасных, технически сложных и уникальных объектов капитального строительства (кроме объектов использования атомной энергии) (дата возникновения/изменения права)	2.3 в отношении объектов использования атомной энергии (дата возникновения/изменения права)
Да, 18.06.2021	Нет	Нет



3. Компенсационный фонд возмещения вреда

3.1	Уровень ответственности члена саморегулируемой организации по обязательствам по договору подряда на подготовку проектной документации, в соответствии с которым указанным членом внесен взнос в компенсационный фонд возмещения вреда	Третий уровень ответственности (не превышает триста миллионов рублей)
3.2	Сведения о приостановлении / прекращении права осуществлять подготовку проектной документации объектов капитального строительства	

4. Компенсационный фонд обеспечения договорных обязательств

4.1	Дата, с которой член саморегулируемой организации имеет право осуществлять подготовку проектной документации по договорам подряда, заключаемым с использованием конкурентных способов заключения договоров, в соответствии с которым указанным членом внесен взнос в компенсационный фонд обеспечения договорных обязательств	18.06.2021
4.2	Уровень ответственности члена саморегулируемой организации по обязательствам по договорам подряда на подготовку проектной документации, заключаемым с использованием конкурентных способов заключения договоров, в соответствии с которым указанным членом внесен взнос в компенсационный фонд обеспечения договорных обязательств	Четвертый уровень ответственности (составляет триста миллионов рублей и более)
4.3	Дата уплаты дополнительного взноса	Нет
4.4	Сведения о приостановлении / прекращении права осуществлять подготовку проектной документации по договорам подряда, заключаемым с использованием конкурентных способов заключения договоров	

5. Фактический совокупный размер обязательств

5.1	Фактический совокупный размер обязательств по договорам подряда на подготовку проектной документации, заключаемым с использованием конкурентных способов заключения договоров на дату выдачи выписки	399883177 руб.
-----	--	----------------



ДОКУМЕНТ ПОДПИСАН УСИЛЕННОЙ КВАЛИФИЦИРОВАННОЙ
ЭЛЕКТРОННОЙ ПОДПИСЬЮ

Владелец: «НАЦИОНАЛЬНОЕ ОБЪЕДИНЕНИЕ ИЗЫСКАТЕЛЕЙ И
ПРОЕКТИРОВЩИКОВ» «НОПРИЗ»

129090, г. Москва, пр-т Мира, 3, стр.3

СЕРТИФИКАТ 02 A9 64 C2 00 16 B3 DD A0 42 4E 1C 7B 48 A1 7E 77

ДЕЙСТВИТЕЛЕН: с 10.07.2025 по 10.10.2026



9710075487-20260216-1016

(регистрационный номер выписки)

16.02.2026

(дата формирования выписки)

ВЫПИСКА

из единого реестра сведений о членах саморегулируемых организаций в области инженерных изысканий и в области архитектурно-строительного проектирования и их обязательствах

Настоящая выписка содержит сведения о юридическом лице (индивидуальном предпринимателе), выполняющем инженерные изыскания:

Государственное автономное учреждение города Москвы Московский научно-исследовательский и проектный институт жилищного хозяйства "МосжилНИИпроект"

(полное наименование юридического лица/ФИО индивидуального предпринимателя)

1197746303204

(основной государственный регистрационный номер)

1. Сведения о члене саморегулируемой организации:

1.1	Идентификационный номер налогоплательщика	9710075487
1.2	Полное наименование юридического лица (Фамилия Имя Отчество индивидуального предпринимателя)	Государственное автономное учреждение города Москвы Московский научно-исследовательский и проектный институт жилищного хозяйства "МосжилНИИпроект"
1.3	Сокращенное наименование юридического лица	ГАУ "МосжилНИИпроект"
1.4	Адрес юридического лица Место фактического осуществления деятельности (для индивидуального предпринимателя)	107078, Россия, Москва, вн.тер.г. муниципальный округ Красносельский, ул. Каланчевская, д. 4/2, стр. 1
1.5	Является членом саморегулируемой организации	Ассоциация саморегулируемая организация «Центральное объединение организаций по инженерным изысканиям для строительства «Центризыскания» (СРО-И-003-14092009)
1.6	Регистрационный номер члена саморегулируемой организации	И-003-009710075487-0097
1.7	Дата вступления в силу решения о приеме в члены саморегулируемой организации	14.10.2009
1.8	Дата и номер решения об исключении из членов саморегулируемой организации, основания исключения	

2. Сведения о наличии у члена саморегулируемой организации права выполнять инженерные изыскания:

2.1 в отношении объектов капитального строительства (кроме особо опасных, технически сложных и уникальных объектов, объектов использования атомной энергии) (дата возникновения/изменения права)	2.2 в отношении особо опасных, технически сложных и уникальных объектов капитального строительства (кроме объектов использования атомной энергии) (дата возникновения/изменения права)	2.3 в отношении объектов использования атомной энергии (дата возникновения/изменения права)
Да, 14.10.2009	Да, 28.06.2023	Нет



3. Компенсационный фонд возмещения вреда

3.1	Уровень ответственности члена саморегулируемой организации по обязательствам по договору подряда на выполнение инженерных изысканий, в соответствии с которым указанным членом внесен взнос в компенсационный фонд возмещения вреда	Третий уровень ответственности (не превышает триста миллионов рублей)
3.2	Сведения о приостановлении права выполнять инженерные изыскания объектов капитального строительства	

4. Компенсационный фонд обеспечения договорных обязательств

4.1	Дата, с которой член саморегулируемой организации имеет право выполнять инженерные изыскания по договорам подряда, заключаемым с использованием конкурентных способов заключения договоров, в соответствии с которым указанным членом внесен взнос в компенсационный фонд обеспечения договорных обязательств	01.07.2017
4.2	Уровень ответственности члена саморегулируемой организации по обязательствам по договорам подряда на выполнение инженерных изысканий, заключаемым с использованием конкурентных способов заключения договоров, в соответствии с которым указанным членом внесен взнос в компенсационный фонд обеспечения договорных обязательств	Третий уровень ответственности (не превышает триста миллионов рублей)
4.3	Дата уплаты дополнительного взноса	07.03.2019
4.4	Сведения о приостановлении права выполнять инженерные изыскания по договорам подряда, заключаемым с использованием конкурентных способов заключения договоров	

5. Фактический совокупный размер обязательств

5.1	Фактический совокупный размер обязательств по договорам подряда на выполнение инженерных изысканий, заключаемым с использованием конкурентных способов заключения договоров на дату выдачи выписки	7736457.93 руб.
-----	--	-----------------



ДОКУМЕНТ ПОДПИСАН УСИЛЕННОЙ КВАЛИФИЦИРОВАННОЙ
ЭЛЕКТРОННОЙ ПОДПИСЬЮ

Владелец: «НАЦИОНАЛЬНОЕ ОБЪЕДИНЕНИЕ ИЗЫСКАТЕЛЕЙ И
ПРОЕКТИРОВЩИКОВ» «НОПРИЗ»

129090, г. Москва, пр-т Мира, 3, стр.3

СЕРТИФИКАТ 02 A9 64 C2 00 16 B3 DD A0 42 4E 1C 7B 48 A1 7E 77

ДЕЙСТВИТЕЛЕН: с 10.07.2025 по 10.10.2026

